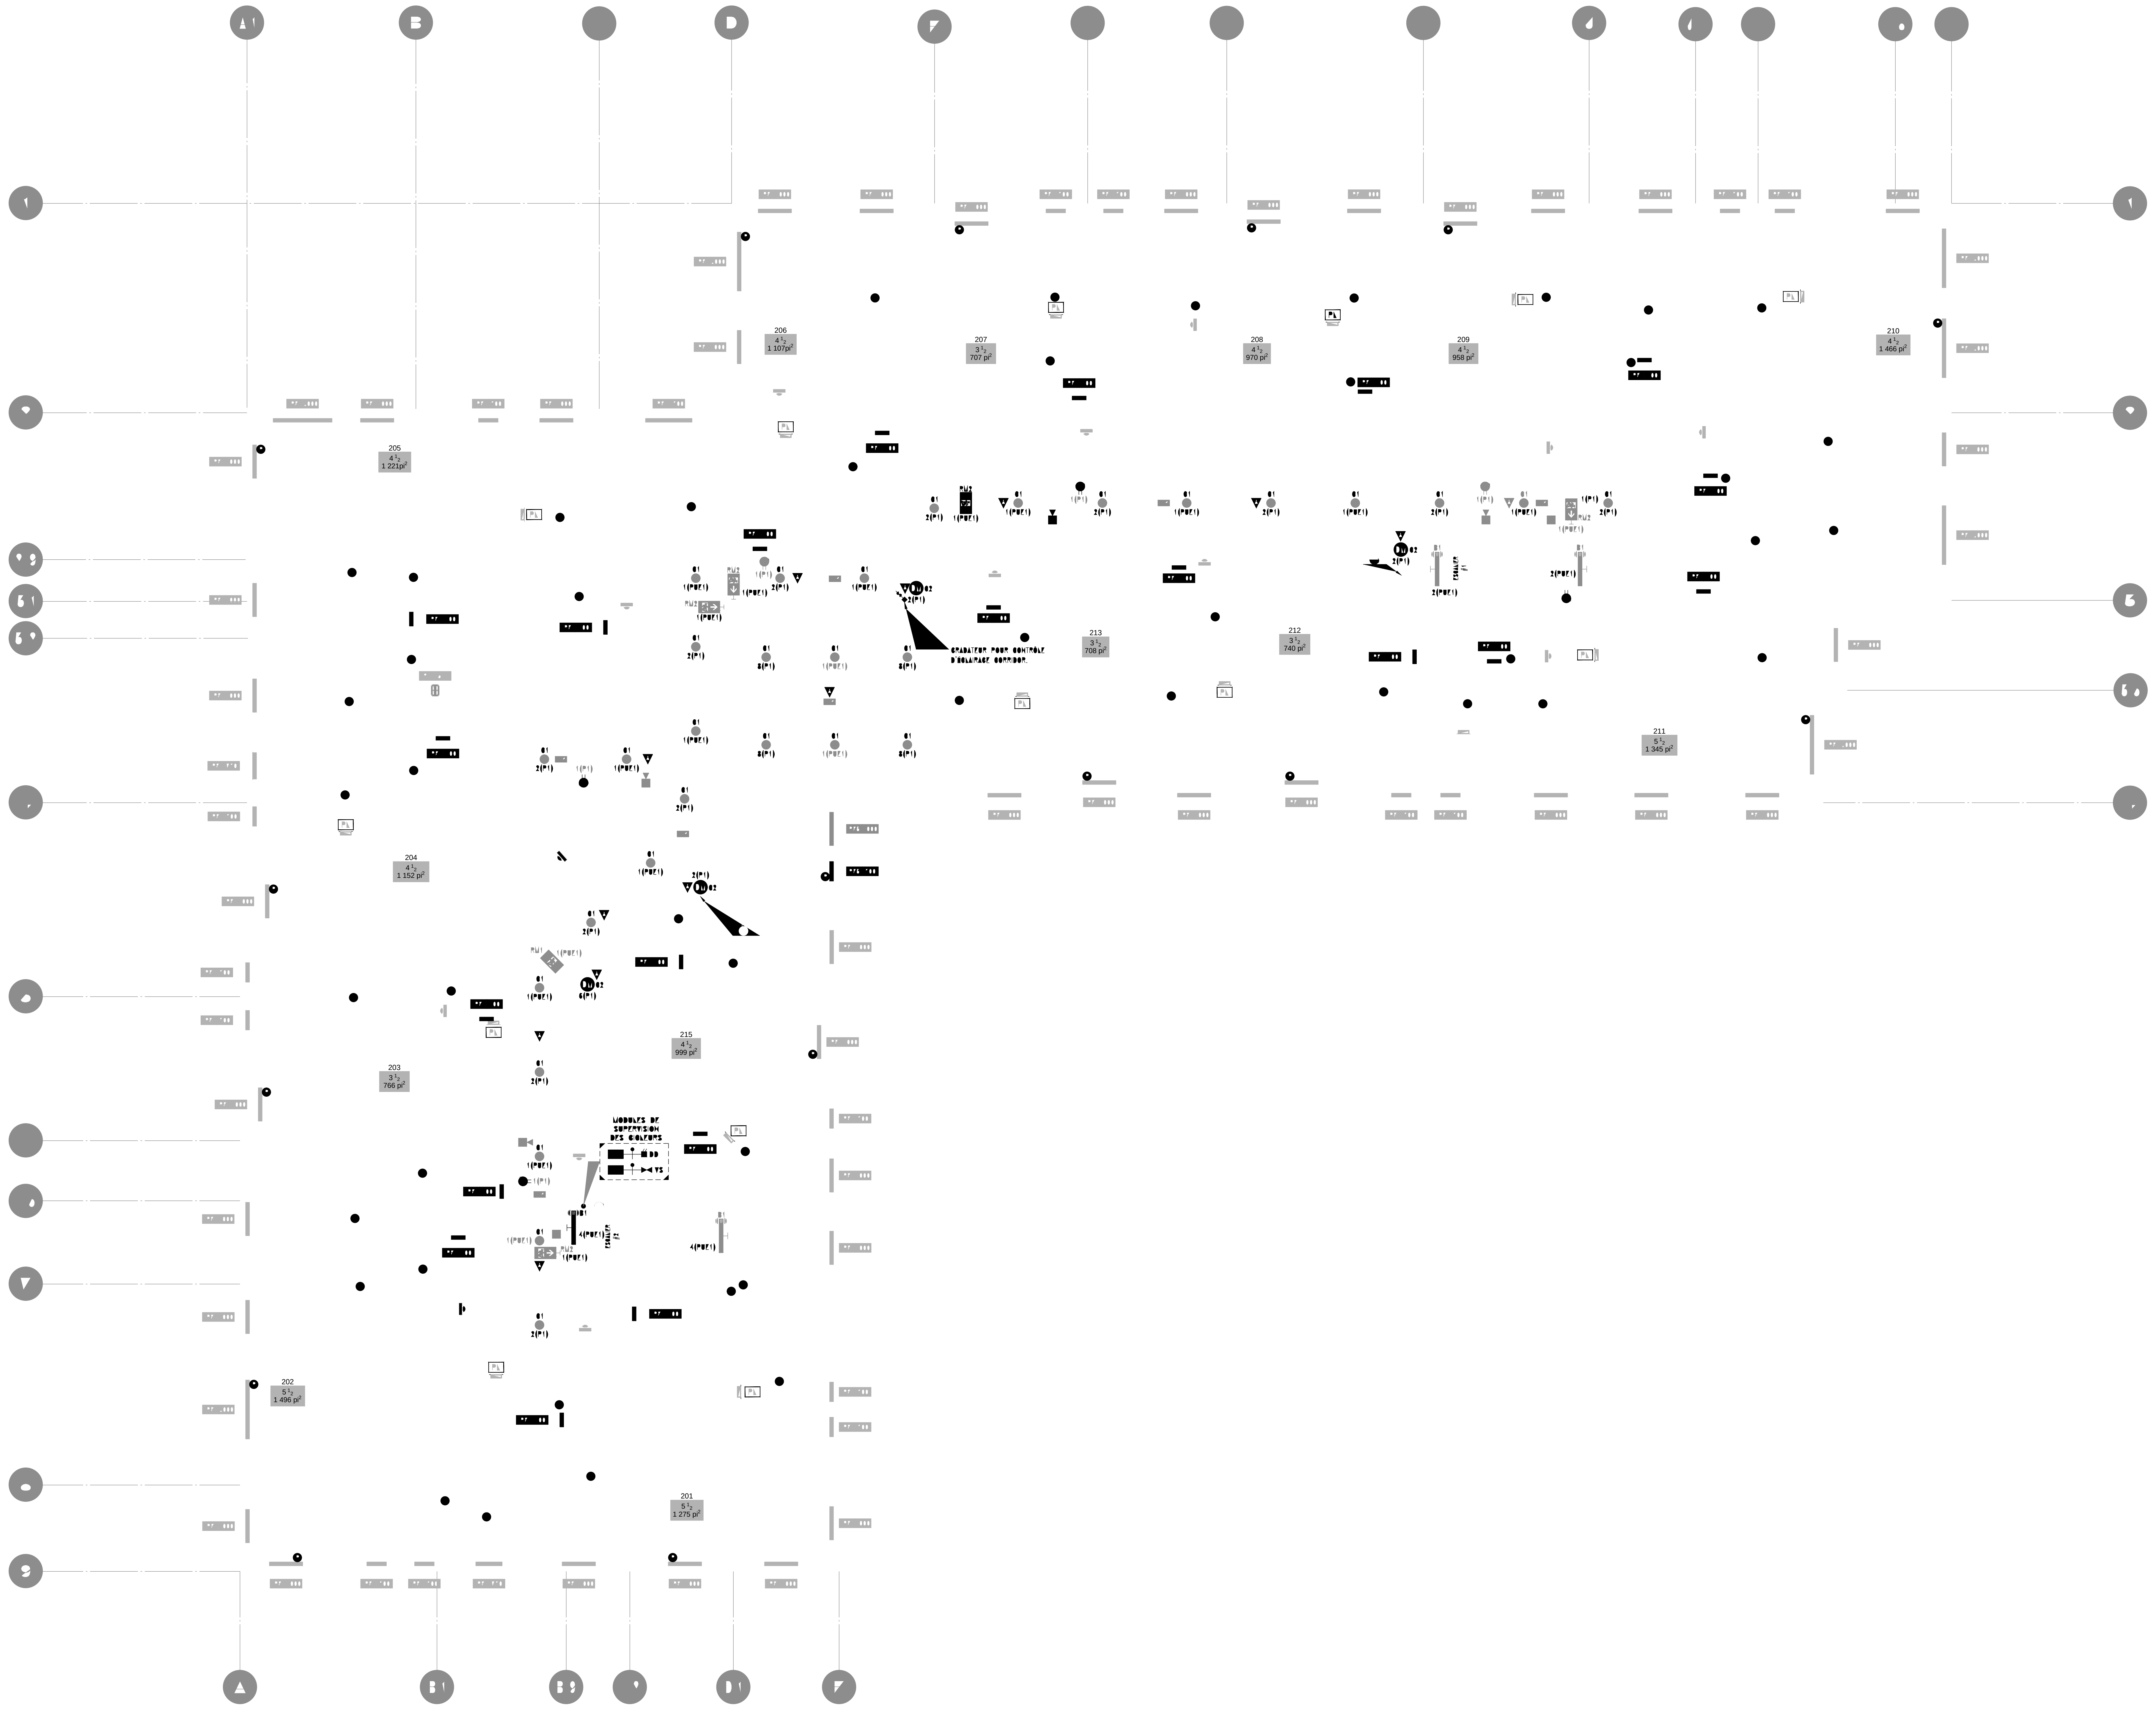
206
4½
1 107pi²
207
3½
707 pi²
208
4½
970 pi²
209
4½
958 pi²
210
4½
1 466 pi²
205
4½
1 221pi²
213
3½
708 pi²
212
3½
740 pi²
211
5½
1 345 pi²
204
4½
1 152 pi²
215
4½
999 pi²
203
3½
766 pi²
202
5½
1 496 pi²
201
5½
1 275 pi²
GRADATEUR POUR CONTRÔLE D'ÉCLAIRAGE CORRIDOR.
MODULES DE SUPERVISION DES GICLEURS
DD
VS
ESCALIER #1
ESCALIER #2
RM2
DM