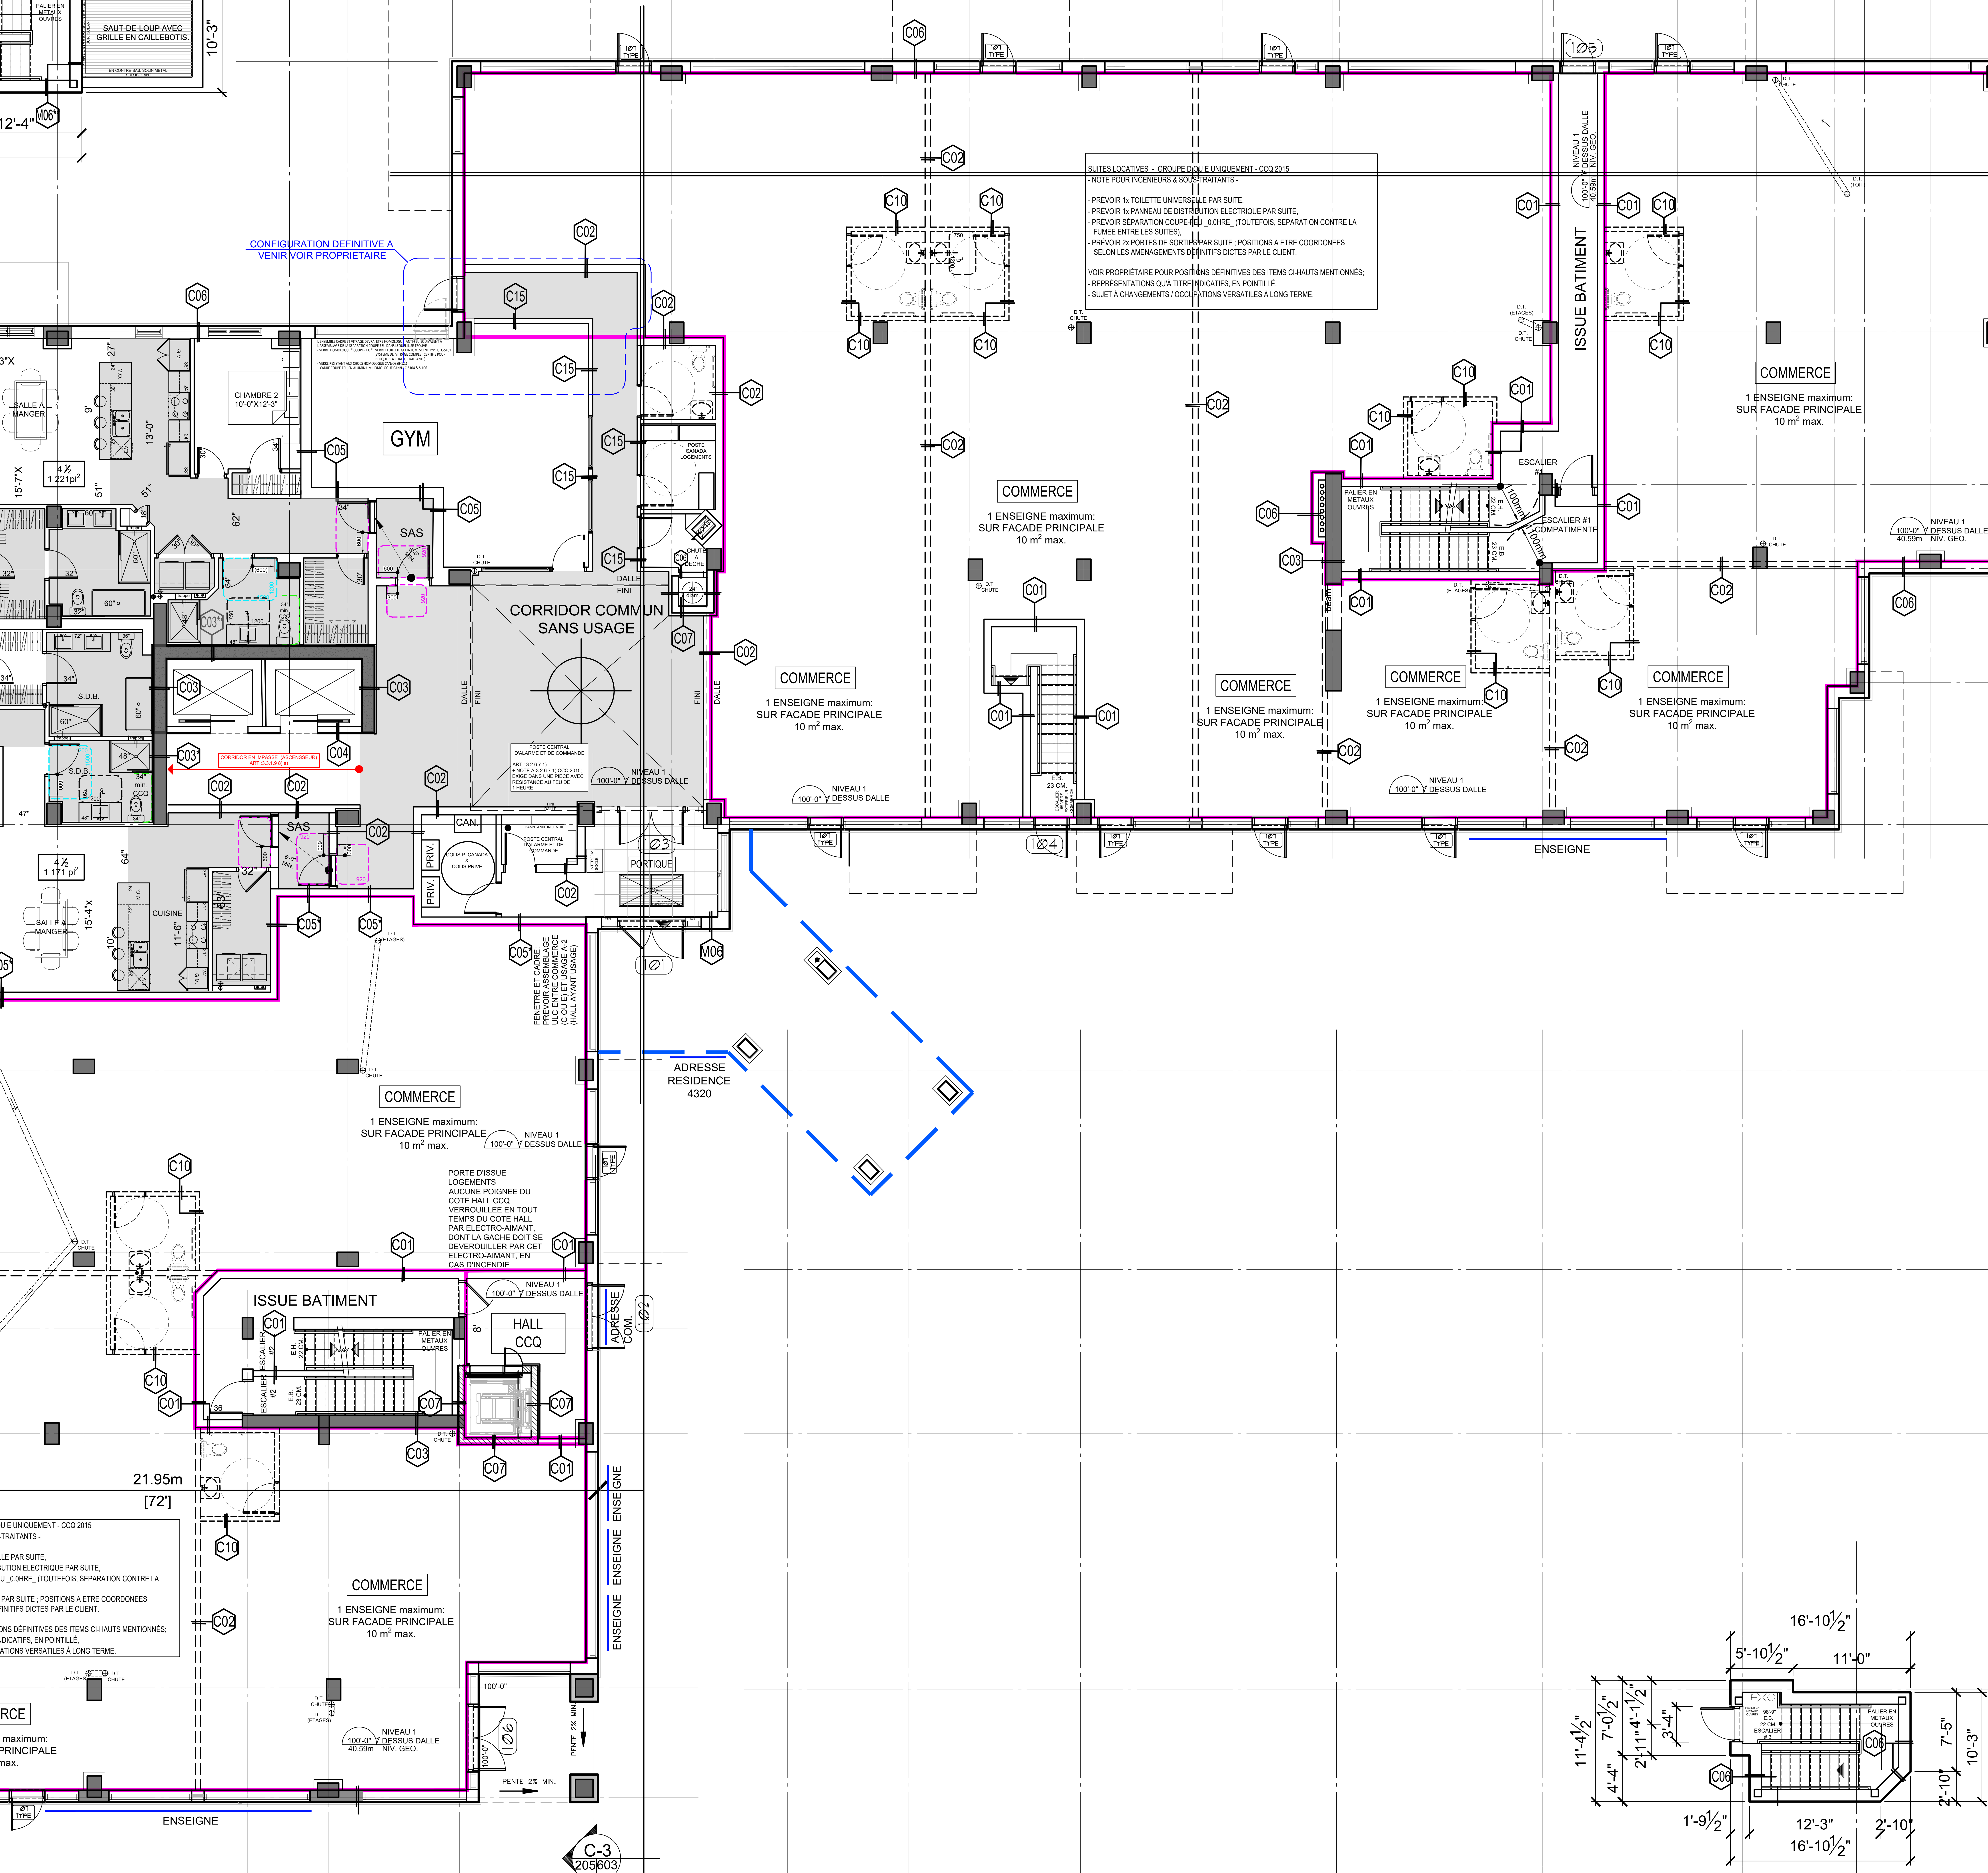
PALIER EN METAUX OUVRES
SAUT-DE-LOUP AVEC GRILLE EN CAILLEBOTIS.
EN CONTRE BAS; SOLIN METAL SUR ISOLANT
10'-3"
12'-4"
M06**
C06
C02
C10
C01
C15
C05
C03
C03*
C04
C07
C06
M06
C05*
101
102
103
104
105
106
101 TYPE
CONFIGURATION DEFINITIVE A VENIR VOIR PROPRIETAIRE
GYM
CHAMBRE 2 10'-0"X12'-3"
SALLE A MANGER
4 ½ 1 221pi²
4 ½ 1 171 pi²
S.D.B.
CUISINE
SAS
6'-0" MIN.
920
600
300
trappe
34" min. CCQ
CORRIDOR EN IMPASSE (ASCENSSEUR) ART.:3.3.1.9 8) a)
CORRIDOR COMMUN SANS USAGE
DALLE FINI
CHUTE A DECHETS
POSTE CANADA LOGEMENTS
D.T. CHUTE
D.T. (ETAGES)
D.T. (TOIT)
CAN.
PRIV.
COLIS P. CANADA & COLIS PRIVE
PANN. ANN. INCENDIE
POSTE CENTRAL D'ALARME ET DE COMMANDE
INTERCOM SOCLE
PORTIQUE
DRAIN
GRILLE GRATTE-PIED ENCASTREE DANS LA DALLE
TABL.
NIVEAU 1 100'-0" DESSUS DALLE
NIVEAU 1 100'-0" DESSUS DALLE 40.59m NIV. GEO.
COMMERCE
1 ENSEIGNE maximum: SUR FACADE PRINCIPALE 10 m² max.
ISSUE BATIMENT
ESCALIER #1 COMPATIMENTE
ESCALIER #2
ESCALIER #3
E.H. 22 CM
E.B. 23 CM
100mm
ENSEIGNE
ADRESSE RESIDENCE 4320
ADRESSE COM.
HALL CCQ
21.95m [72']
PENTE 2% MIN.
C-3 205|603
16'-10½"
5'-10½"
11'-0"
12'-3"
2'-10"
1'-9½"
7'-5"
10'-3"
11'-4½"
4'-1½"
3'-4"
2'-11"
4'-4"
7'-0½"
98'-9" E.B. 22 CM. ESCALIER # 3

SUITES LOCATIVES - GROUPE D OU E UNIQUEMENT - CCQ 2015
- NOTE POUR INGENIEURS & SOUS-TRAITANTS -

- PRÉVOIR 1x TOILETTE UNIVERSELLE PAR SUITE,
- PRÉVOIR 1x PANNEAU DE DISTRIBUTION ELECTRIQUE PAR SUITE,
- PRÉVOIR SÉPARATION COUPE-FEU _0.0HRE_ (TOUTEFOIS, SEPARATION CONTRE LA FUMEE ENTRE LES SUITES),
- PRÉVOIR 2x PORTES DE SORTIES PAR SUITE ; POSITIONS A ETRE COORDONEES SELON LES AMENAGEMENTS DEFINITIFS DICTES PAR LE CLIENT.

VOIR PROPRIÉTAIRE POUR POSITIONS DÉFINITIVES DES ITEMS CI-HAUTS MENTIONNÉS;
- REPRÉSENTATIONS QU'À TITRE INDICATIFS, EN POINTILLÉ,
- SUJET À CHANGEMENTS / OCCUPATIONS VERSATILES À LONG TERME.

L'ENSEMBLE CADRE ET VITRAGE DEVRA ETRE HOMOLOGUE ANTI-FEU EQUIVALENT A L'ASSEMBLAGE DE LA SEPARATION COUPE-FEU DANS LEQUEL IL SE TROUVE :
- VERRE HOMOLOGUE " COUPE-FEU " : VERRE FEUILLETE GEL INTUMESCENT TYPE ULC-S101 (SYSTEME DE VITRAGE COMPLET CERTIFIE POUR BLOQUER LA CHALEUR RADIANTE)
- VERRE RESISTANT AUX CHOCS HOMOLOGUE CAN/CGSB-12.1
- CADRE COUPE-FEU EN ALUMINIUM HOMOLOGUE CAN/ULC-S104 & S-106

POSTE CENTRAL D'ALARME ET DE COMMANDE
ART.: 3.2.6.7.1)
+ NOTE A-3.2.6.7.1) CCQ 2015;
EXIGE DANS UNE PIECE AVEC RESISTANCE AU FEU DE 1 HEURE

FENETRE ET CADRE: PREVOIR ASSEMBLAGE ULC ENTRE COMMERCE (C OU E) ET USAGE A-2 (HALL AYANT USAGE)

PORTE D'ISSUE LOGEMENTS AUCUNE POIGNEE DU COTE HALL CCQ VERROUILLEE EN TOUT TEMPS DU COTE HALL PAR ELECTRO-AIMANT, DONT LA GACHE DOIT SE DEVEROUILLER PAR CET ELECTRO-AIMANT, EN CAS D'INCENDIE

U E UNIQUEMENT - CCQ 2015
-TRAITANTS -

LLE PAR SUITE,
UTION ELECTRIQUE PAR SUITE,
U _0.0HRE_ (TOUTEFOIS, SEPARATION CONTRE LA

PAR SUITE ; POSITIONS A ETRE COORDONEES
FINITIFS DICTES PAR LE CLIENT.

ONS DÉFINITIVES DES ITEMS CI-HAUTS MENTIONNÉS;
NDICATIFS, EN POINTILLÉ,
ATIONS VERSATILES À LONG TERME.