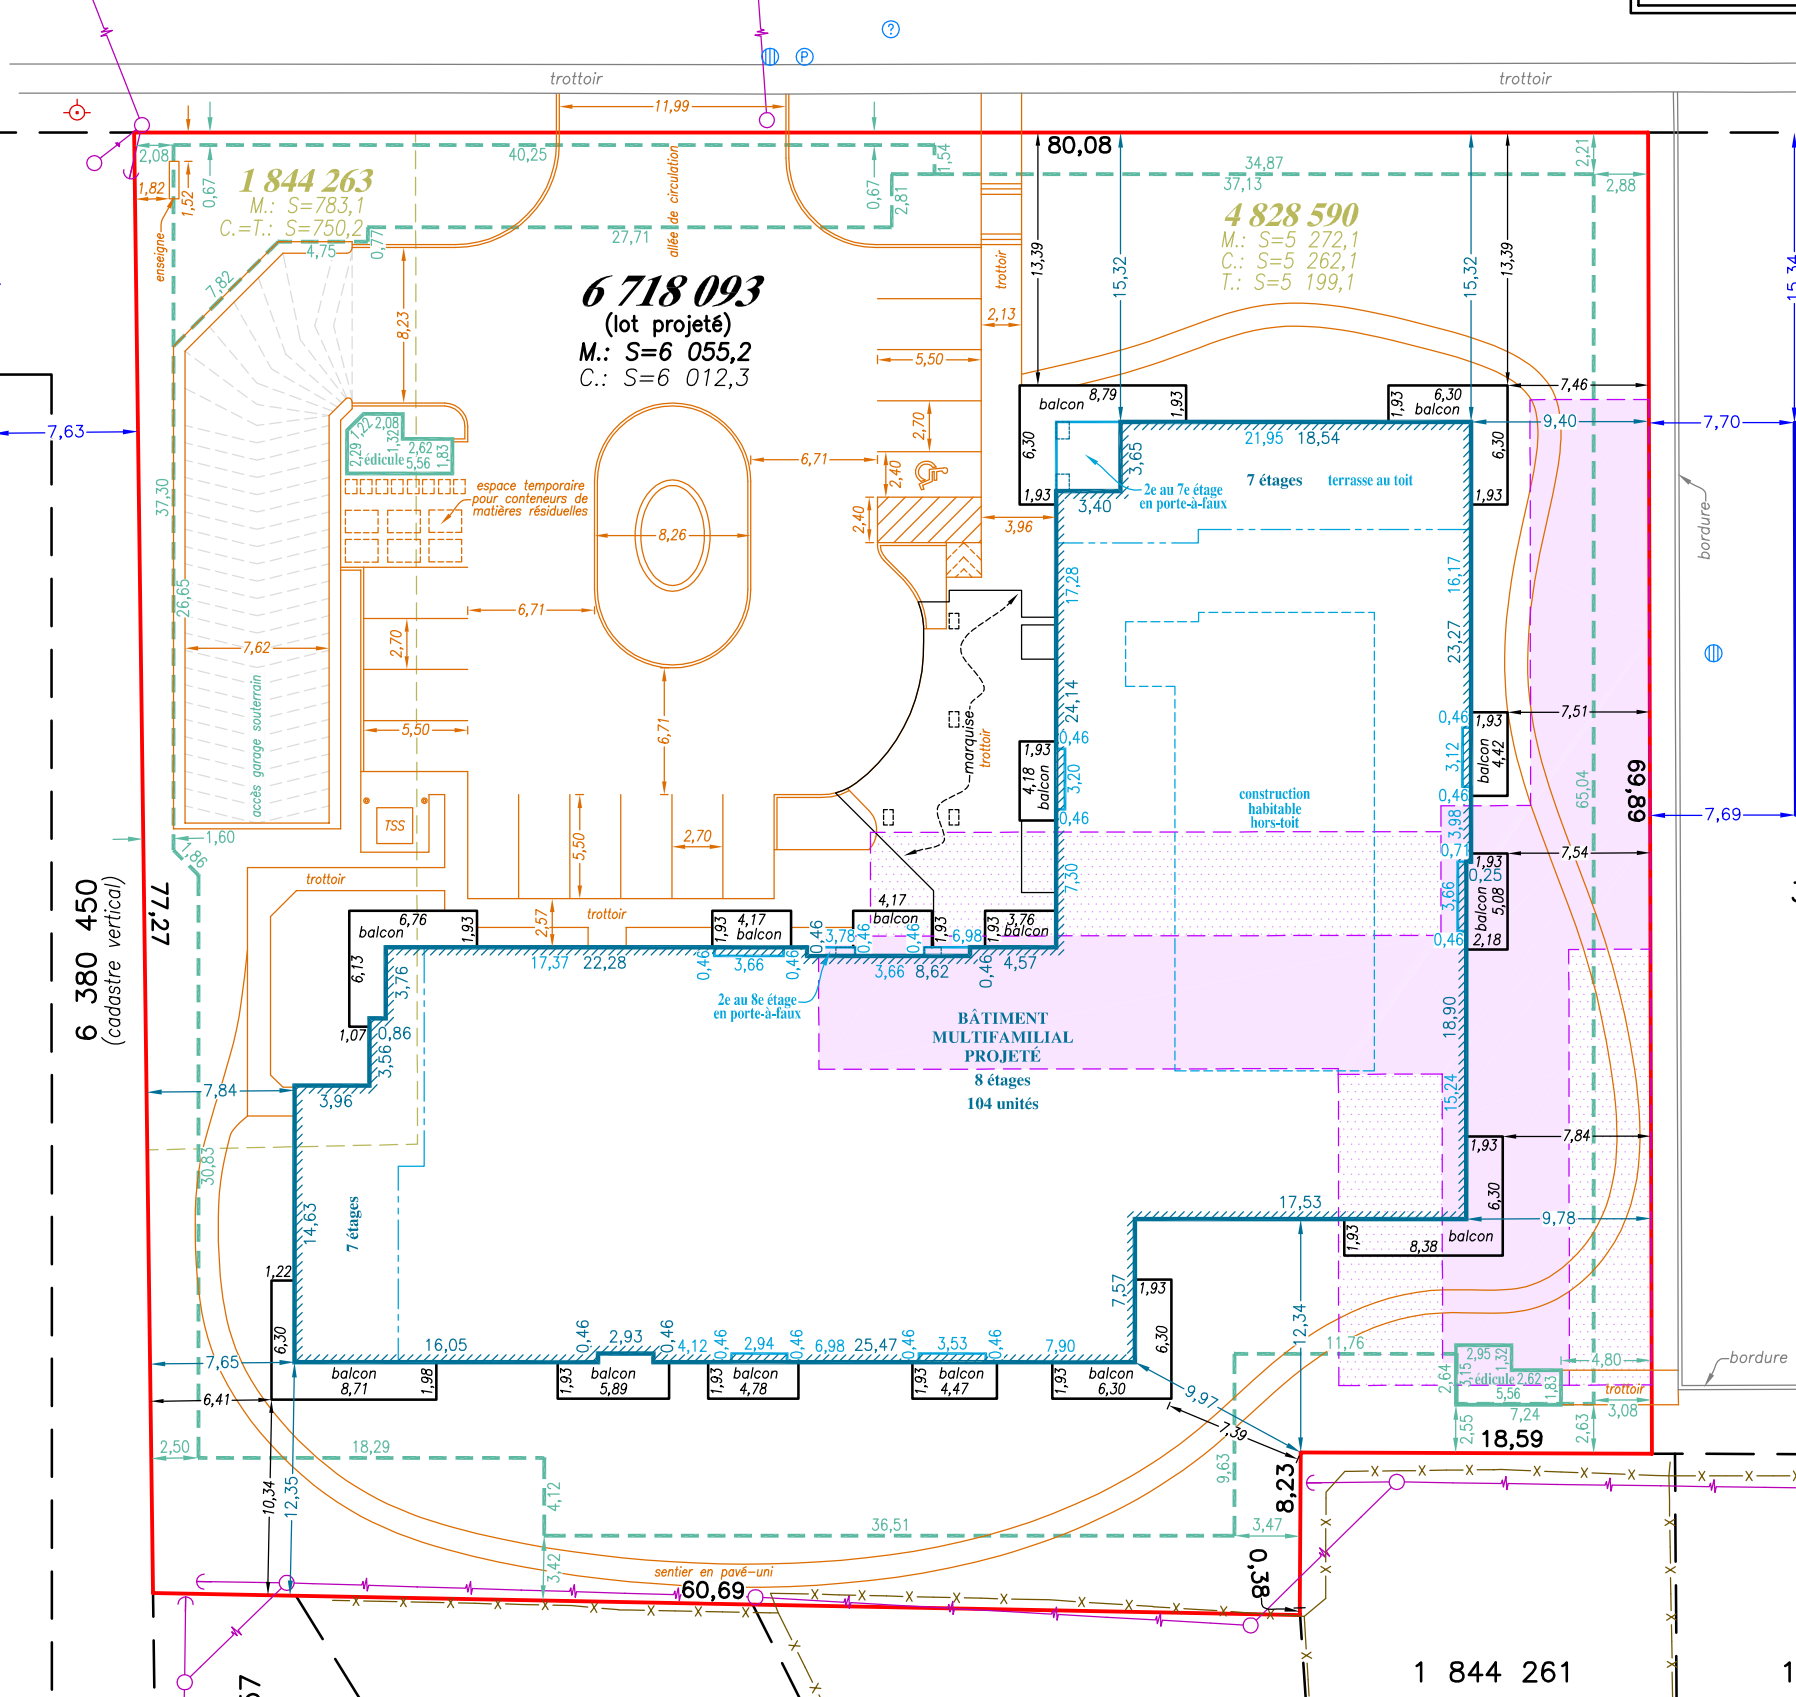

trottoir
trottoir
11,99
80,08
1 844 263
M.: S=783,1
C.=T.: S=750,2
6 718 093
(lot projeté)
M.: S=6 055,2
C.: S=6 012,3
4 828 590
M.: S=5 272,1
C.: S=5 262,1
T.: S=5 199,1
allée de circulation
enseigne
espace temporaire pour conteneurs de matières résiduelles
accès garage souterrain
TSS
marquise
trottoir
7 étages
terrasse au toit
2e au 7e étage en porte-à-faux
construction habitable hors-toit
2e au 8e étage en porte-à-faux
BÂTIMENT MULTIFAMILIAL PROJETÉ
8 étages
104 unités
7 étages
sentier en pavé-uni
bordure
bordure
trottoir
6 380 450
(cadastre vertical)
1 844 261
77,27
68,69
60,69
18,59
7,63
7,70
7,69
balcon
cédicule