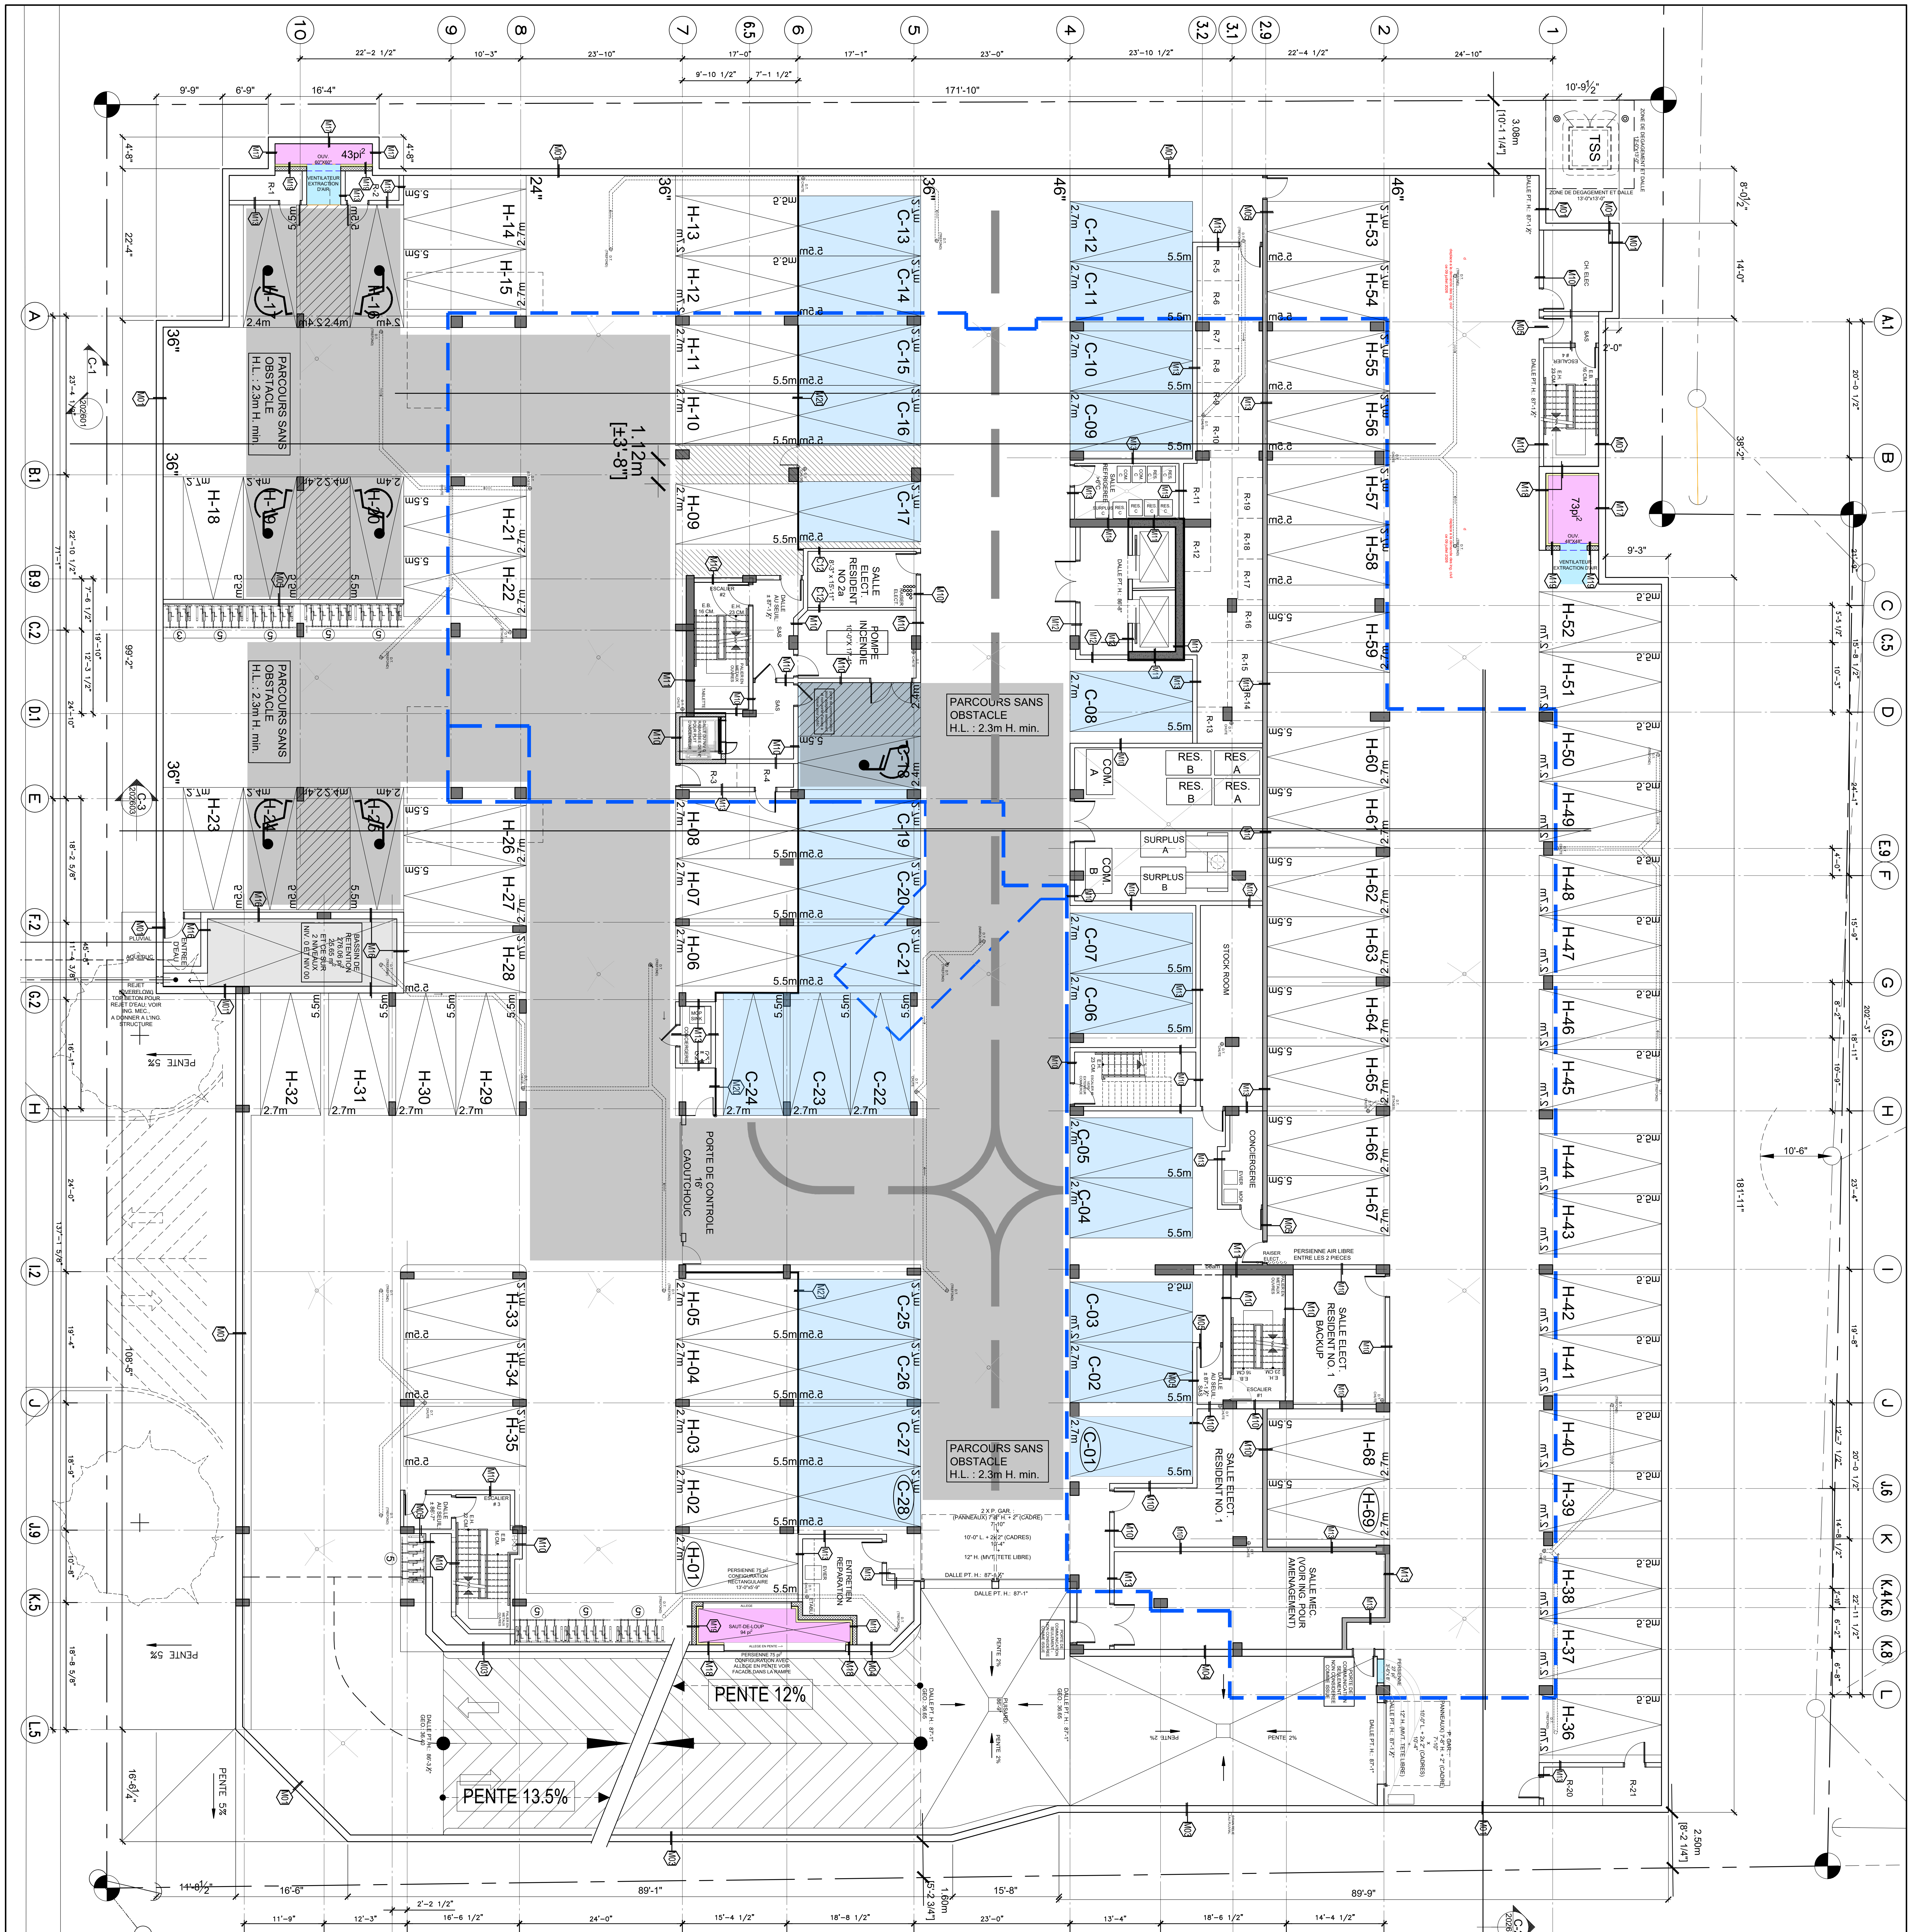
10
9
8
7
6.5
6
5
4
3.2
3.1
2.9
2
1
A
B.1
B.9
C.2
D.1
E
F.2
G.2
H
I.2
J
J.9
K.5
L.5
A.1
B
C
C.5
D
E.9
F
G
G.5
H
I
J
J.6
K
K.4
K.6
K.8
L
171'-10"
TSS
43pi²
73pi²
OUV.
VENTILATEUR EXTRACTION D'AIR
PARCOURS SANS OBSTACLE H.L. : 2.3m H. min.
1.12m [±3'-8"]
H-01
H-02
H-03
H-04
H-05
H-06
H-07
H-08
H-09
H-10
H-11
H-12
H-13
H-14
H-15
H-16
H-17
H-18
H-19
H-20
H-21
H-22
H-23
H-24
H-25
H-26
H-27
H-28
H-29
H-30
H-31
H-32
H-33
H-34
H-35
H-36
H-37
H-38
H-39
H-40
H-41
H-42
H-43
H-44
H-45
H-46
H-47
H-48
H-49
H-50
H-51
H-52
H-53
H-54
H-55
H-56
H-57
H-58
H-59
H-60
H-61
H-62
H-63
H-64
H-65
H-66
H-67
H-68
H-69
C-01
C-02
C-03
C-04
C-05
C-06
C-07
C-08
C-09
C-10
C-11
C-12
C-13
C-14
C-15
C-16
C-17
C-18
C-19
C-20
C-21
C-22
C-23
C-24
C-25
C-26
C-27
C-28
5.5m
2.7m
2.4m
SALLE ELECT. RESIDENT NO 2a
POMPE INCENDIE
ESCALIER #2
ESCALIER #1
ESCALIER #3
COM. A
COM. B
RES. A
RES. B
SURPLUS A
SURPLUS B
STOCK ROOM
CONCIERGERIE
SALLE ELECT. RESIDENT NO. 1 BACKUP
SALLE ELECT. RESIDENT NO. 1
SALLE MEC. (VOIR ING. POUR AMENAGEMENT)
ENTRETIEN REPARATION
PORTE DE CONTROLE 16' CAOUTCHOUC
BASSIN DE RETENTION
PENTE 12%
PENTE 13.5%
PENTE 5%
PENTE 2%
SAUT-DE-LOUP
PERSIENNE AIR LIBRE ENTRE LES 2 PIECES
DALLE PT. H. : 87'-1"
R-1
R-2
R-3
R-4
R-5
R-6
R-7
R-8
R-9
R-10
R-11
R-12
R-13
R-14
R-15
R-16
R-17
R-18
R-19
R-20
R-21
3.08m [10'-1 1/4"]
2.50m [8'-2 1/4"]
1.60m [5'-2 3/4"]