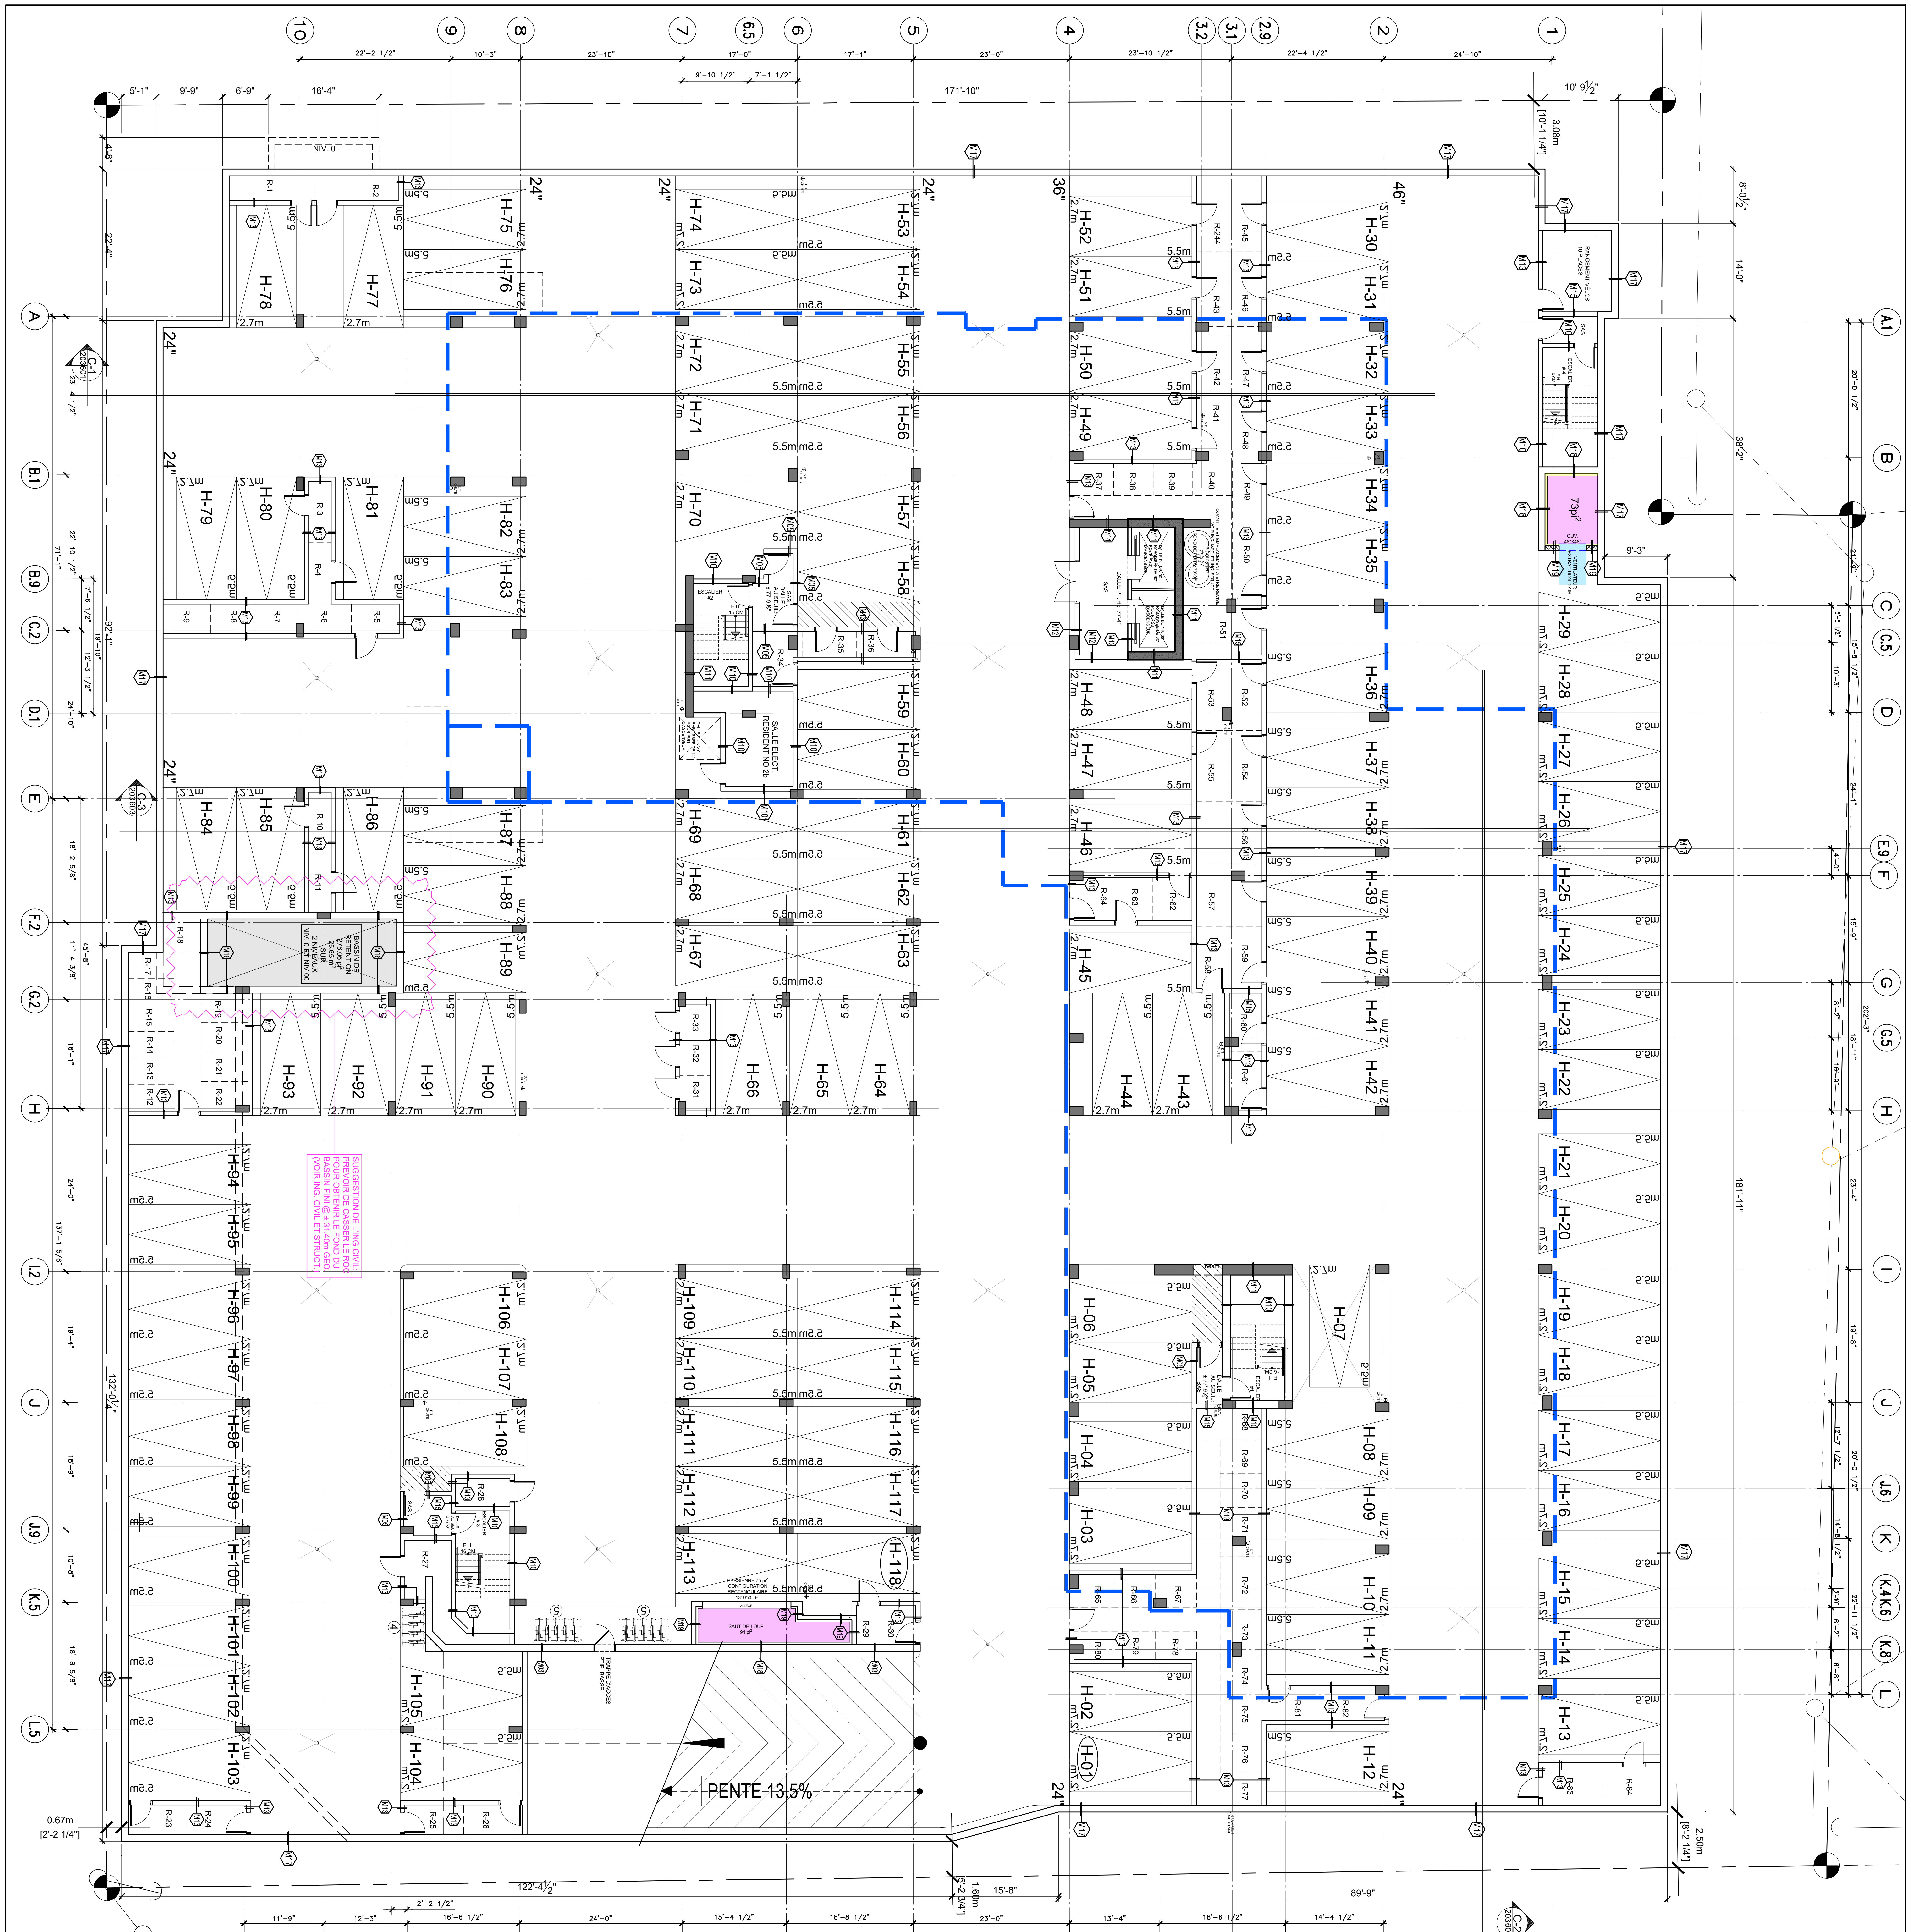
10
9
8
7
6.5
6
5
4
3.2
3.1
2.9
2
1
22'-2 1/2"
10'-3"
23'-10"
17'-0"
9'-10 1/2"
7'-1 1/2"
17'-1"
23'-0"
23'-10 1/2"
22'-4 1/2"
24'-10"
5'-1"
9'-9"
6'-9"
16'-4"
171'-10"
10'-9 1/2"
3.08m
[10'-1 1/4"]
NIV. 0
A
B.1
B.9
C.2
D.1
E
F.2
G.2
H
I.2
J
J.9
K.5
L.5
A.1
B
C
C.5
D
E.9
F
G
G.5
H
I
J
J.6
K
K.4
K.6
K.8
L
C-1
C-3
C-2
24"
36"
46"
H-01
H-02
H-03
H-04
H-05
H-06
H-07
H-08
H-09
H-10
H-11
H-12
H-13
H-14
H-15
H-16
H-17
H-18
H-19
H-20
H-21
H-22
H-23
H-24
H-25
H-26
H-27
H-28
H-29
H-30
H-31
H-32
H-33
H-34
H-35
H-36
H-37
H-38
H-39
H-40
H-41
H-42
H-43
H-44
H-45
H-46
H-47
H-48
H-49
H-50
H-51
H-52
H-53
H-54
H-55
H-56
H-57
H-58
H-59
H-60
H-61
H-62
H-63
H-64
H-65
H-66
H-67
H-68
H-69
H-70
H-71
H-72
H-73
H-74
H-75
H-76
H-77
H-78
H-79
H-80
H-81
H-82
H-83
H-84
H-85
H-86
H-87
H-88
H-89
H-90
H-91
H-92
H-93
H-94
H-95
H-96
H-97
H-98
H-99
H-100
H-101
H-102
H-103
H-104
H-105
H-106
H-107
H-108
H-109
H-110
H-111
H-112
H-113
H-114
H-115
H-116
H-117
H-118
5.5m
2.7m
R-1
R-2
R-3
R-4
R-5
R-6
R-7
R-8
R-9
R-10
R-11
R-12
R-13
R-14
R-15
R-16
R-17
R-18
R-19
R-20
R-21
R-22
R-23
R-24
R-25
R-26
R-27
R-28
R-29
R-30
M13
M16
M17
M18
M19
M03
BASSIN DE RETENTION
276.06 pi²
25.65 m²
SUR
2 NIVEAUX
NIV. 0 ET NIV 00
SUGGESTION DE L'ING CIVIL:
PREVOIR DE CASSER LE ROC
POUR OBTENIR LE FOND DU
BASSIN FINI @ ± 31.40m GEO
(VOIR ING. CIVIL ET STRUCT.)
ESCALIER
SALLE ÉLECT. RÉSIDENT. NO 2b
RANGEMENT VELOS
73pi²
PERSIENNE 75 pi²
CONFIGURATION
RECTANGULAIRE
13'-0"x5'-9"
ALLEGE
SAUT-DE-LOUP
94 pi²
TRAPPE D'ACCES
PTIE. BASSE
PENTE 13.5%
0.67m
[2'-2 1/4"]
122'-4 1/2"
1.60m
[5'-2 3/4"]
15'-8"
89'-9"
2.50m
[8'-2 1/4"]
11'-9"
12'-3"
2'-2 1/2"
16'-6 1/2"
24'-0"
15'-4 1/2"
18'-8 1/2"
23'-0"
13'-4"
18'-6 1/2"
14'-4 1/2"
181'-11"
202'-3"
132'-0"
92'-4"
71'-1"
45'-8"
137'-1 5/8"
8'-0 1/2"
14'-0"
38'-2"
9'-3"