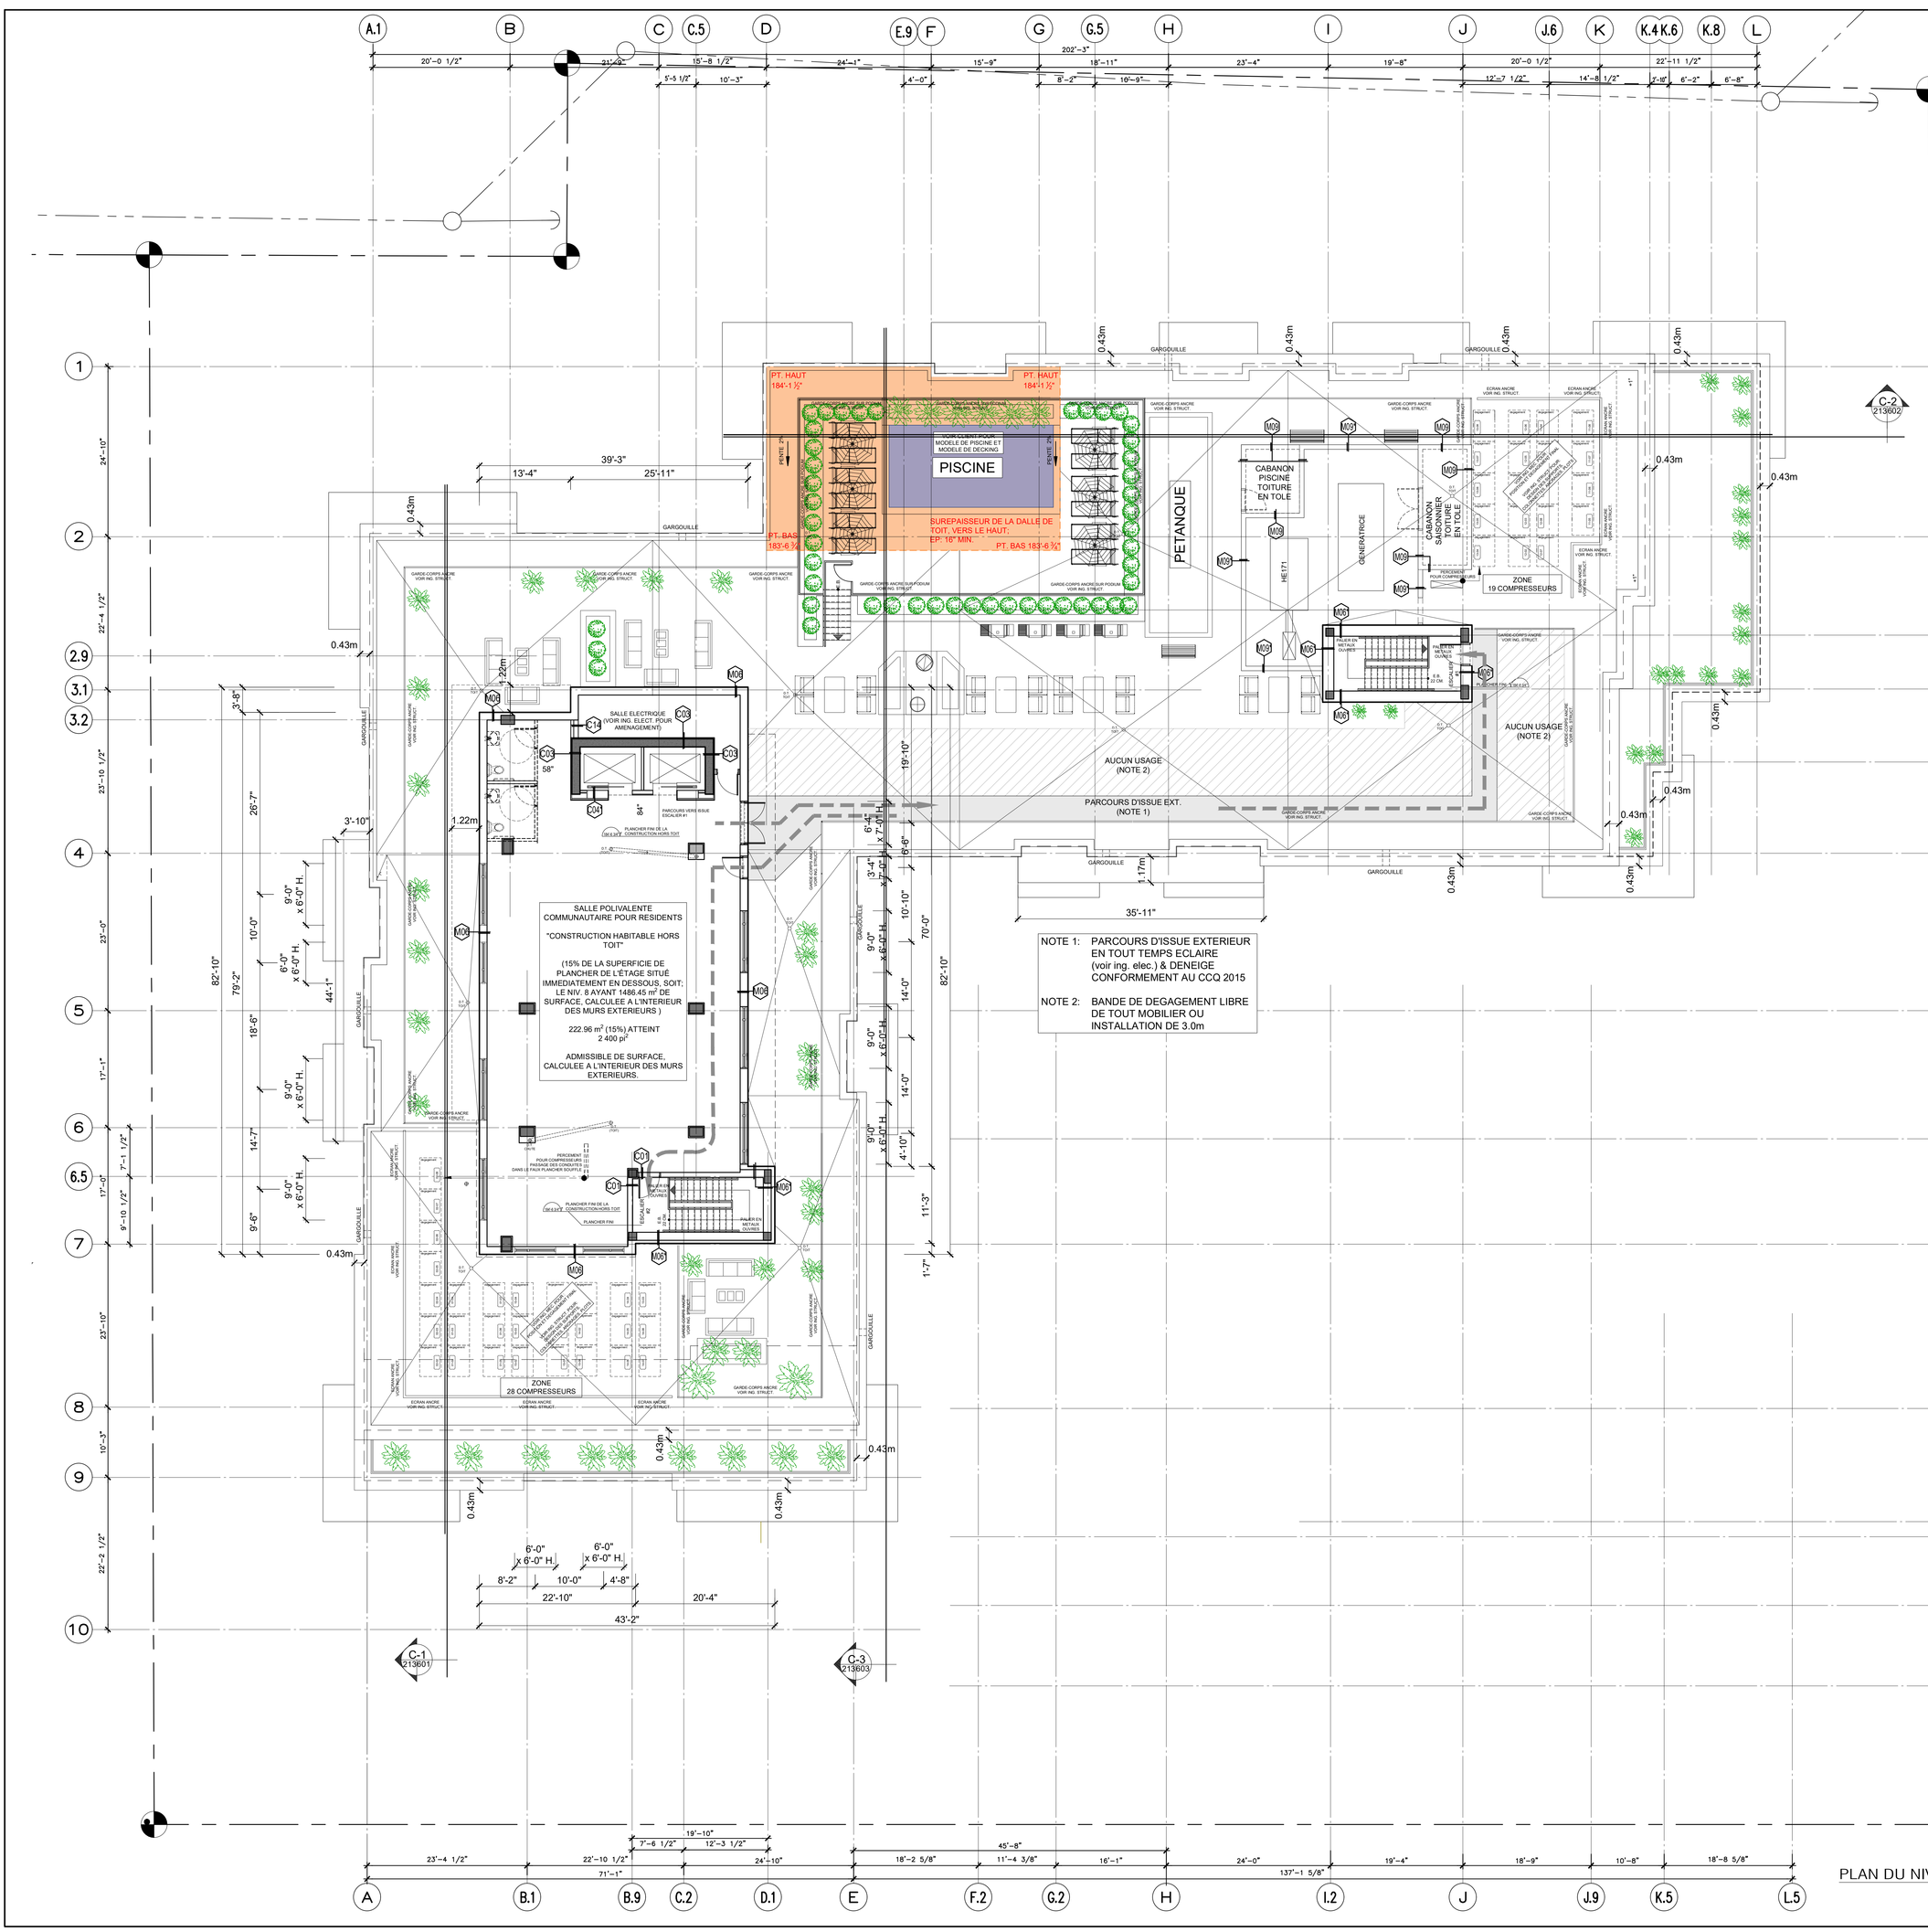

PT. HAUT 184'-1 ½"
PT. HAUT 184'-1 ½"
PISCINE
SURÉPAISSEUR DE LA DALLE DE TOIT, VERS LE HAUT. EP: 16" MIN.
PT. BAS 183'-6 ¾"
PT. BAS 183'-6 ¾"
PETANQUE
CABANON PISCINE TOITURE EN TOLE
GÉNÉRATRICE
CABANON SAISONNIER TOITURE EN TOLE
ZONE 19 COMPRESSEURS
AUCUN USAGE (NOTE 2)
PARCOURS D'ISSUE EXT. (NOTE 1)
SALLE ELECTRIQUE (VOIR ING. ELECT. POUR AMENAGEMENT)
SALLE POLIVALENTE COMMUNAUTAIRE POUR RESIDENTS
"CONSTRUCTION HABITABLE HORS TOIT"
(15% DE LA SUPERFICIE DE PLANCHER DE L'ÉTAGE SITUÉ IMMEDIATEMENT EN DESSOUS, SOIT; LE NIV. 8 AYANT 1486.45 m² DE SURFACE, CALCULÉE A L'INTERIEUR DES MURS EXTERIEURS )
222.96 m² (15%) ATTEINT 2 400 pi²
ADMISSIBLE DE SURFACE, CALCULEE A L'INTERIEUR DES MURS EXTERIEURS.
ZONE 28 COMPRESSEURS
NOTE 1: PARCOURS D'ISSUE EXTERIEUR EN TOUT TEMPS ECLAIRE (voir ing. elec.) & DENEIGE CONFORMEMENT AU CCQ 2015
NOTE 2: BANDE DE DEGAGEMENT LIBRE DE TOUT MOBILIER OU INSTALLATION DE 3.0m
GARGOUILLE
GARDE-CORPS ANCRE VOIR ING. STRUCT.
ECRAN ANCRE VOIR ING. STRUCT.
C-1 213601
C-2 213602
C-3 213603
PLAN DU NIVEA