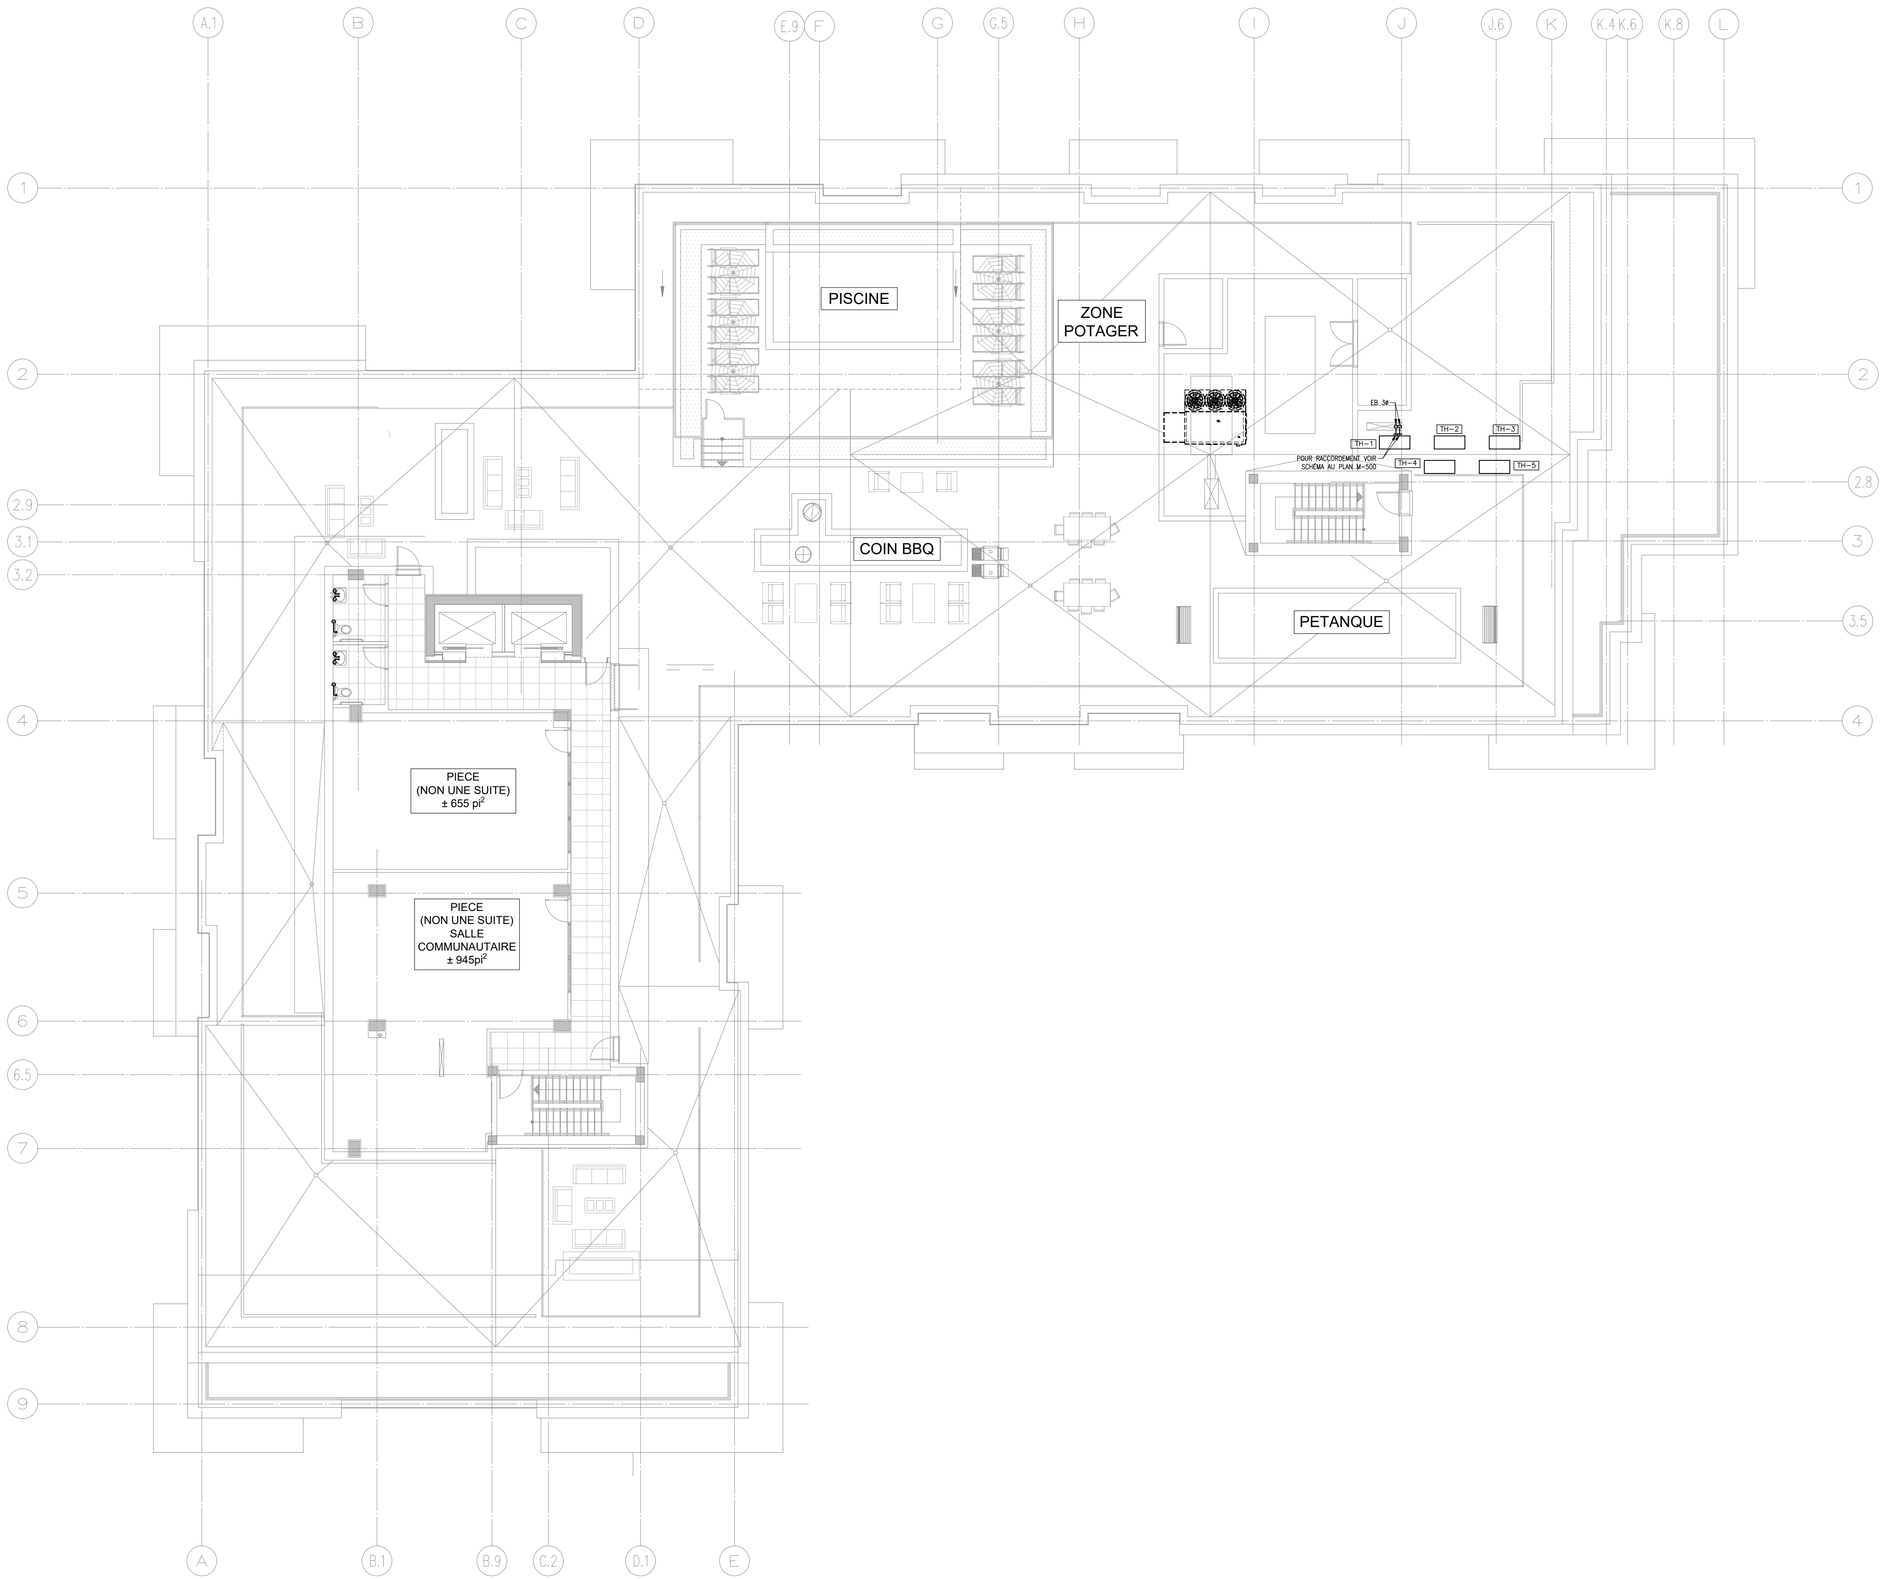

PISCINE
ZONE
POTAGER
COIN BBQ
PETANQUE
EB 34
TH-1
TH-2
TH-3
TH-4
TH-5
POUR RACCORDEMENT VOIR
SCHÉMA AU PLAN M-500
PIECE
(NON UNE SUITE)
± 655 pi²
PIECE
(NON UNE SUITE)
SALLE
COMMUNAUTAIRE
± 945pi²
A.1
B
C
D
E.9
F
G
G.5
H
I
J
J.6
K
K.4
K.6
K.8
L
1
2
2.8
2.9
3.1
3.2
3
3.5
4
5
6
6.5
7
8
9
A
B.1
B.9
C.2
D.1
E