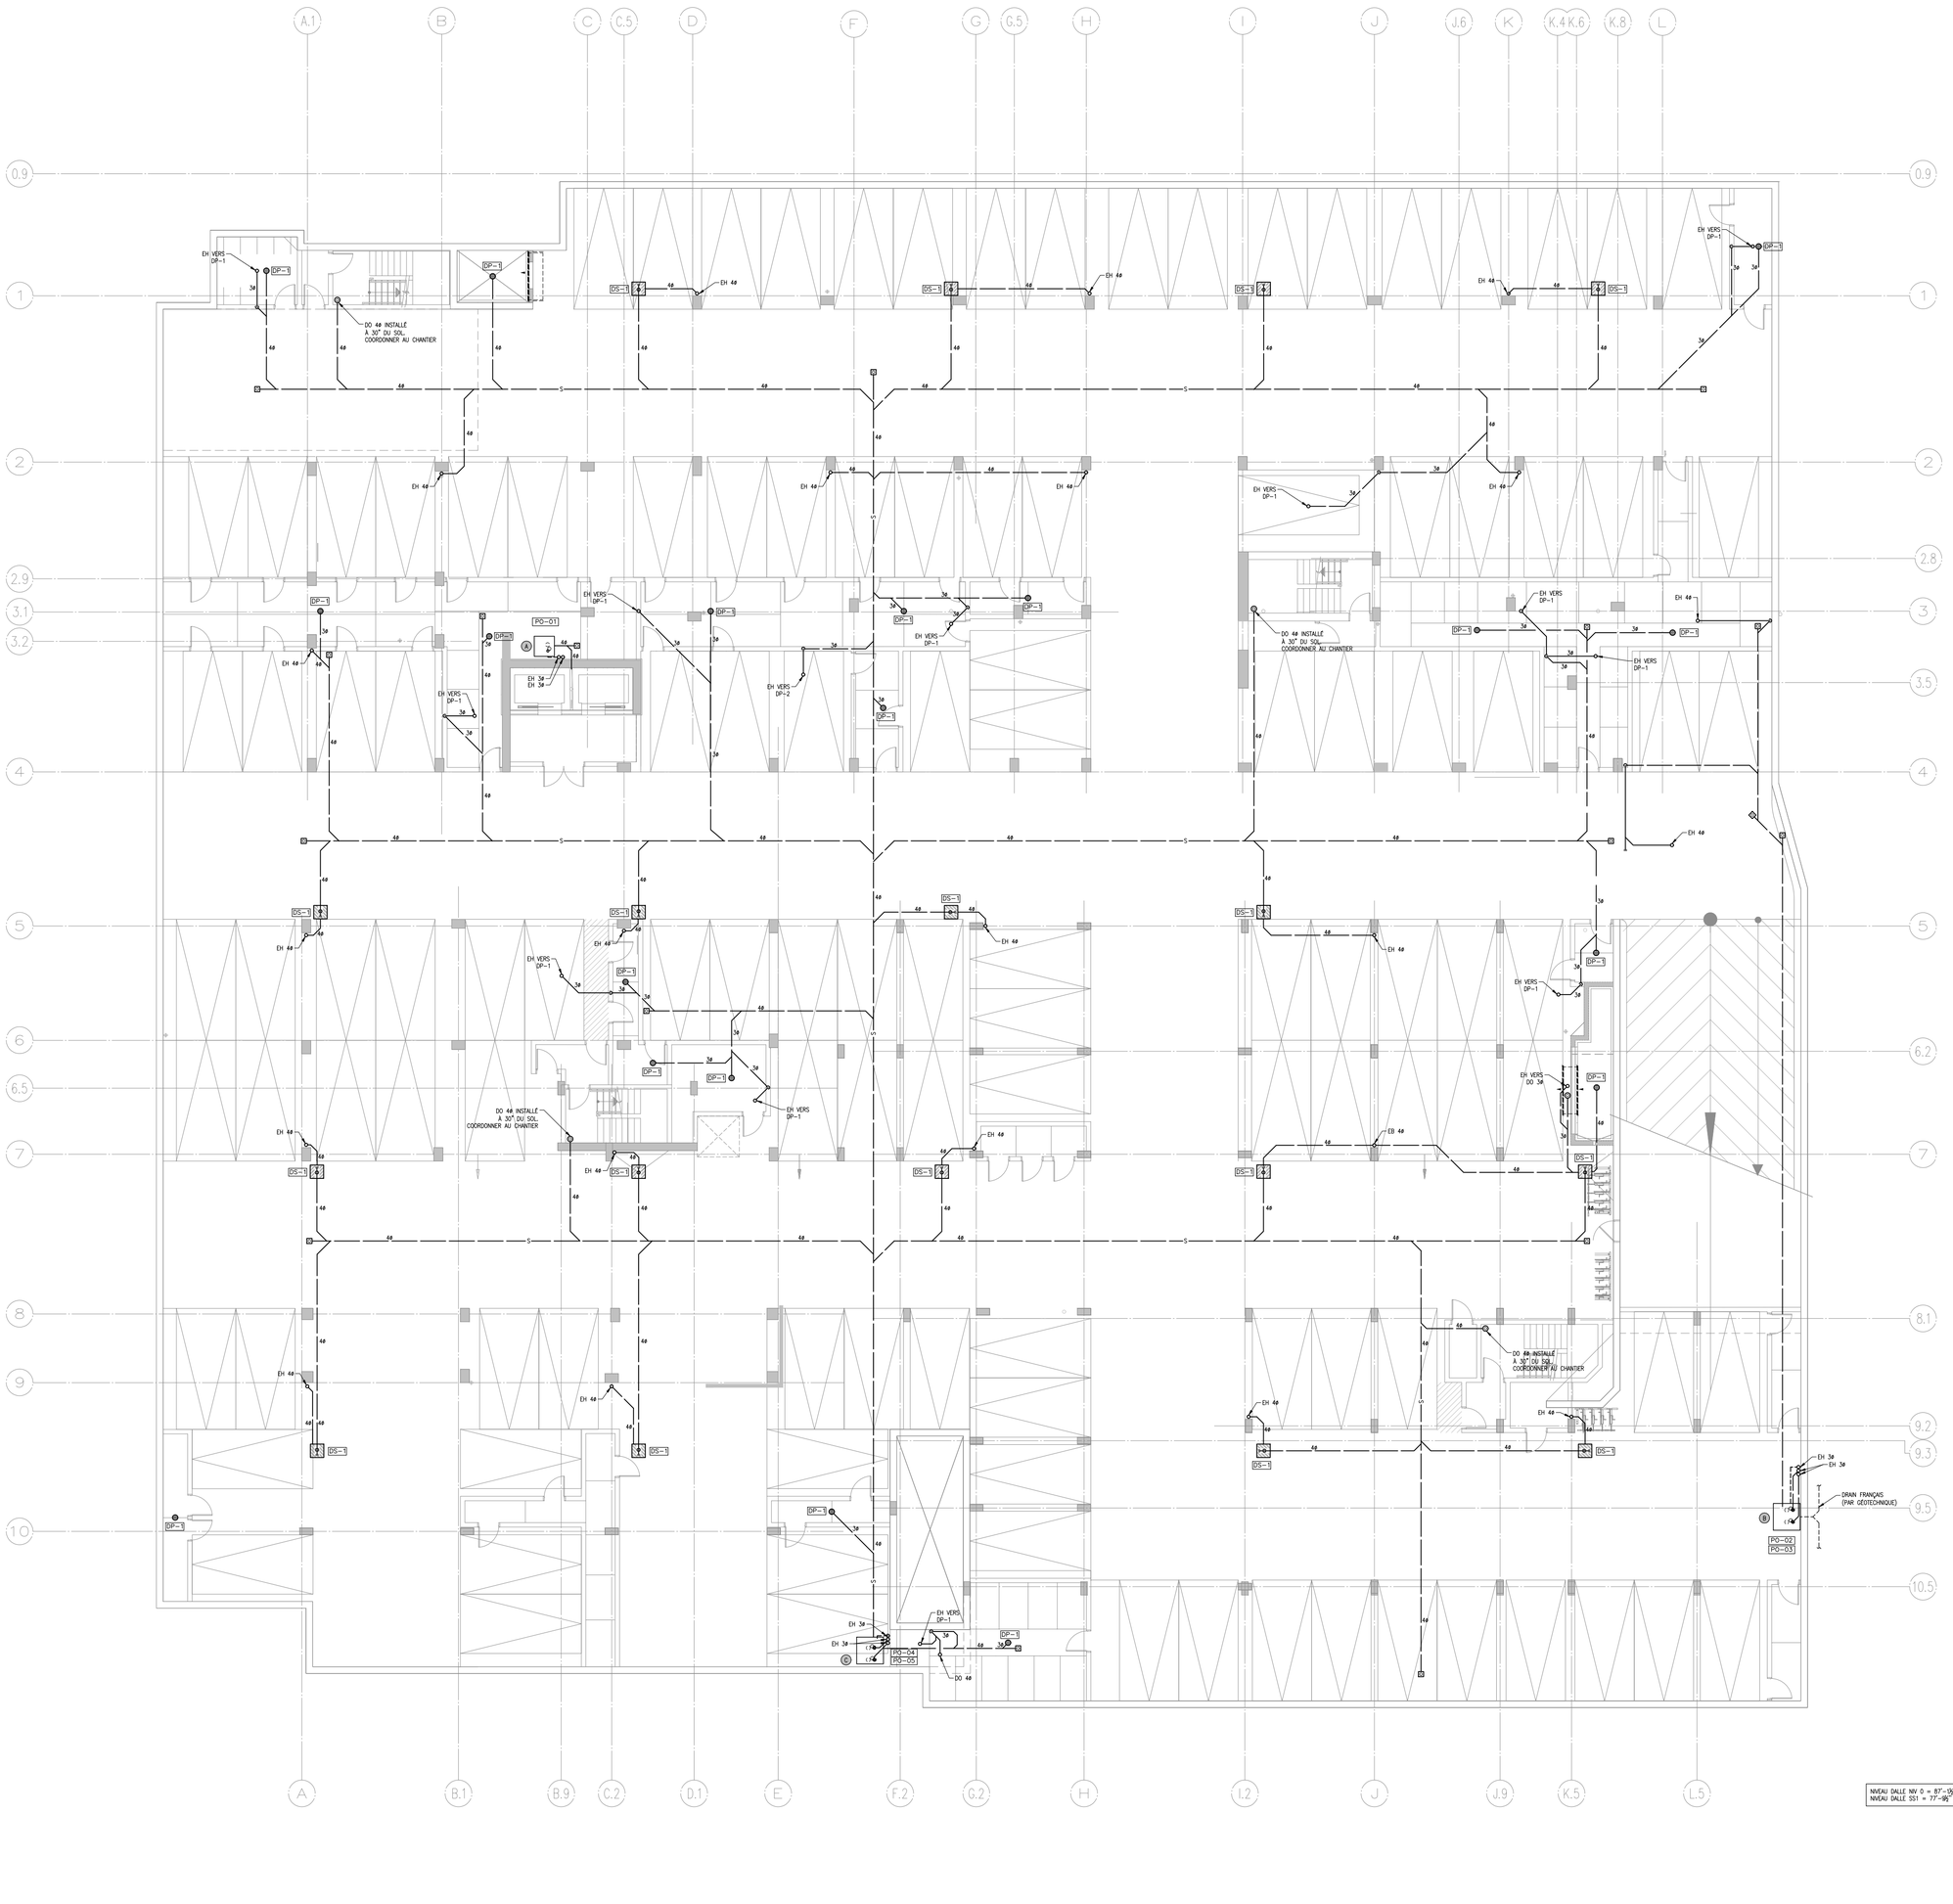


HAUTEUR LIBRE STATIONNEMENT

CONSERVER 7'-7" (2300mm) MIN. LIBRE ENTRE LE PLANCHER FINI ET TOUT ÉQUIPEMENT MÉCANIQUE AU PLAFOND DES ALLÉES DE CIRCULATION ET DES STATIONNEMENTS POUR HANDICAPÉS. VOIR ZONE HACHURÉE AU PLAN, À COORDONNER AVEC L'ARCHITECTE. CONSERVER 6'-7" (2000mm) MIN. LIBRE ENTRE LE PLANCHER FINI ET TOUT ÉQUIPEMENT MÉCANIQUE AU PLAFOND DE TOUT AUTRE STATIONNEMENT.

PUISARDS POMPÉS

Ⓐ PUISARD D'ASCENSEUR
36"x36"x24" PLUS PROFOND QUE LE PUITS D'ASCENSEUR AVEC COUVERCLE TYPE "B" (VOIR DÉTAIL)
PAR ENTREPRENEUR GÉNÉRAL
POMPES PAR ENTREPRENEUR EN PLOMBERIE
PUISARD PAR STRUCTURE
PO-1

Ⓑ PUISARD PLUVIAL
48"x48"x60" AVEC COUVERCLE TYPE "B" (VOIR DÉTAIL)
PAR ENTREPRENEUR GÉNÉRAL
POMPES PAR ENTREPRENEUR EN PLOMBERIE
PUISARD PAR EXCAVATION
PO-2 PO-3

Ⓒ PUISARD SANITAIRE 48"x48"x72" AVEC COUVERCLE TYPE "B" (VOIR DÉTAIL) PAR ENTREPRENEUR GÉNÉRAL
POMPES PAR ENTREPRENEUR EN PLOMBERIE
PUISARD PAR EXCAVATION
PO-4 PO-5

NIVEAU DALLE NIV 0 = 87'-0⅝" ARCH. = 36.66 GÉO.
NIVEAU DALLE SS1 = 77'-9⅝" ARCH. = 33.81 GÉO.