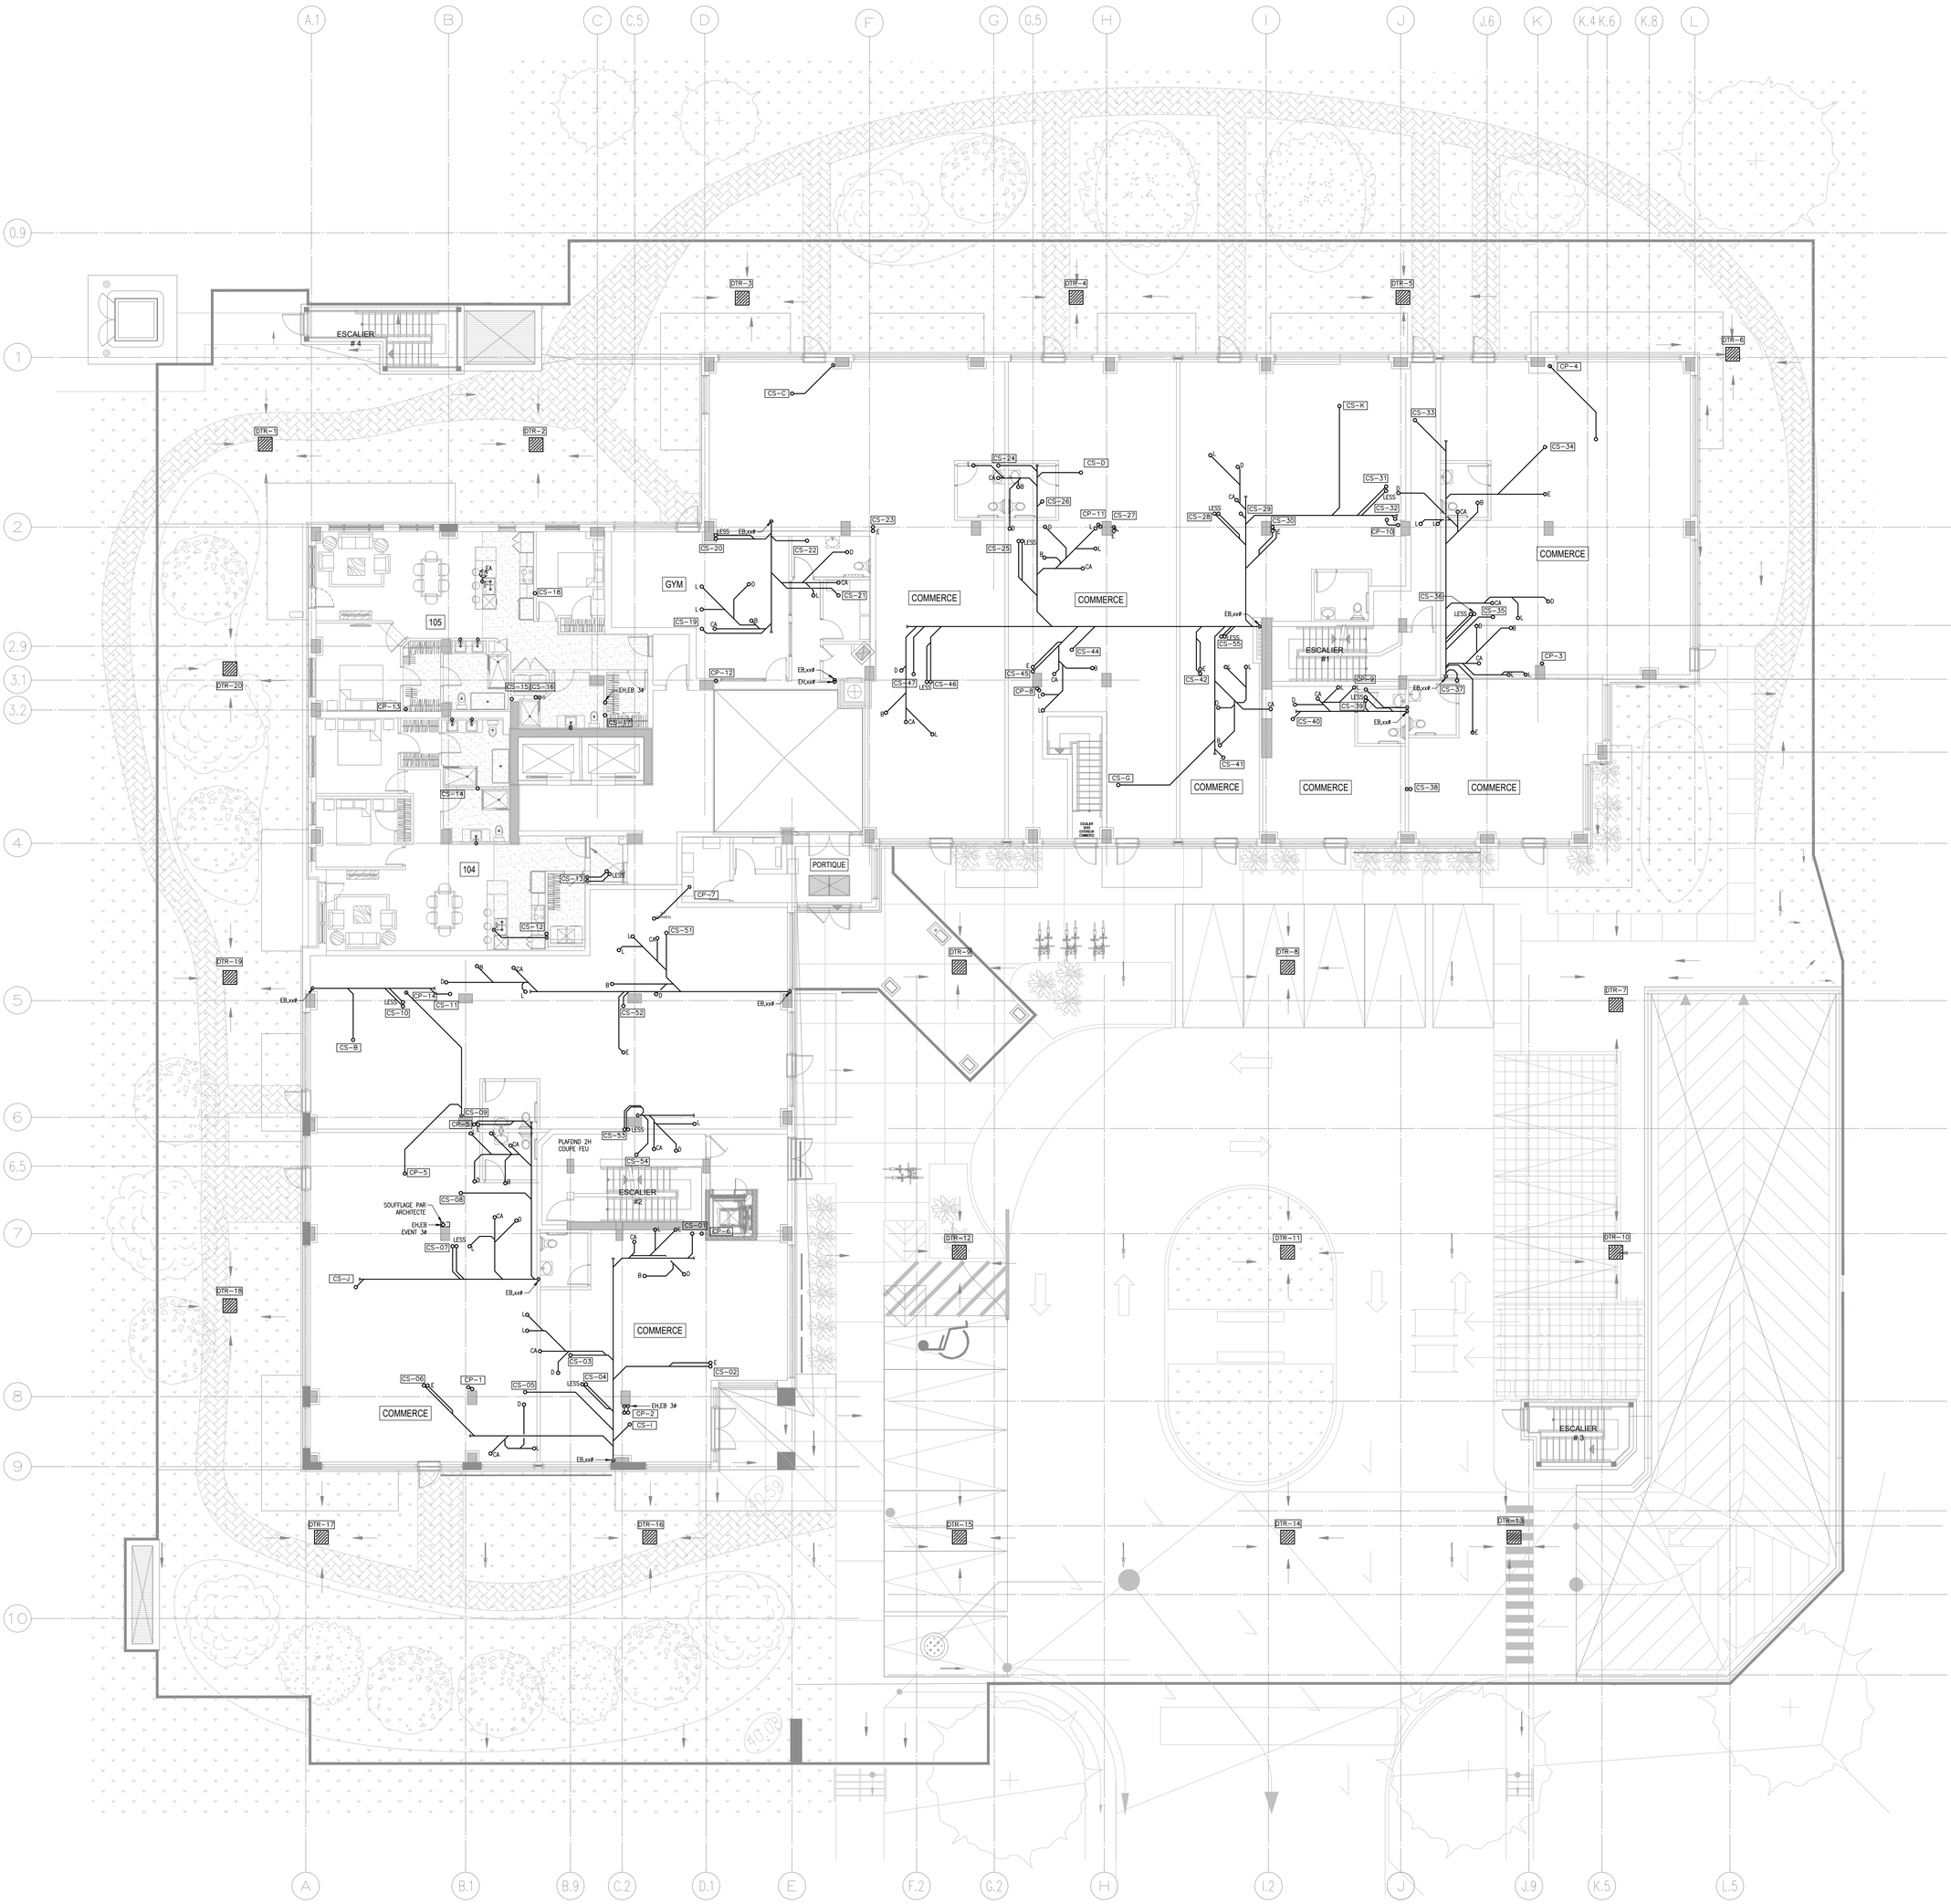

A.1
B
C
C.5
D
F
G
G.5
H
I
J
J.6
K
K.4
K.6
K.8
L
0.9
1
2
2.9
3.1
3.2
4
5
6
6.5
7
8
9
10
A
B.1
B.9
C.2
D.1
E
F.2
G.2
H
I.2
J
J.9
K.5
L.5
ESCALIER #4
ESCALIER #2
ESCALIER #1
ESCALIER #3
GYM
105
104
PORTIQUE
COMMERCE
PLAFOND 2H COUPE FEU
SOUFFLAGE PAR ARCHITECTE
DTR-1
DTR-2
DTR-3
DTR-4
DTR-5
DTR-6
DTR-7
DTR-8
DTR-9
DTR-10
DTR-11
DTR-12
DTR-13
DTR-14
DTR-15
DTR-16
DTR-17
DTR-18
DTR-19
DTR-20
CS-A
CS-B
CS-C
CS-D
CS-E
CS-F
CS-G
CS-H
CS-I
CS-J
CS-K
CP-1
CP-2
CP-3
CP-4
CP-5
CP-6
CP-7
CP-8
CP-9
CP-10
CP-11
CP-12
EB,xx#
EN,EB 3#
LESS
CA