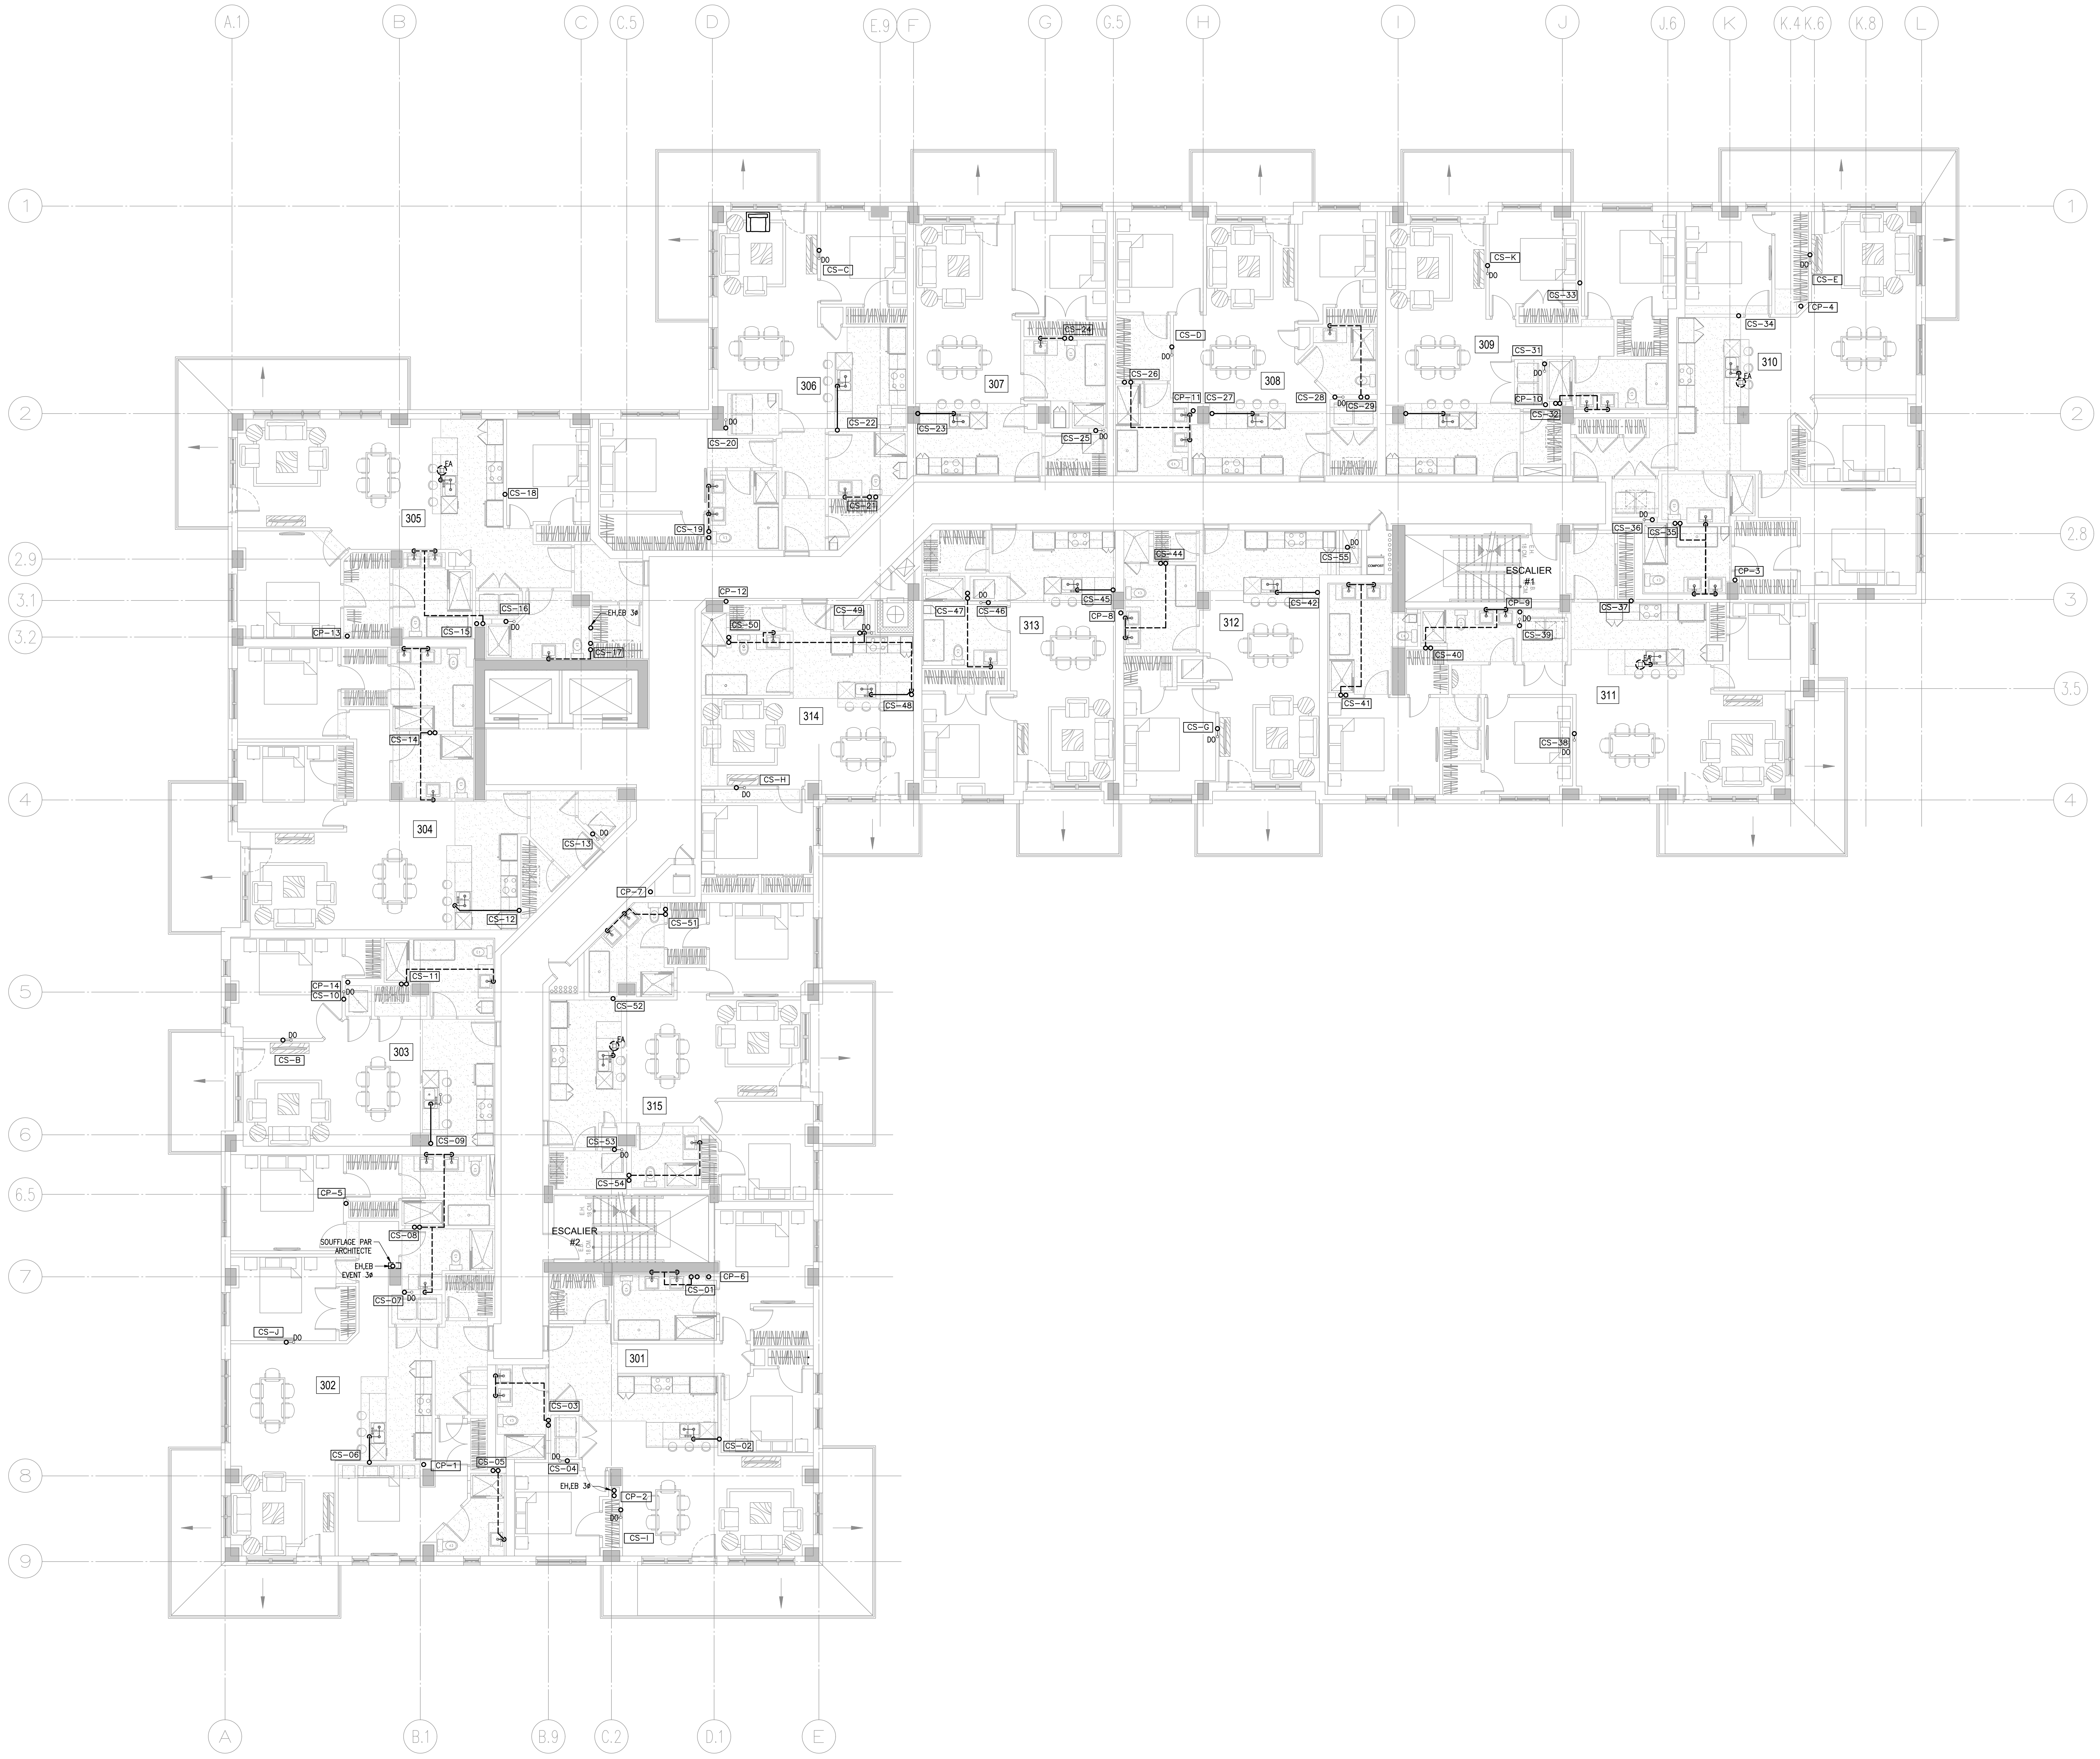
A.1
B
C
C.5
D
E.9
F
G
G.5
H
I
J
J.6
K
K.4
K.6
K.8
L
1
2
2.8
2.9
3
3.1
3.2
3.5
4
5
6
6.5
7
8
9
A
B.1
B.9
C.2
D.1
E
301
302
303
304
305
306
307
308
309
310
311
312
313
314
315
ESCALIER #1
ESCALIER #2
SOUFFLAGE PAR ARCHITECTE
EH,EB EVENT 3#
EH,EB 3#
CS-01
CS-02
CS-03
CS-04
CS-05
CS-06
CS-07
CS-08
CS-09
CS-10
CS-11
CS-12
CS-13
CS-14
CS-15
CS-16
CS-17
CS-18
CS-19
CS-20
CS-21
CS-22
CS-23
CS-24
CS-25
CS-26
CS-27
CS-28
CS-29
CS-30
CS-31
CS-32
CS-33
CS-34
CS-35
CS-36
CS-37
CS-38
CS-39
CS-40
CS-41
CS-42
CS-43
CS-44
CS-45
CS-46
CS-47
CS-48
CS-49
CS-50
CS-51
CS-52
CS-53
CS-54
CS-55
CS-B
CS-C
CS-D
CS-E
CS-G
CS-H
CS-I
CS-J
CS-K
CP-1
CP-2
CP-3
CP-4
CP-5
CP-6
CP-7
CP-8
CP-9
CP-10
CP-11
CP-12
CP-13
CP-14