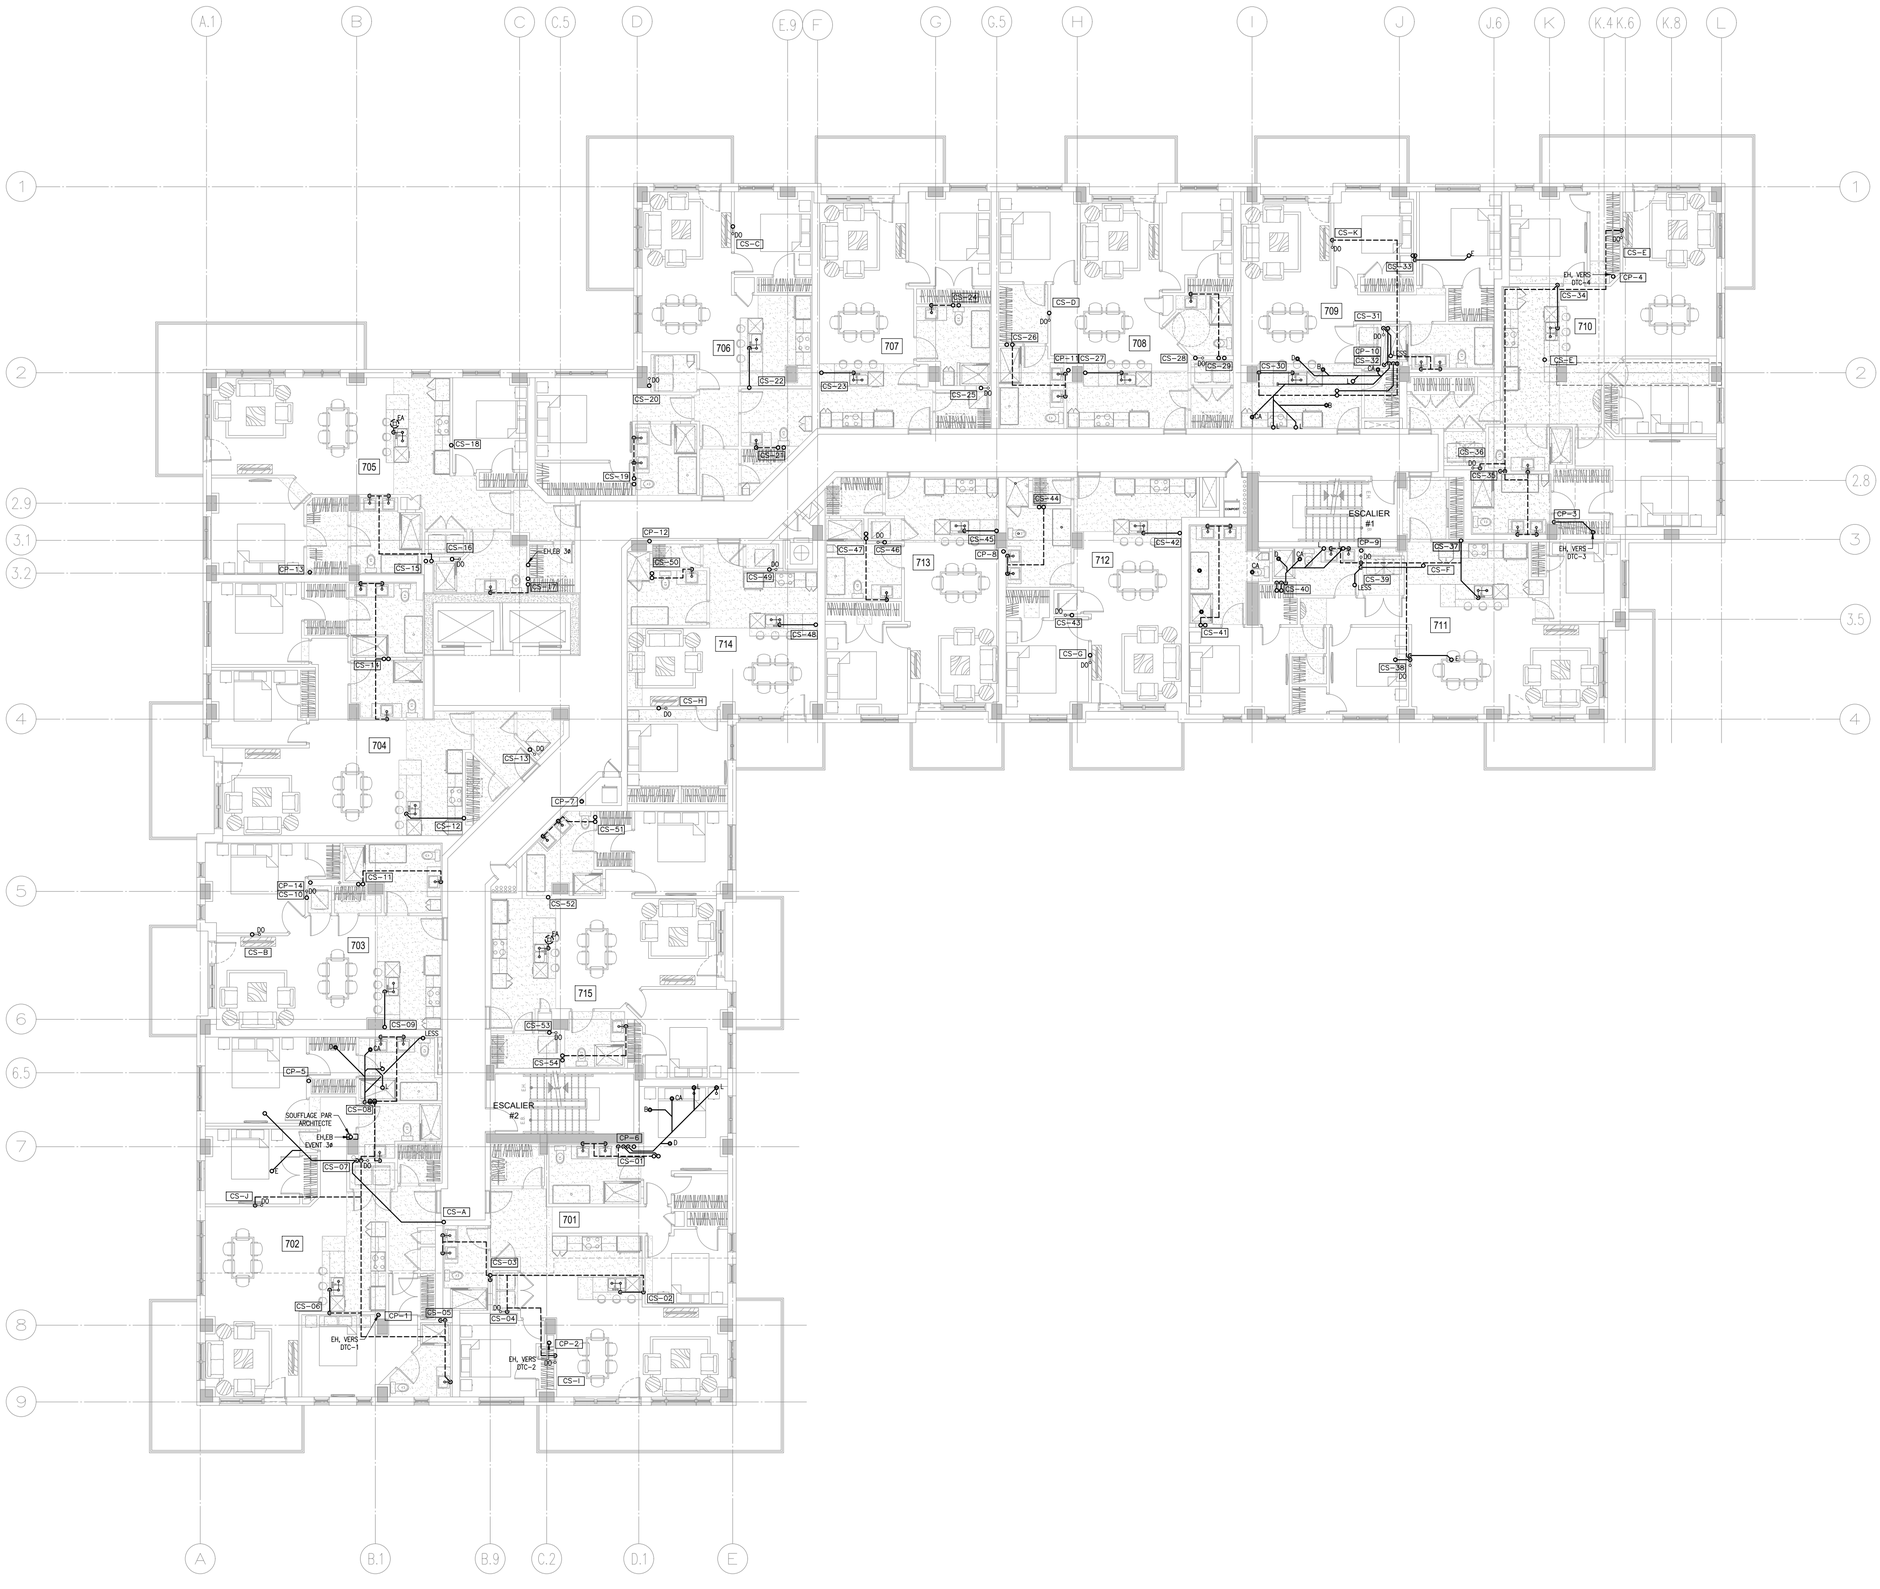

A.1
B
C
C.5
D
E.9
F
G
G.5
H
I
J
J.6
K
K.4
K.6
K.8
L
A
B.1
B.9
C.2
D.1
E
1
2
2.8
2.9
3
3.1
3.2
3.5
4
5
6
6.5
7
8
9
701
702
703
704
705
706
707
708
709
710
711
712
713
714
715
ESCALIER #1
ESCALIER #2
SOUFFLAGE PAR ARCHITECTE
EH, VERS DTC-1
EH, VERS DTC-2
EH, VERS DTC-3
EH, VERS DTC-4
EH,EB 3d
EVENT 3d
CS-A
CS-B
CS-C
CS-D
CS-E
CS-F
CS-G
CS-H
CS-I
CS-J
CS-K
CP-1
CP-2
CP-3
CP-4
CP-5
CP-6
CP-7
CP-9
CP-10
CP-11
CP-12
CP-13
CP-14