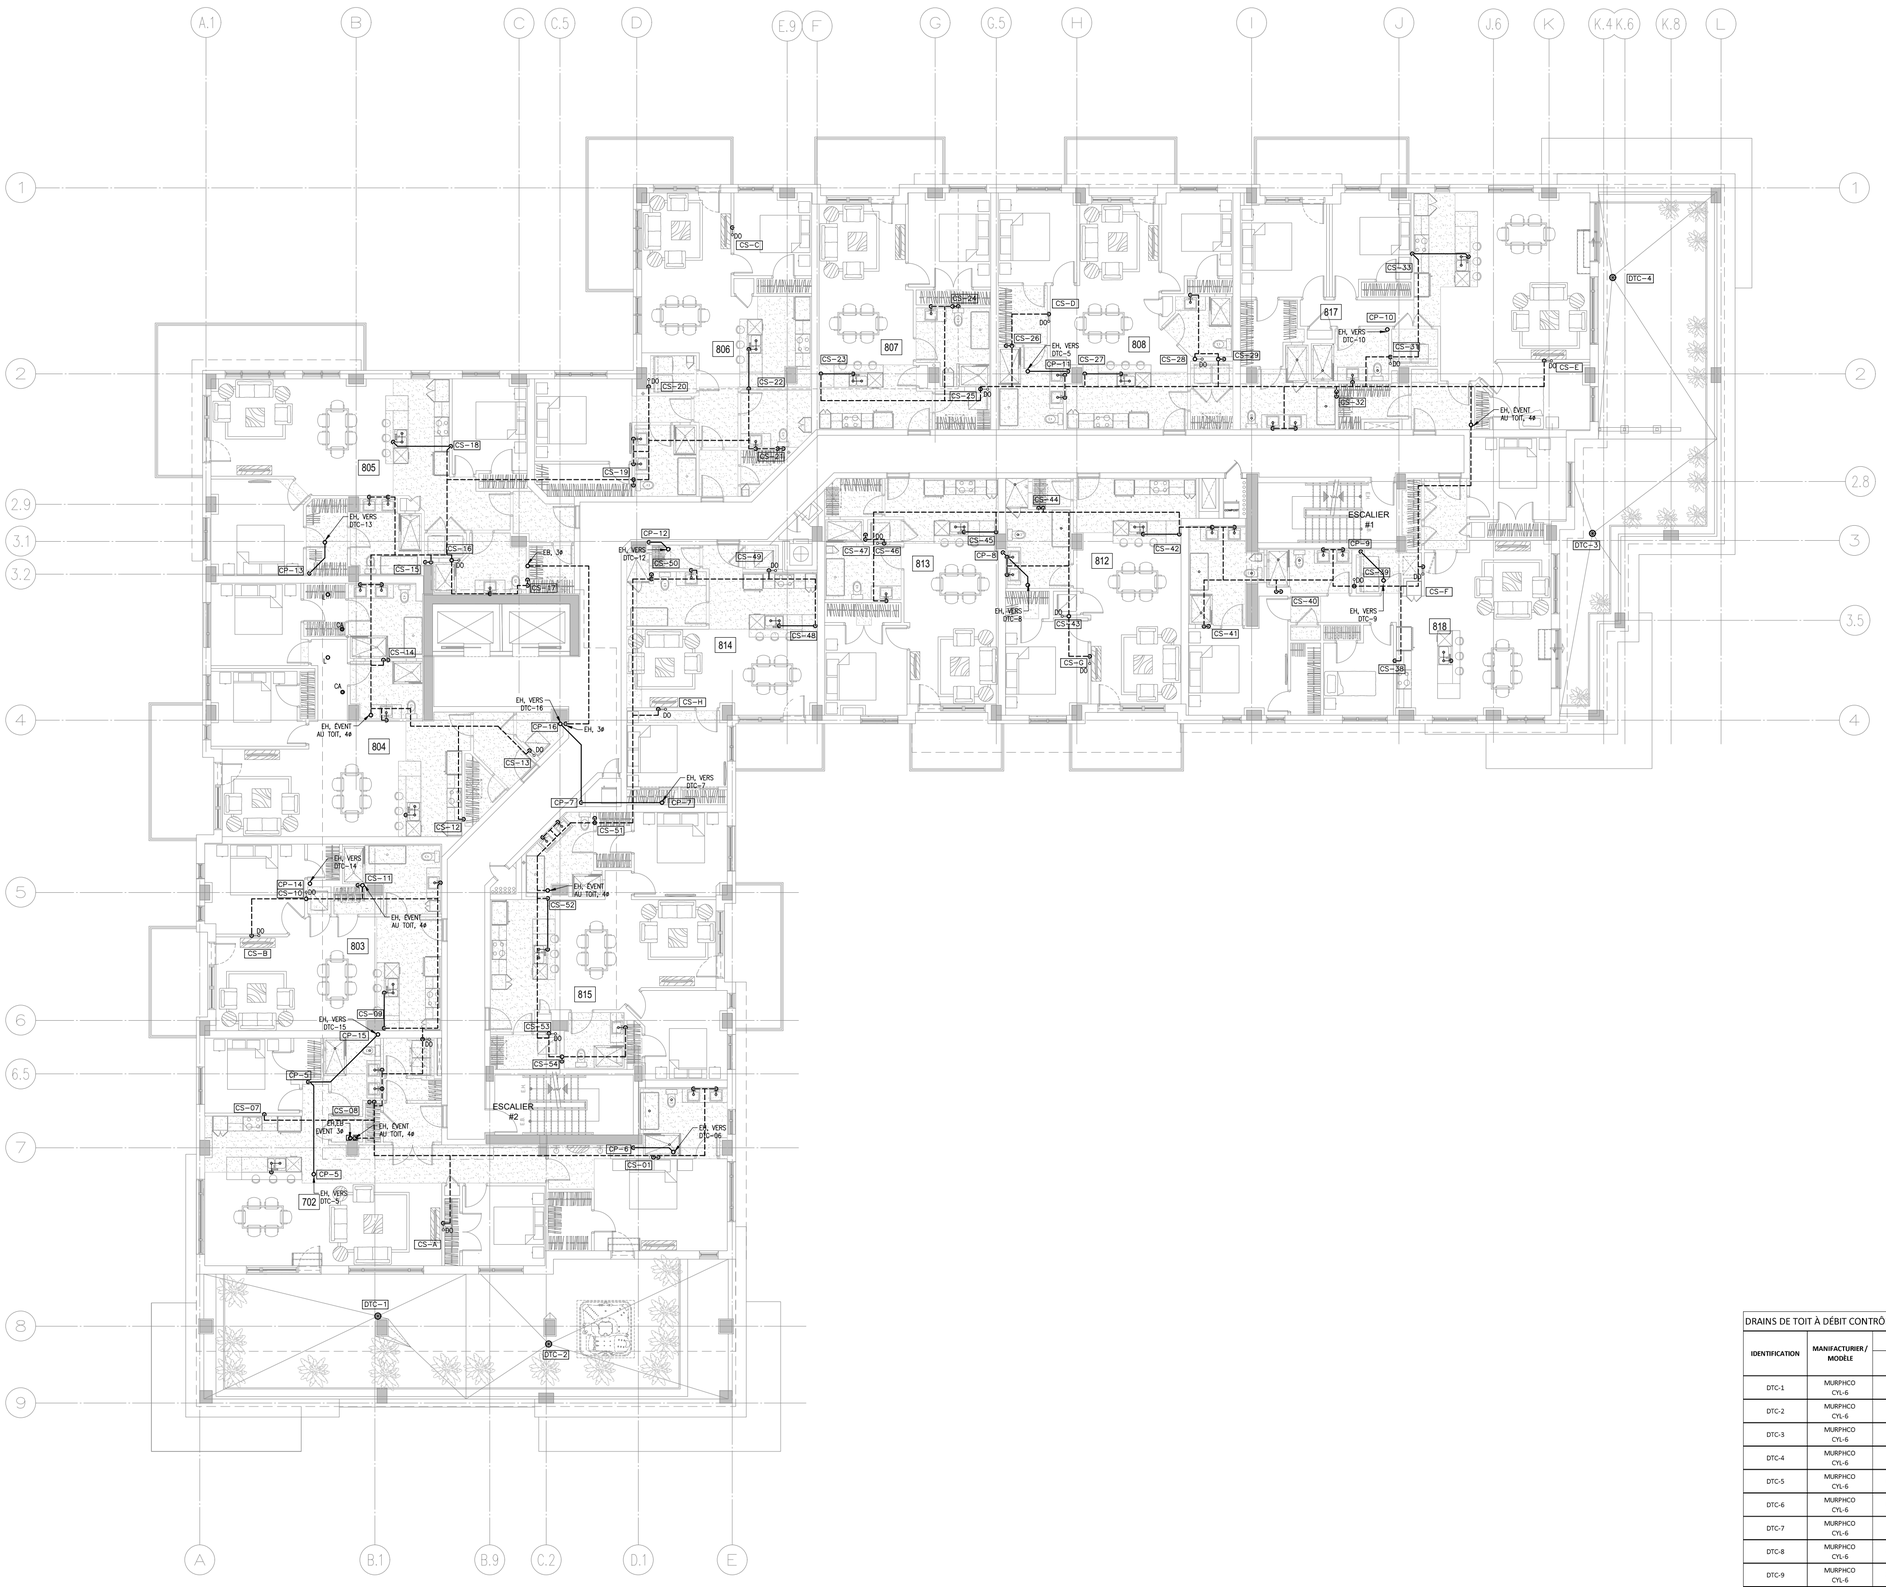


DALOTS

IDENTIFICATION		SUPERFICIE			
pi²	m²	po	mm	poØ	mmØ
0 à 1970	0 à 183	12x4	300x100	8	200
1970 à 5800	183 à 539	12x10	300x250	12	300
58000 à 9688	539 à 900	16x12	400x300	16	400

NOTES:

1.AU MOINS UN DALOT POUR CHACUN DES BASSINS DE TOIT DEVRA ÊTRE INSTALLÉ ESPACÉS LES UNS DES AUTRES D'AU-PLUS 98'-5" (30m) AU PÉRIMETRE DU BÂTIMENT. LE RADIER DU DALOT DEVRA ÊTRE À 6'' (150mm) AU-DESSUS DU DRAIN DE TOIT. L'EMPLACEMENT EXACT DEVRA ÊTRE DÉTERMINÉ PAR L'ARCHITECTE.

DRAINS DE TOIT À DÉBIT CONTRÔLÉ

IDENTIFICATION	MANIFACTURIER / MODÈLE	SUPERFICIE		OUVERTURE	DÉBIT		ACC. EAU	VOLUME DE RÉTENTION		TEMPS ÉCOULEMENT	NOTES
		pi²	m²	mm	gpm	l/s	mm	m³	l	heures	
DTC-1	MURPHCO CYL-6	819	76,1	6	-	0,19	134	-	2814	4,88	CRÉPINE DUO PROCAST
DTC-2	MURPHCO CYL-6	866	80,5	6	-	0,2	137	-	3002	5,13	CRÉPINE DUO PROCAST
DTC-3	MURPHCO CYL-6	595	55,3	6	-	0,2	142	-	1963	3,12	CRÉPINE DUO PROCAST
DTC-4	MURPHCO CYL-6	718	66,7	6	-	0,16	94	-	2496	5,23	CRÉPINE DUO PROCAST
DTC-5	MURPHCO CYL-6	1405	130,5	6	-	0,19	136	-	5245	9,05	CRÉPINE DUO PROCAST
DTC-6	MURPHCO CYL-6	1246	115,8	6	-	0,2	146	-	4563	7,58	CRÉPINE DUO PROCAST
DTC-7	MURPHCO CYL-6	691	64,2	6	-	0,16	94	-	2383	4,98	CRÉPINE DUO PROCAST
DTC-8	MURPHCO CYL-6	1699	157,8	6	-	0,19	126	-	6483	11,62	CRÉPINE DUO PROCAST
DTC-9	MURPHCO CYL-6	2210	205,3	6	-	0,21	142	-	8536	13,52	CRÉPINE DUO PROCAST
DTC-10	MURPHCO CYL-6	1913	177,7	6	-	0,19	12	-	7365	12,92	CRÉPINE DUO PROCAST
DTC-11	MURPHCO CYL-6	1277	118,6	6	-	0,2	140	-	4704	7,98	CRÉPINE DUO PROCAST
DTC-12	MURPHCO CYL-6	1872	173,9	6	-	0,2	138	-	7181	12,28	CRÉPINE DUO PROCAST
DTC-13	MURPHCO CYL-6	1539	143	6	-	0,19	134	-	5807	10,1	CRÉPINE DUO PROCAST
DTC-14	MURPHCO CYL-6	785	72,9	6	-	0,17	99	-	2759	5,6	CRÉPINE DUO PROCAST
DTC-15	MURPHCO CYL-6	1578	146,6	6	-	0,19	124	-	5991	10,83	CRÉPINE DUO PROCAST
DTC-16	MURPHCO CYL-6	1435	133,3	6	-	0,18	122	-	5403	9,87	CRÉPINE DUO PROCAST
TOTAL		20648	1918,2		-	3,02			76695		

NOTES:

1.LES DÉBITS DES DRAINS DE TOIT ONT ÉTÉS CALCULÉS SELON L'OUVERTURE SÉLECTIONNÉE AVEC LES COURBES DU MANUFACTURIER. POUR TOUTE ÉQUIVALENCE SOUMISE À L'INGÉNIEUR, LES DÉBITS CALCULÉS DEVRONT ÊTRE RESPECTÉS.

2.LES NOUES ENTRE CHACUN DES BASSINS DE TOIT AURONT UNE HAUTEUR MAXIMALE DE 5½" (140mm) DE FAÇON À CE QUE CHACUN DES BASSINS PUISSE DÉBORDER VERS UN BASSIN ADJACENT.

COLONNES DE DRAINAGE PLUVIAL

COLONNES PLUVIAL DE 3" Ø		COLONNES PLUVIAL DE 4" Ø		COLONNES PLUVIAL DE 6" Ø	
CP-1	CP-9				
CP-2	CP-10				
CP-3	CP-11				
CP-4	CP-12				
CP-5	CP-13				
CP-6	CP-14				
CP-7	CP-15				
CP-8	CP-16				