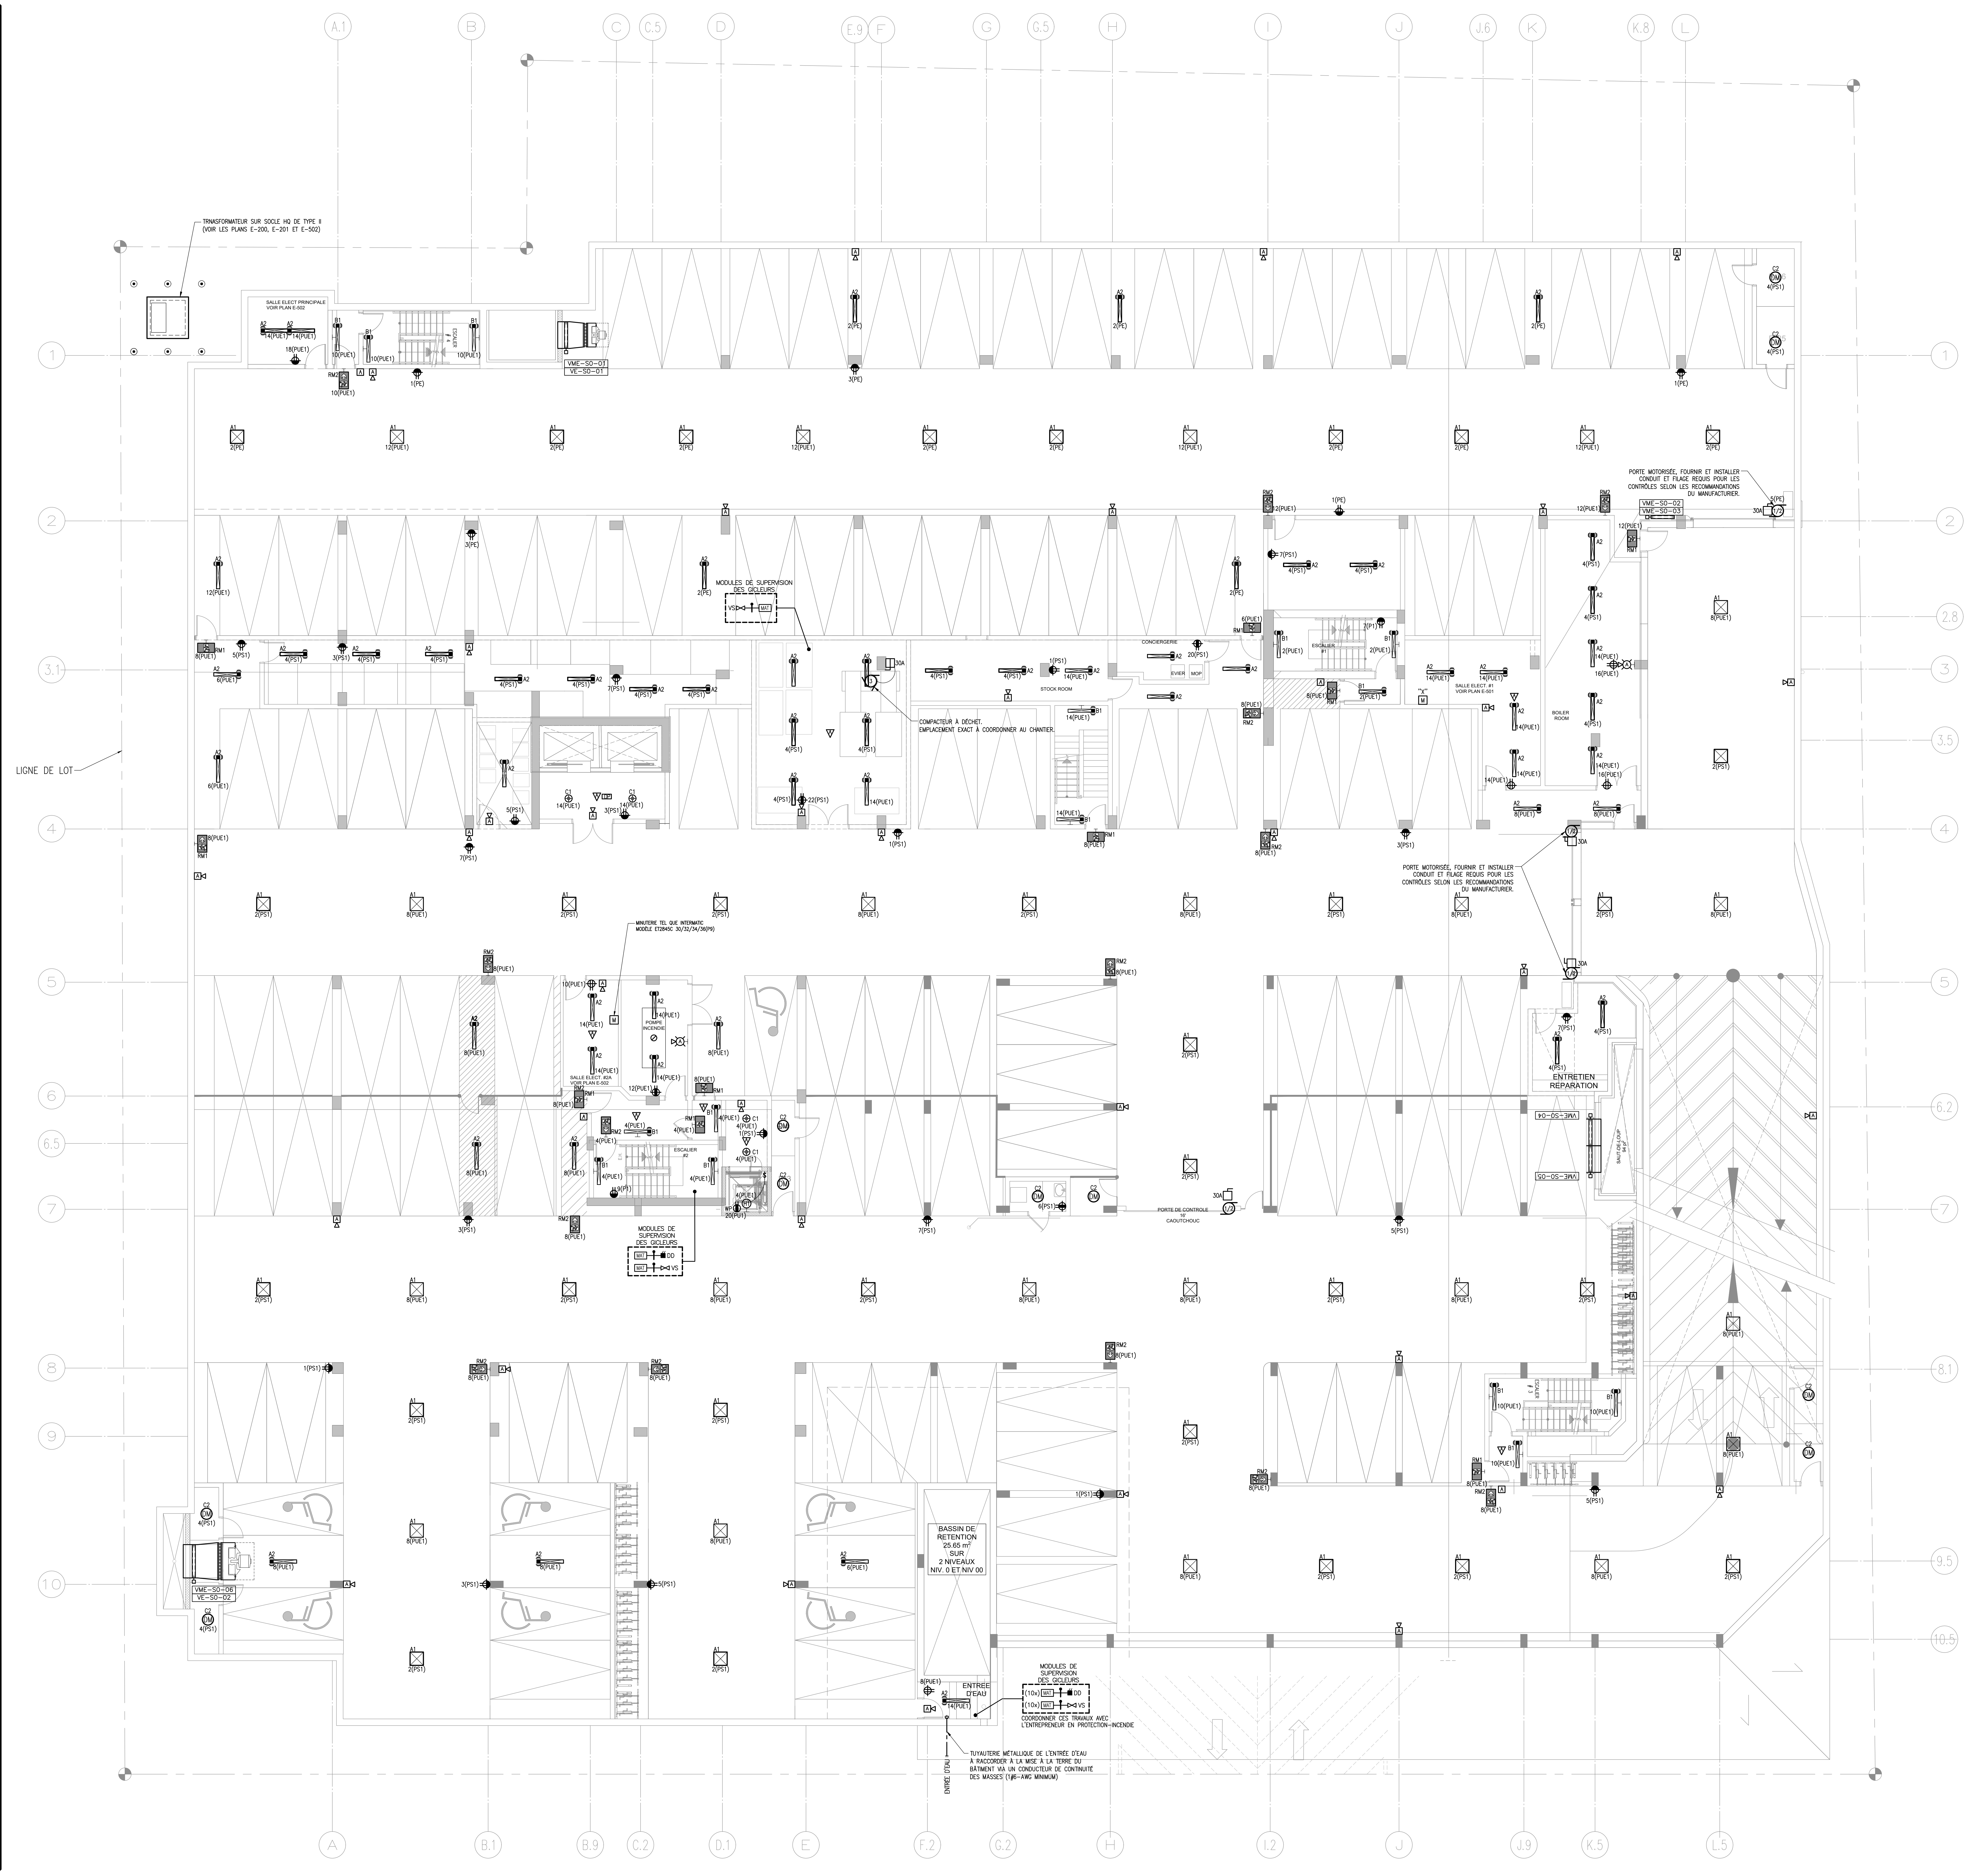
A.1
B
C
C.5
D
E.9
F
G
G.5
H
I
J
J.6
K
K.8
L
1
2
2.8
3
3.1
3.5
4
5
6
6.2
6.5
7
8
8.1
9
9.5
10
10.5
A
B.1
B.9
C.2
D.1
E
F.2
G.2
I.2
J.9
K.5
L.5
TRNASFORMATEUR SUR SOCLE HQ DE TYPE II (VOIR LES PLANS E-200, E-201 ET E-502)
SALLE ELECT PRINCIPALE VOIR PLAN E-502
ESCALIER # 4
VME-SO-01
VE-SO-01
LIGNE DE LOT
MODULES DE SUPERVISION DES GICLEURS
VS
MAT
DD
COMPACTEUR À DÉCHET. EMPLACEMENT EXACT À COORDONNER AU CHANTIER.
STOCK ROOM
CONCIERGERIE
EVIER
MOP
SALLE ELECT. #1 VOIR PLAN E-501
BOILER ROOM
PORTE MOTORISÉE, FOURNIR ET INSTALLER CONDUIT ET FILAGE REQUIS POUR LES CONTRÔLES SELON LES RECOMMANDATIONS DU MANUFACTURIER.
VME-SO-02
VME-SO-03
30A
1/2
MINUTERIE TEL QUE INTERMATIC MODÈLE ET2845C 30/32/34/36(P9)
POMPE INCENDIE
SALLE ELECT. #2A VOIR PLAN E-502
ESCALIER #2
ENTRETIEN REPARATION
VME-SO-04
VME-SO-05
SAUT-DE-LOUP 94 pi²
PORTE DE CONTROLE 16' CAOUTCHOUC
BASSIN DE RETENTION 25.65 m² SUR 2 NIVEAUX NIV. 0 ET NIV 00
ENTREE D'EAU
(10x)
COORDONNER CES TRAVAUX AVEC L'ENTREPRENEUR EN PROTECTION-INCENDIE
TUYAUTERIE MÉTALLIQUE DE L'ENTRÉE D'EAU À RACCORDER À LA MISE À LA TERRE DU BÂTIMENT VIA UN CONDUCTEUR DE CONTINUITÉ DES MASSES (1#6-AWG MINIMUM)
ENTRÉE D'EAU
VME-SO-06
VE-SO-02

NOTES

- LE BÂTIMENT EST PROTÉGÉ PAR UN SYSTÈME DE GICLEURS AUTOMATIQUE.

NOTES SPÉCIFIQUES

1– LE VENTILATEUR S'ARRÊTE AU DÉCLENCHEMENT D'UNE ALARME–INCENDIE.

2– SIGNAL VERS PANNEAU D'ALARME–INCENDIE.

NOTES CONTRÔLE D'ÉCLAIRAGE

- L'ÉCLAIRAGE DANS LE GARAGE DE STATIONNEMENT DOIT ÊTRE DIVISÉ EN ZONES D'AU PLUS 360M².
- L'ÉCLAIRAGE DU GARAGE DE STATIONNEMENT DOIT ÊTRE CONTRÔLÉE PAR UN DISPOSITIF QUI RÉDUIT AUTOMATIQUEMENT LA PUISSANCE DE CHAQUE APPAREIL D'ÉCLAIRAGE DE LA ZONE D'AU MOINS 30% LORSQU'AUCUNE ACTIVITÉ N'Y EST DÉTECTÉE PENDANT 20 MINUTES.
- L'ÉCLAIRAGE DE L'ENTRÉE POUR VÉHICULES DES GARAGES DE STATIONNEMENT DOIT ÊTRE COMMANDÉ SÉPARÉMENT PAR UN DISPOSITIF QUI RÉDUIT AUTOMATIQUEMENT L'ÉCLAIRAGE D'AU MOINS 50% ENTRE LE COUCHER ET LE LEVER DU SOLEIL.
- L'ÉCLAIRAGE EXTÉRIEUR DOIT ÊTRE COMMANDÉ SÉPARÉMENT PAR UN DISPOSITIF QUI ALLUME AUTOMATIQUEMENT L'ÉCLAIRAGE À 100% AU COUCHER DU SOLEIL ET AU LEVER DU SOLEIL L'ÉCLAIRAGE S'ÉTEINT.

IDENTIFICATIONS BORNE DE RECHARGE

1 PRÉVOIR UN CONDUIT VIDE DE 27mm POUR BORNE DE RECHARGE FUTURE JUSQU'À LA SALLE ÉLECTRIQUE. COORDONNER L'EMPLACEMENT EXACT AU CHANTIER AVEC LE CLIENT AVANT LE DÉBUT DES TRAVAUX.

2 PRÉVOIR LE RACCORDEMENT POUR BORNE DE RECHARGE JUSQU'À LA SALLE ÉLECTRIQUE. COORDONNER L'EMPLACEMENT EXACT AU CHANTIER AVEC LE CLIENT AVANT LE DÉBUT DES TRAVAUX. MODÈLE PULSAR PLUS 40A–2P (NIVEAU 2) DE WALLBOX C/A TOUS LES ACCESSOIRES REQUIS POUR UNE INSTALLATION CONFORME AUX RECOMMANDATION DU MANUFACTURIER.

- LA HAUTEUR D'INSTALLATION DES BORNES DE RECHARGE POUR VOITURE ÉLECTRIQUE EST DE 48'' CENTRE/CENTRE.