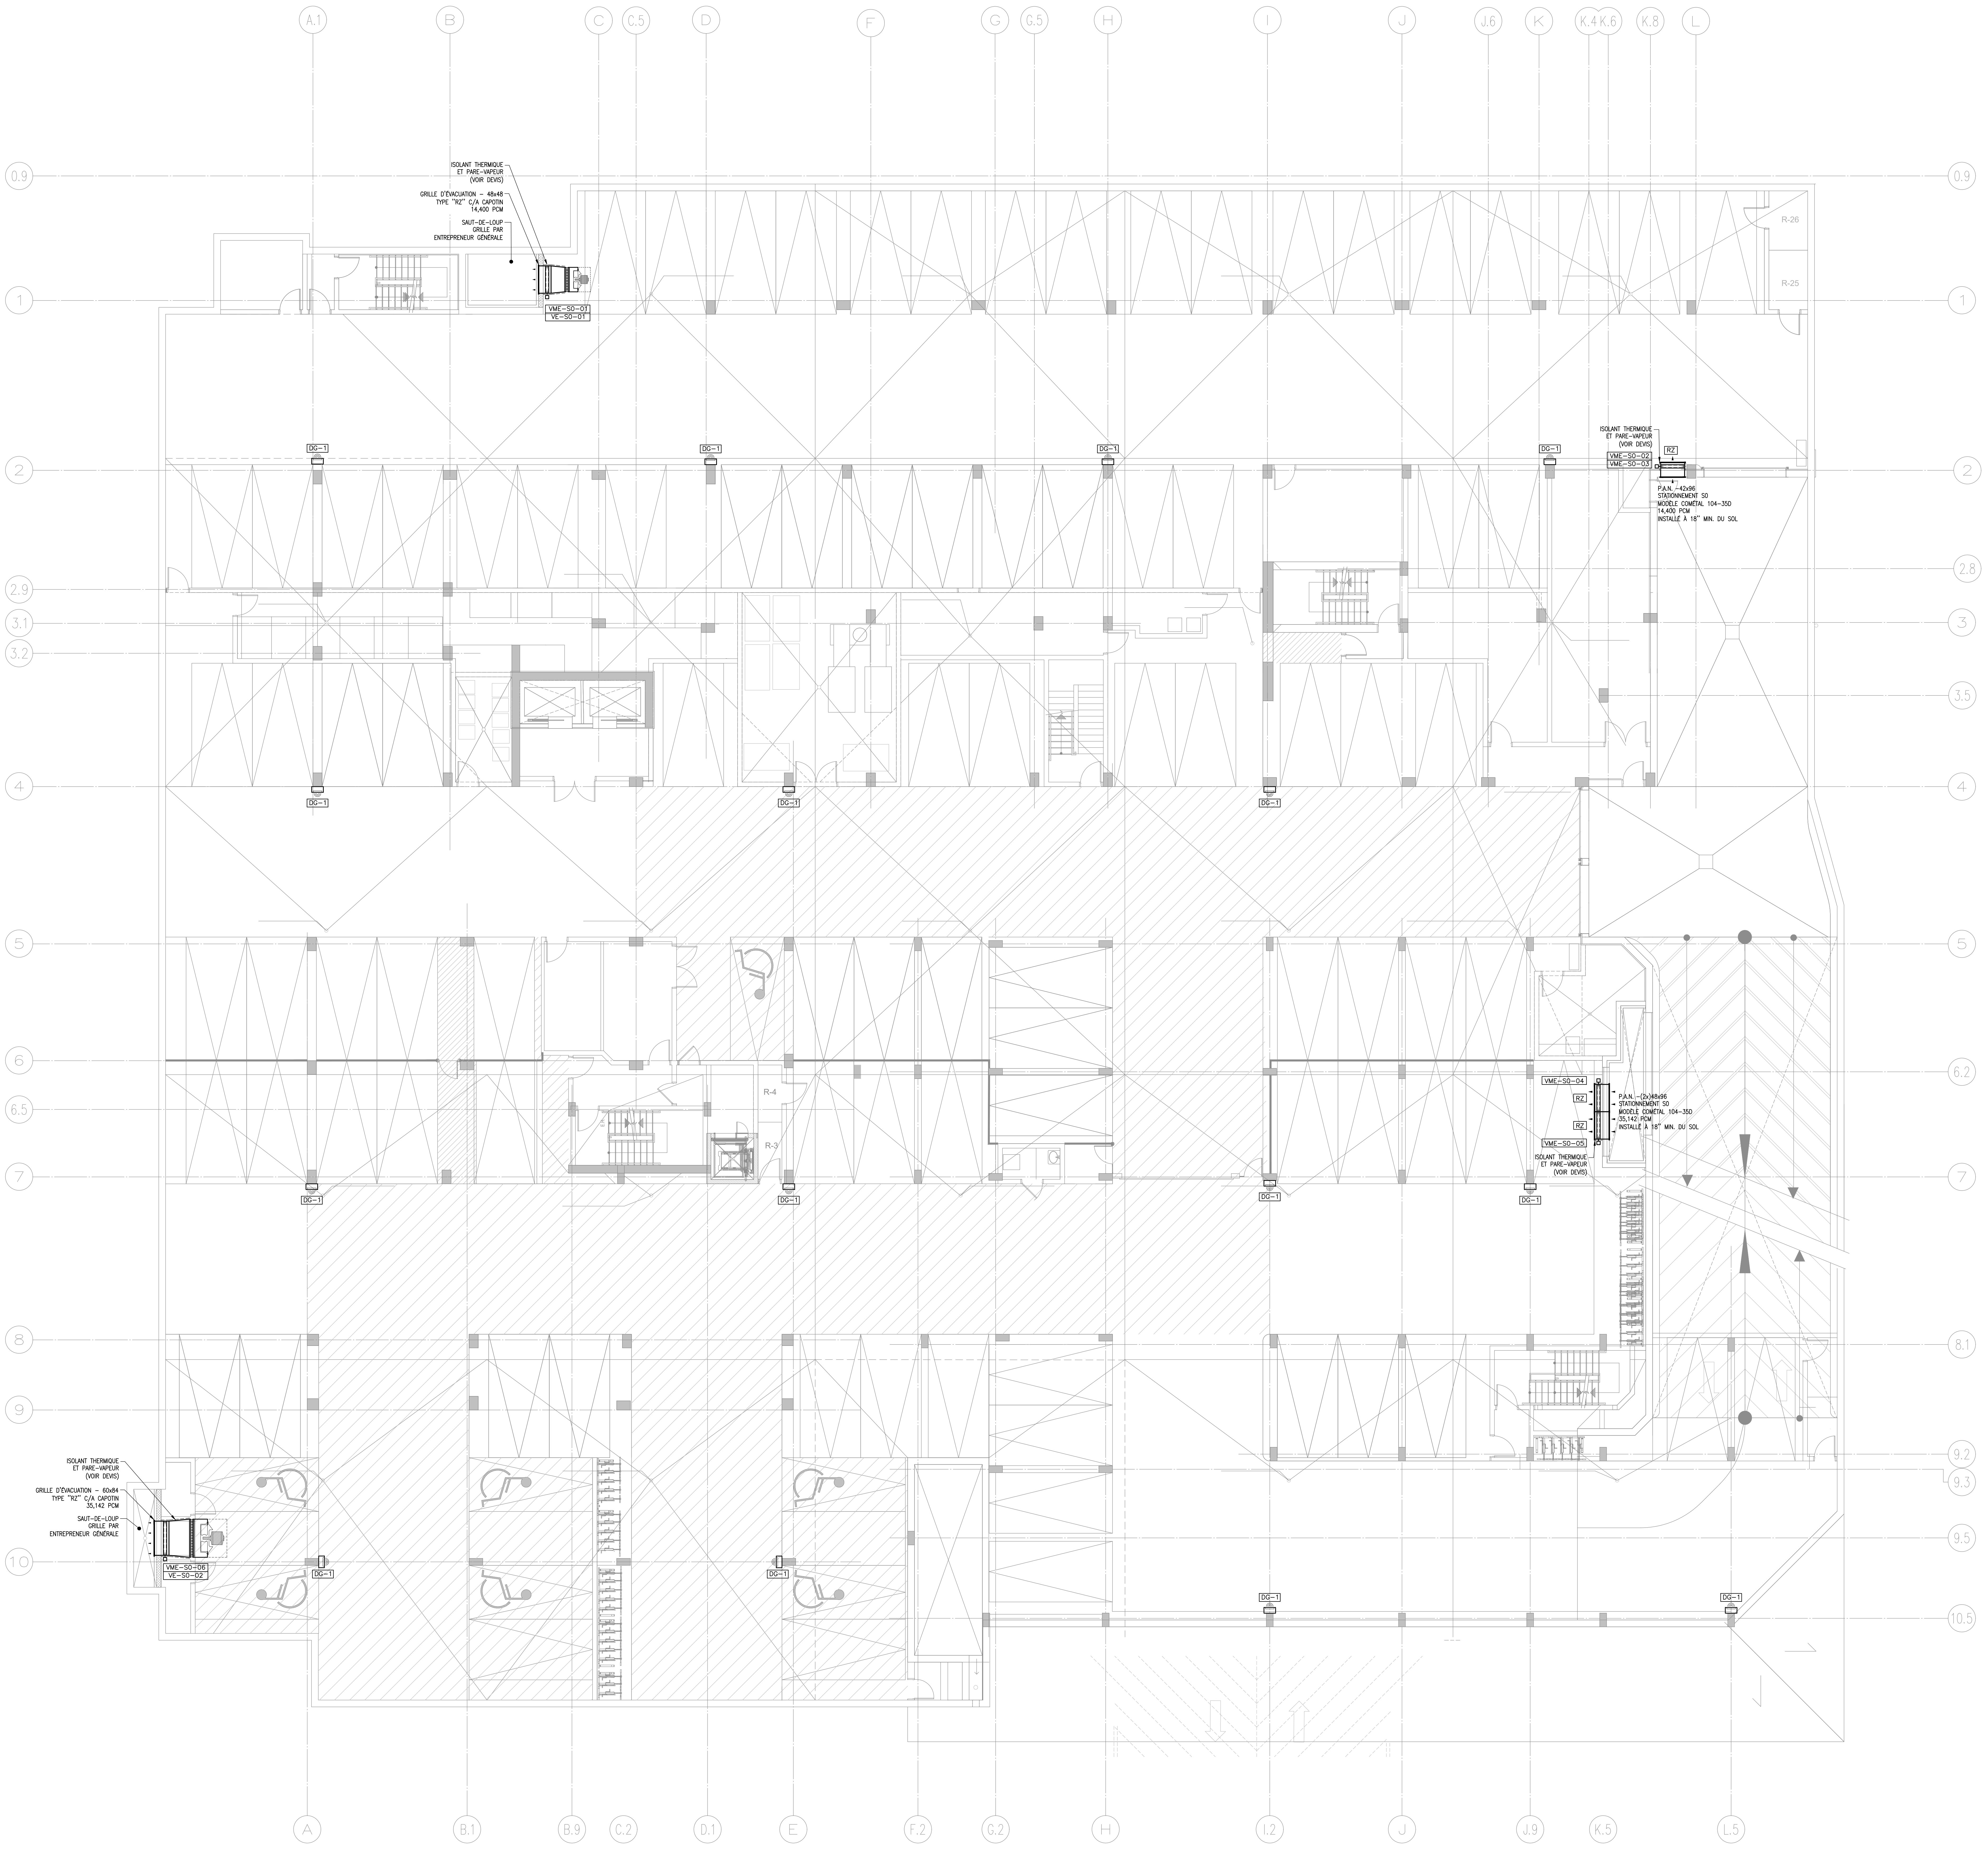
A.1
B
C
C.5
D
F
G
G.5
H
I
J
J.6
K
K.4
K.6
K.8
L
0.9
1
2
2.8
2.9
3
3.1
3.2
3.5
4
5
6
6.2
6.5
7
8
8.1
9
9.2
9.3
9.5
10
10.5
A
B.1
B.9
C.2
D.1
E
F.2
G.2
H
I.2
J
J.9
K.5
L.5
ISOLANT THERMIQUE ET PARE-VAPEUR (VOIR DEVIS)
GRILLE D'ÉVACUATION – 48x48 TYPE "RZ" C/A CAPOTIN 14,400 PCM
SAUT-DE-LOUP GRILLE PAR ENTREPRENEUR GÉNÉRALE
VME-S0-01
VE-S0-01
R-26
R-25
DG-1
ISOLANT THERMIQUE ET PARE-VAPEUR (VOIR DEVIS)
VME-S0-02
VME-S0-03
RZ
P.A.N. –42x96 STATIONNEMENT S0 MODÈLE COMÉTAL 104-35D 14,400 PCM INSTALLÉ À 18" MIN. DU SOL
R-4
R-3
VME-S0-04
RZ
RZ
VME-S0-05
P.A.N. –(2x)48x96 STATIONNEMENT S0 MODÈLE COMÉTAL 104-35D 35,142 PCM INSTALLÉ À 18" MIN. DU SOL
ISOLANT THERMIQUE ET PARE-VAPEUR (VOIR DEVIS)
ISOLANT THERMIQUE ET PARE-VAPEUR (VOIR DEVIS)
GRILLE D'ÉVACUATION – 60x84 TYPE "RZ" C/A CAPOTIN 35,142 PCM
SAUT-DE-LOUP GRILLE PAR ENTREPRENEUR GÉNÉRALE
VME-S0-06
VE-S0-02