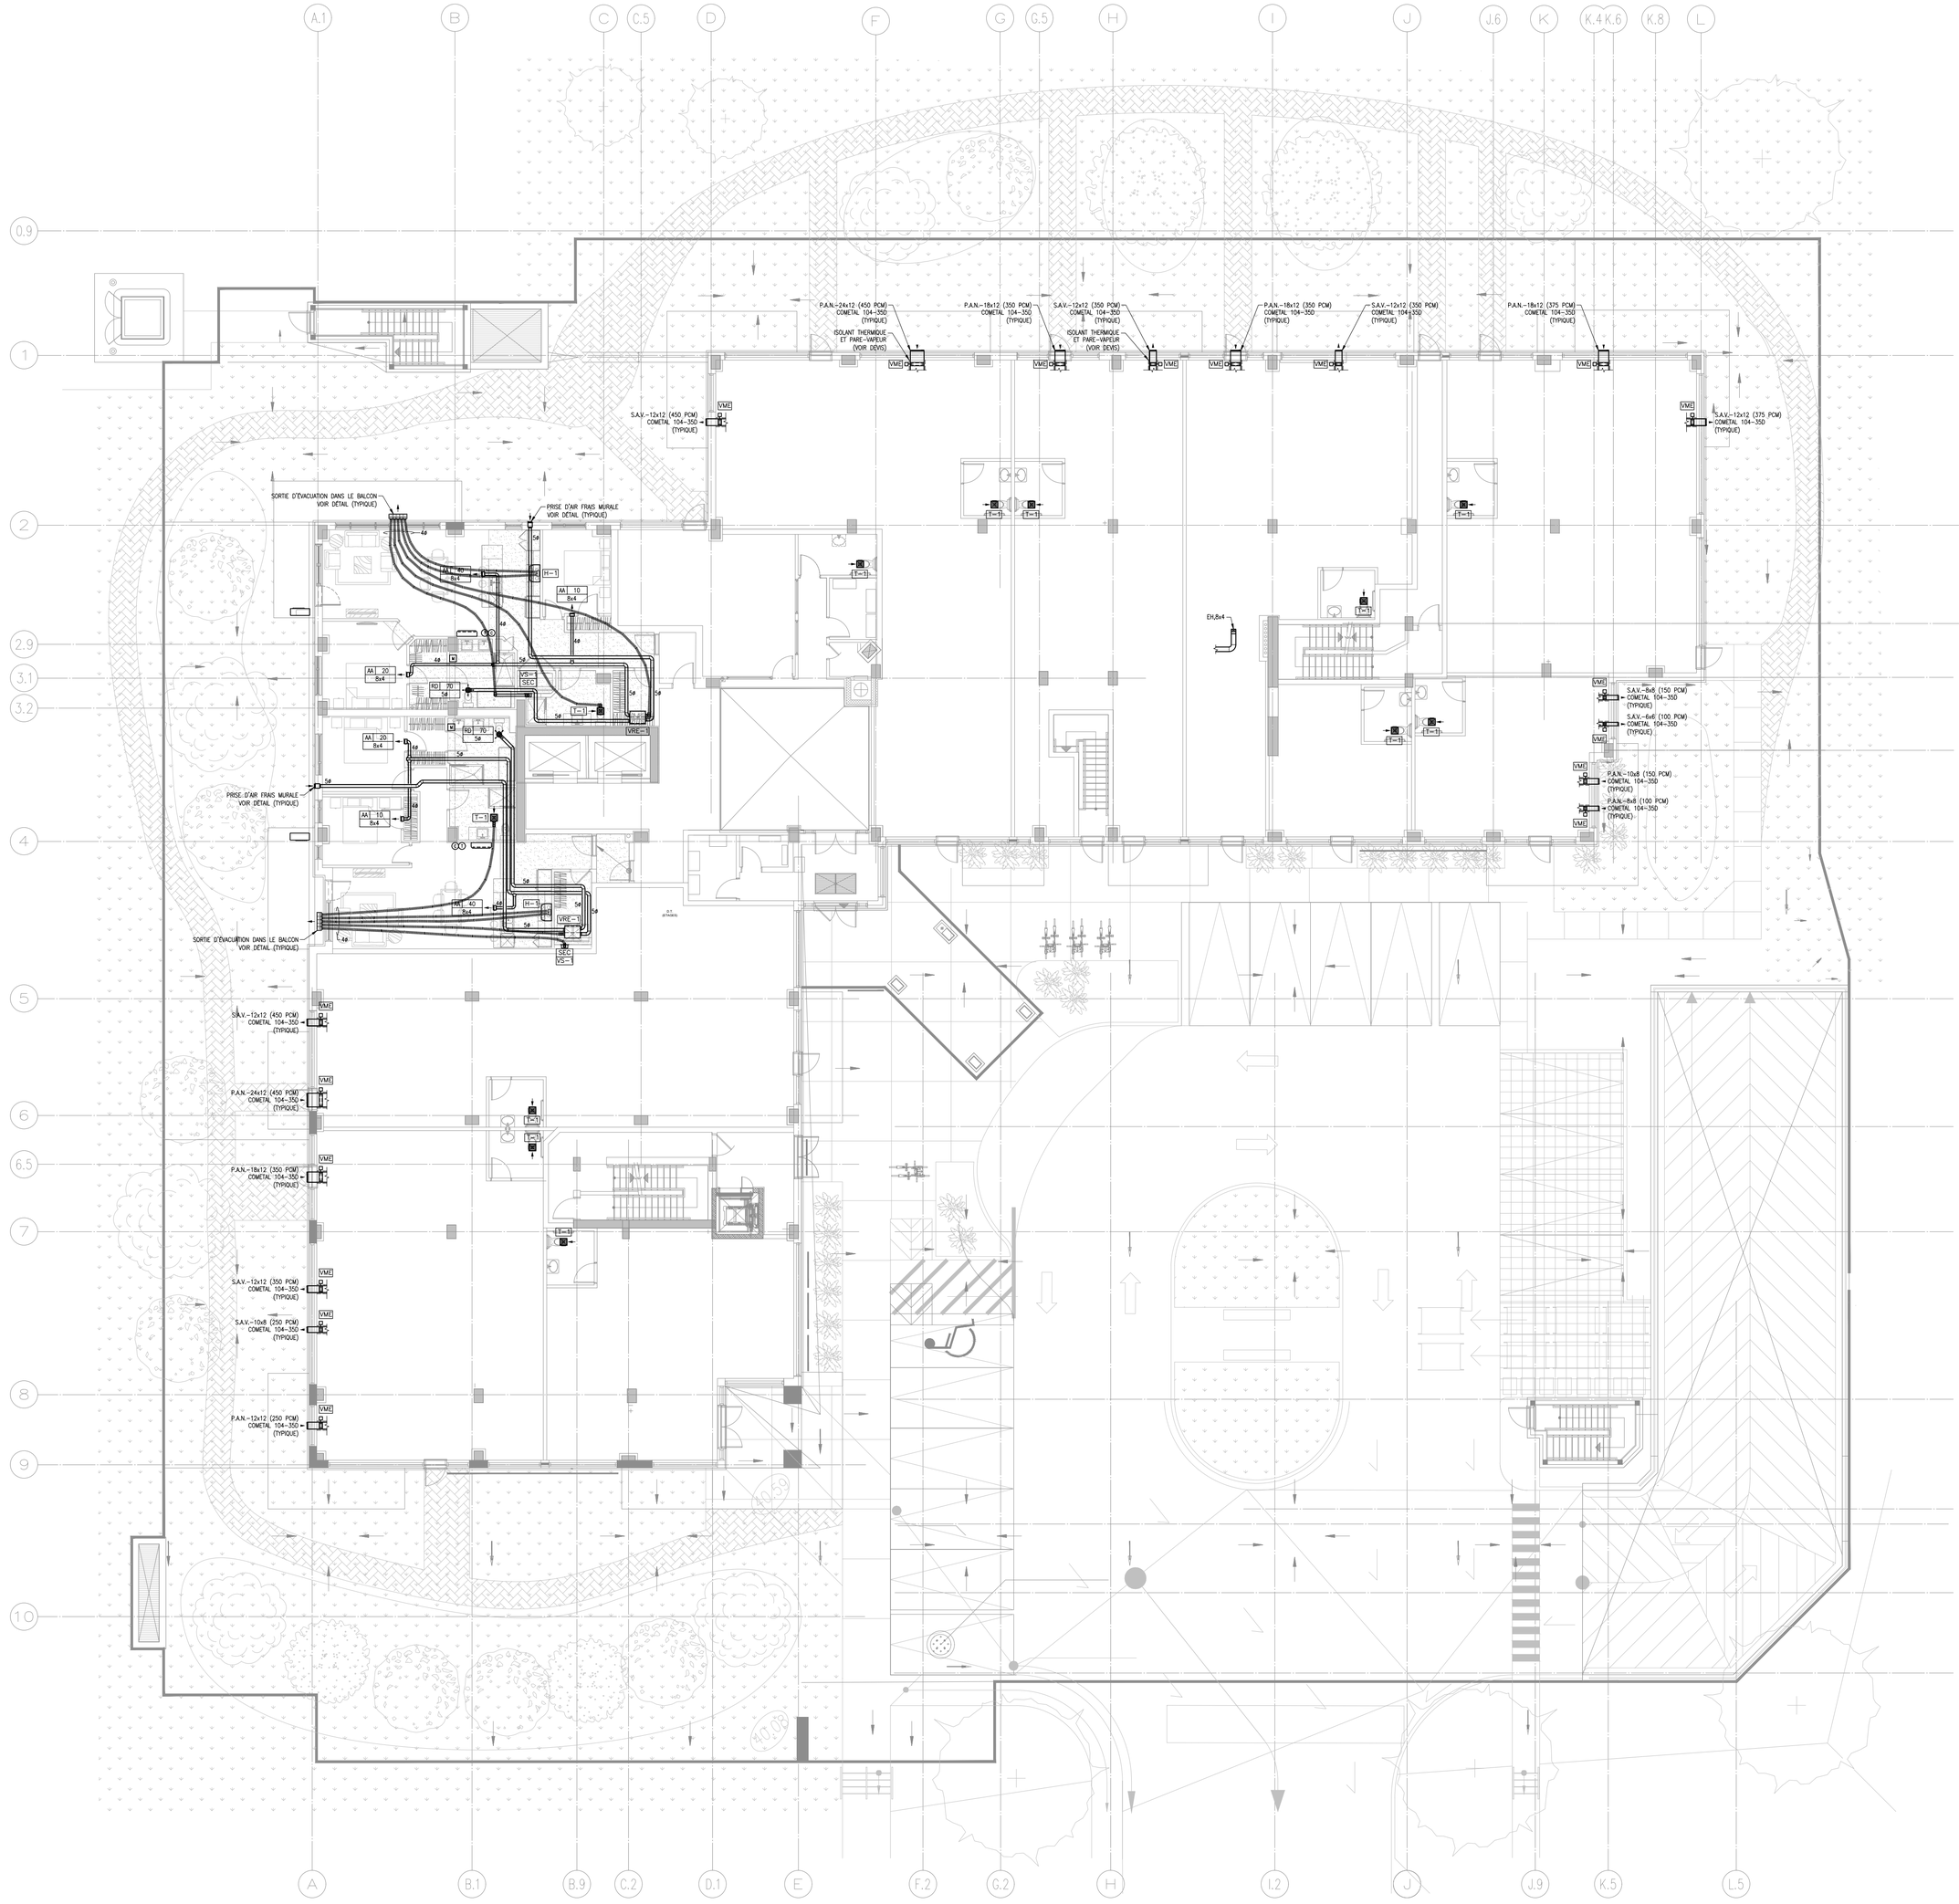

A.1
B
C
C.5
D
F
G
G.5
H
I
J
J.6
K
K.4 K.6
K.8
L
0.9
1
2
2.9
3.1
3.2
4
5
6
6.5
7
8
9
10
A
B.1
B.9
C.2
D.1
E
F.2
G.2
H
I.2
J
J.9
K.5
L.5
P.A.N.–24x12 (450 PCM) COMETAL 104–350 (TYPIQUE)
ISOLANT THERMIQUE ET PARE–VAPEUR (VOIR DEVIS)
P.A.N.–18x12 (350 PCM) COMETAL 104–350 (TYPIQUE)
S.A.V.–12x12 (350 PCM) COMETAL 104–350 (TYPIQUE)
P.A.N.–18x12 (375 PCM) COMETAL 104–350 (TYPIQUE)
S.A.V.–12x12 (450 PCM) COMETAL 104–350 (TYPIQUE)
S.A.V.–12x12 (375 PCM) COMETAL 104–350 (TYPIQUE)
SORTIE D'ÉVACUATION DANS LE BALCON VOIR DÉTAIL (TYPIQUE)
PRISE D'AIR FRAIS MURALE VOIR DÉTAIL (TYPIQUE)
EH,8x4
S.A.V.–8x8 (150 PCM) COMETAL 104–350 (TYPIQUE)
S.A.V.–6x6 (100 PCM) COMETAL 104–350 (TYPIQUE)
P.A.N.–10x8 (150 PCM) COMETAL 104–350 (TYPIQUE)
P.A.N.–8x8 (100 PCM) COMETAL 104–350 (TYPIQUE)
S.A.V.–12x12 (350 PCM) COMETAL 104–350 (TYPIQUE)
S.A.V.–10x8 (250 PCM) COMETAL 104–350 (TYPIQUE)
P.A.N.–12x12 (250 PCM) COMETAL 104–350 (TYPIQUE)
VME
VRE–1
VS–1
SEC
H–1
T–1
RD 70
AA 10 8x4
AA 20 8x4
AA 40 8x4
40.09
40.08