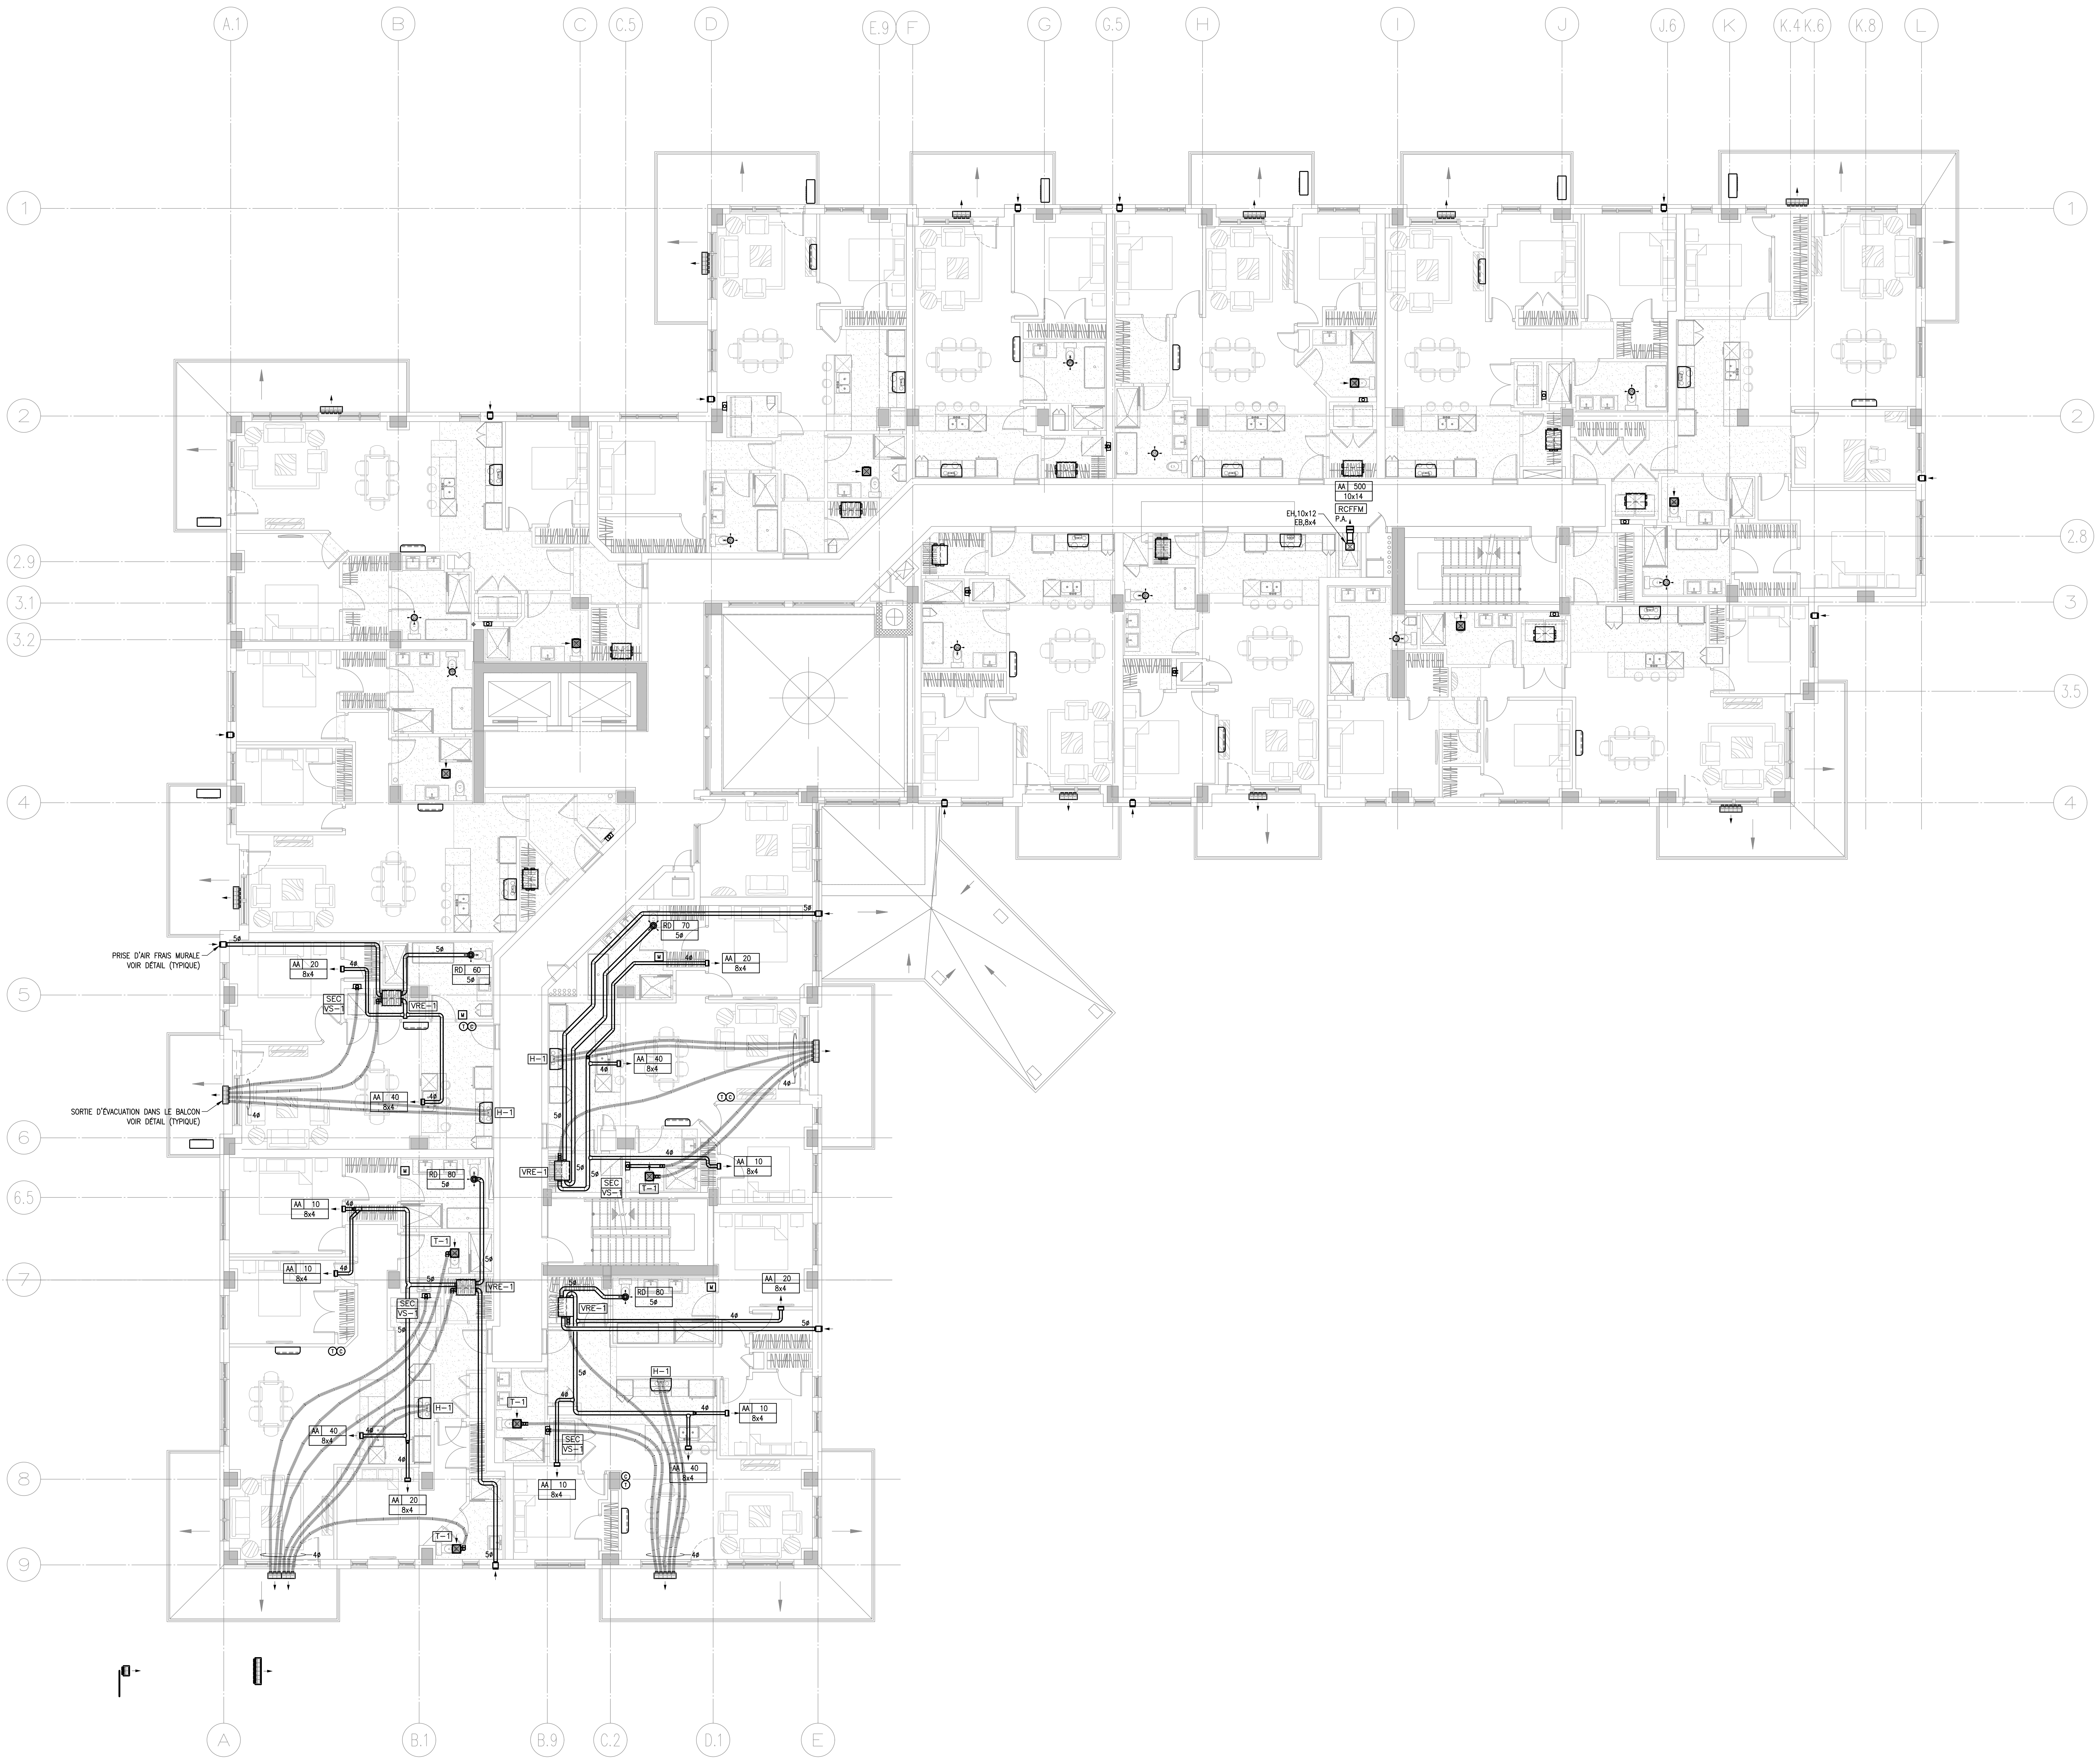
A.1
B
C
C.5
D
E.9
F
G
G.5
H
I
J
J.6
K
K.4
K.6
K.8
L
1
2
2.8
2.9
3
3.1
3.2
3.5
4
5
6
6.5
7
8
9
A
B.1
B.9
C.2
D.1
E
AA 500
10x14
RCFFM
P.A.
EH,10x12
EB,8x4
PRISE D'AIR FRAIS MURALE
VOIR DÉTAIL (TYPIQUE)
SORTIE D'ÉVACUATION DANS LE BALCON
VOIR DÉTAIL (TYPIQUE)
AA 20
8x4
RD 60
5ø
SEC
VS-1
VRE-1
AA 40
8x4
H-1
RD 80
5ø
AA 10
8x4
T-1
RD 70
5ø
M
T
C
5ø
4ø