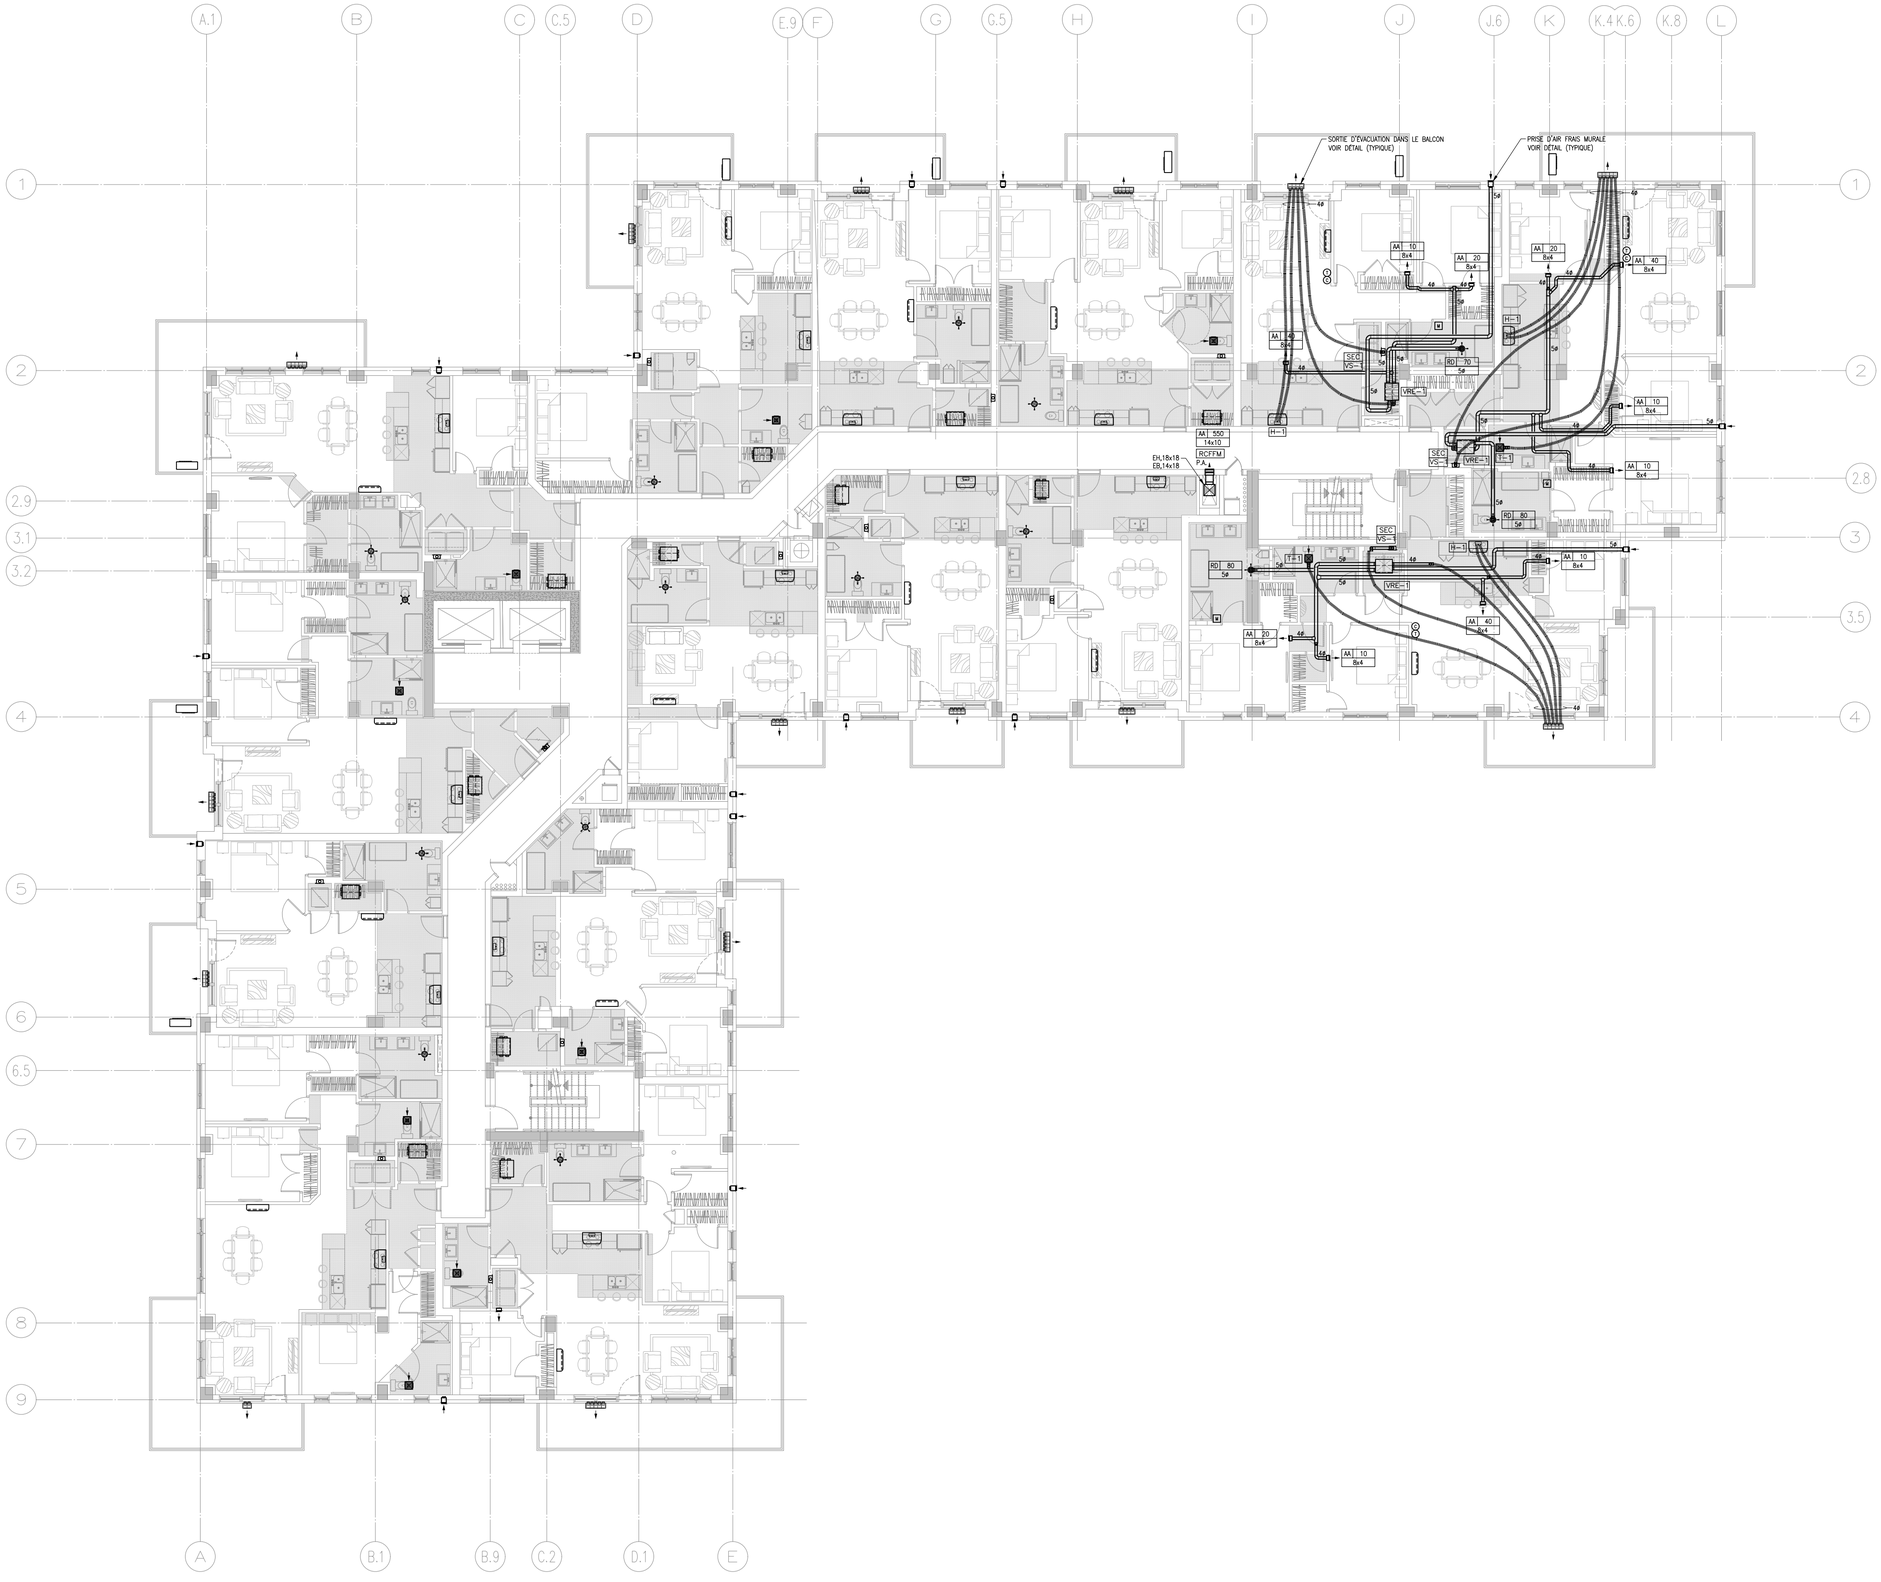

A.1
B
C
C.5
D
E.9
F
G
G.5
H
I
J
J.6
K
K.4
K.6
K.8
L
1
2
2.9
3.1
3.2
4
5
6
6.5
7
8
9
A
B.1
B.9
C.2
D.1
E
2
2.8
3
3.5
4
SORTIE D'ÉVACUATION DANS LE BALCON
VOIR DÉTAIL (TYPIQUE)
PRISE D'AIR FRAIS MURALE
VOIR DÉTAIL (TYPIQUE)
AA 10 8x4
AA 20 8x4
AA 40 8x4
AA 550 14x10
RCFFM
EH.18x18
EB.14x18
SEC VS-1
VRE-1
VRL-1
H-1
RD 70 5ø
RD 80 5ø
TF-1