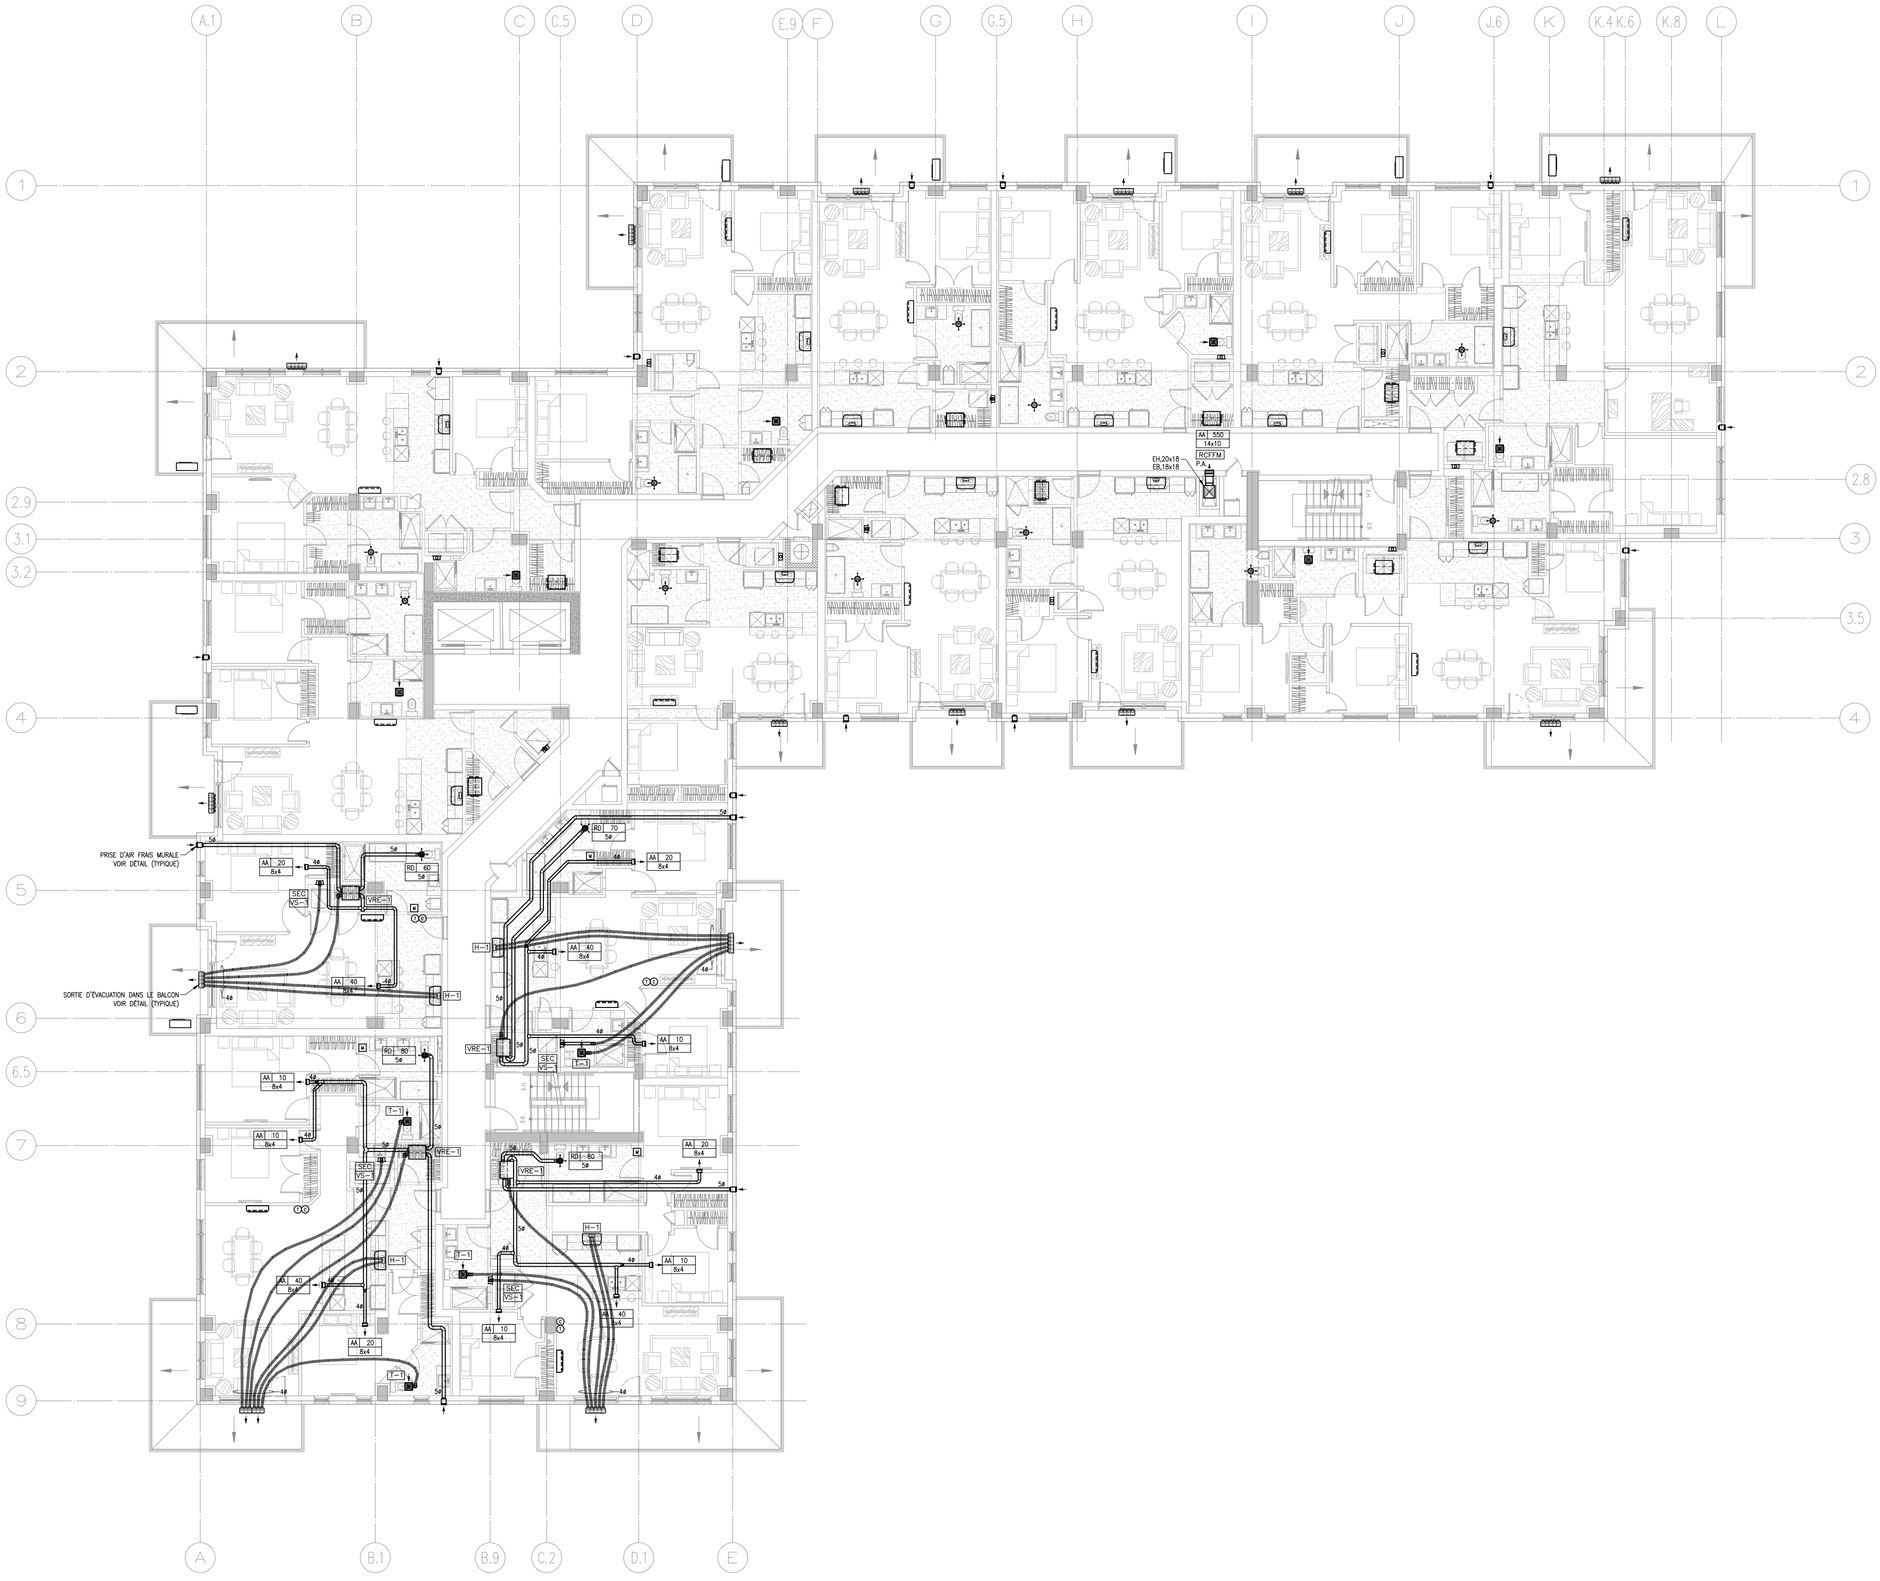

A.1
B
C
C.5
D
E.9
F
G
G.5
H
I
J
J.6
K
K.4
K.6
K.8
L
1
2
2.9
3.1
3.2
4
5
6
6.5
7
8
9
2.8
3
3.5
A
B.1
B.9
C.2
D.1
E
AA 550
14x10
RC/FFM
EH.20x18
EB.18x18
PRISE D'AIR FRAIS MURALE
VOIR DÉTAIL (TYPIQUE)
SORTIE D'ÉVACUATION DANS LE BALCON
VOIR DÉTAIL (TYPIQUE)
AA 20 8x4
AA 40 8x4
AA 10 8x4
RD 60 5ø
RD 70 5ø
RD 80 5ø
RD 80 10 5ø
SEC VS-1
VRE-1
H-1
T-1