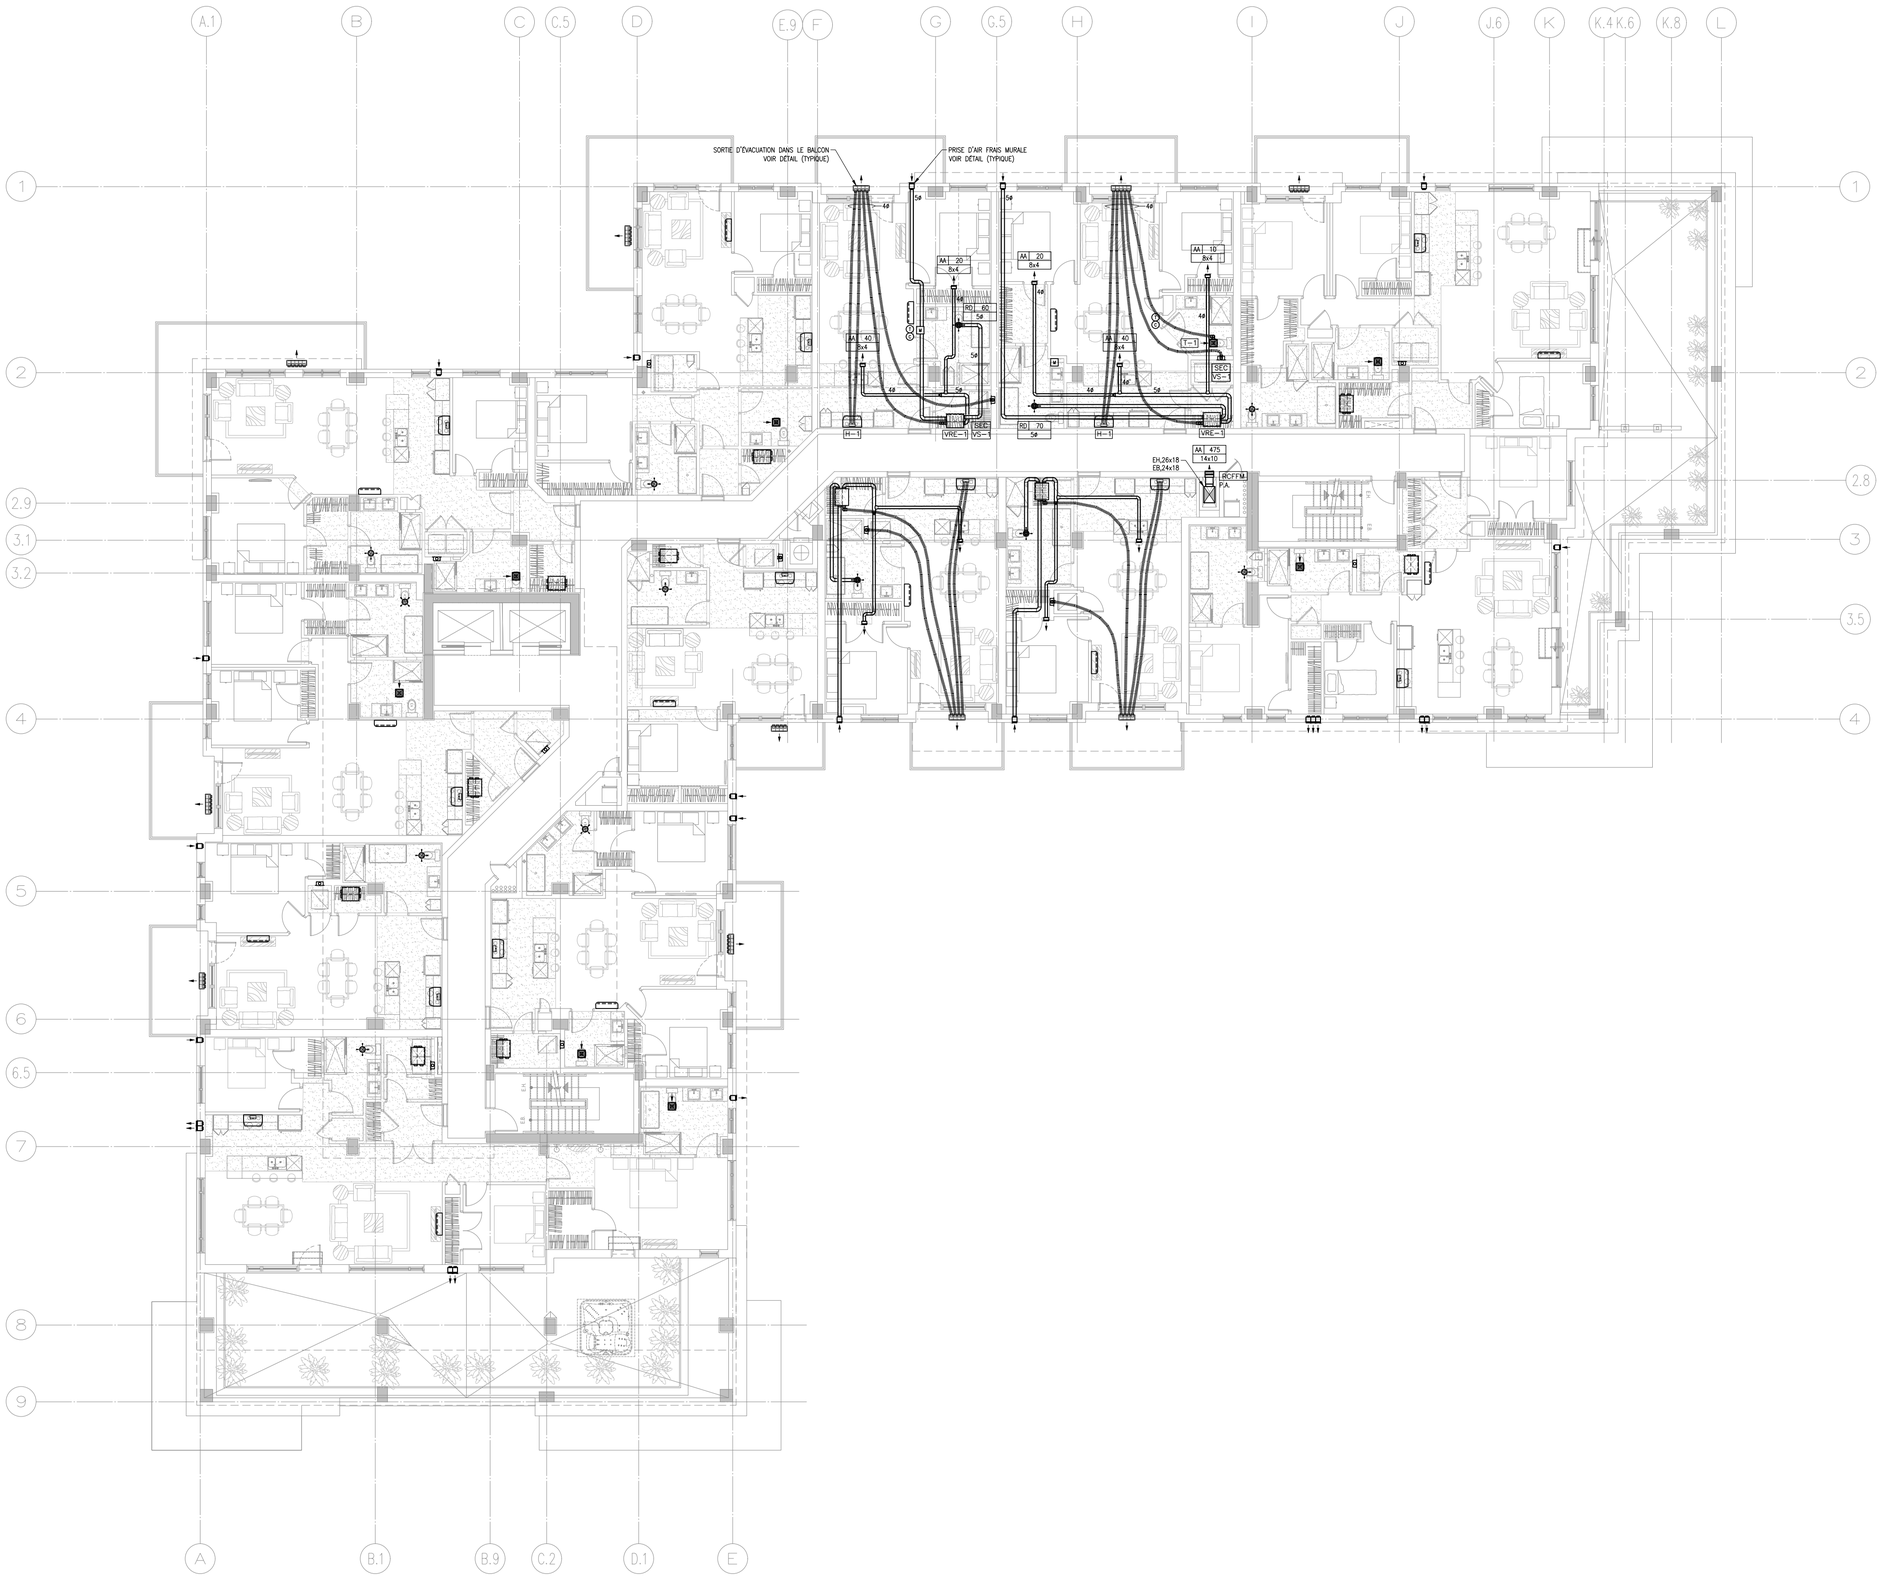

SORTIE D'EVACUATION DANS LE BALCON
VOIR DÉTAIL (TYPIQUE)
PRISE D'AIR FRAIS MURALE
VOIR DÉTAIL (TYPIQUE)
AA 20 8x4
AA 10 8x4
AA 40 8x4
AA 475 14x10
RO 60
RO 70
T-1
H-1
VRE-1
VS-1
EH.26x18
EB.24x18
RCFFM
P.A.
A.1
B
C
C.5
D
E.9
F
G
G.5
H
I
J
J.6
K
K.4
K.6
K.8
L
1
2
2.8
2.9
3
3.1
3.2
3.5
4
5
6
6.5
7
8
9
A
B.1
B.9
C.2
D.1
E