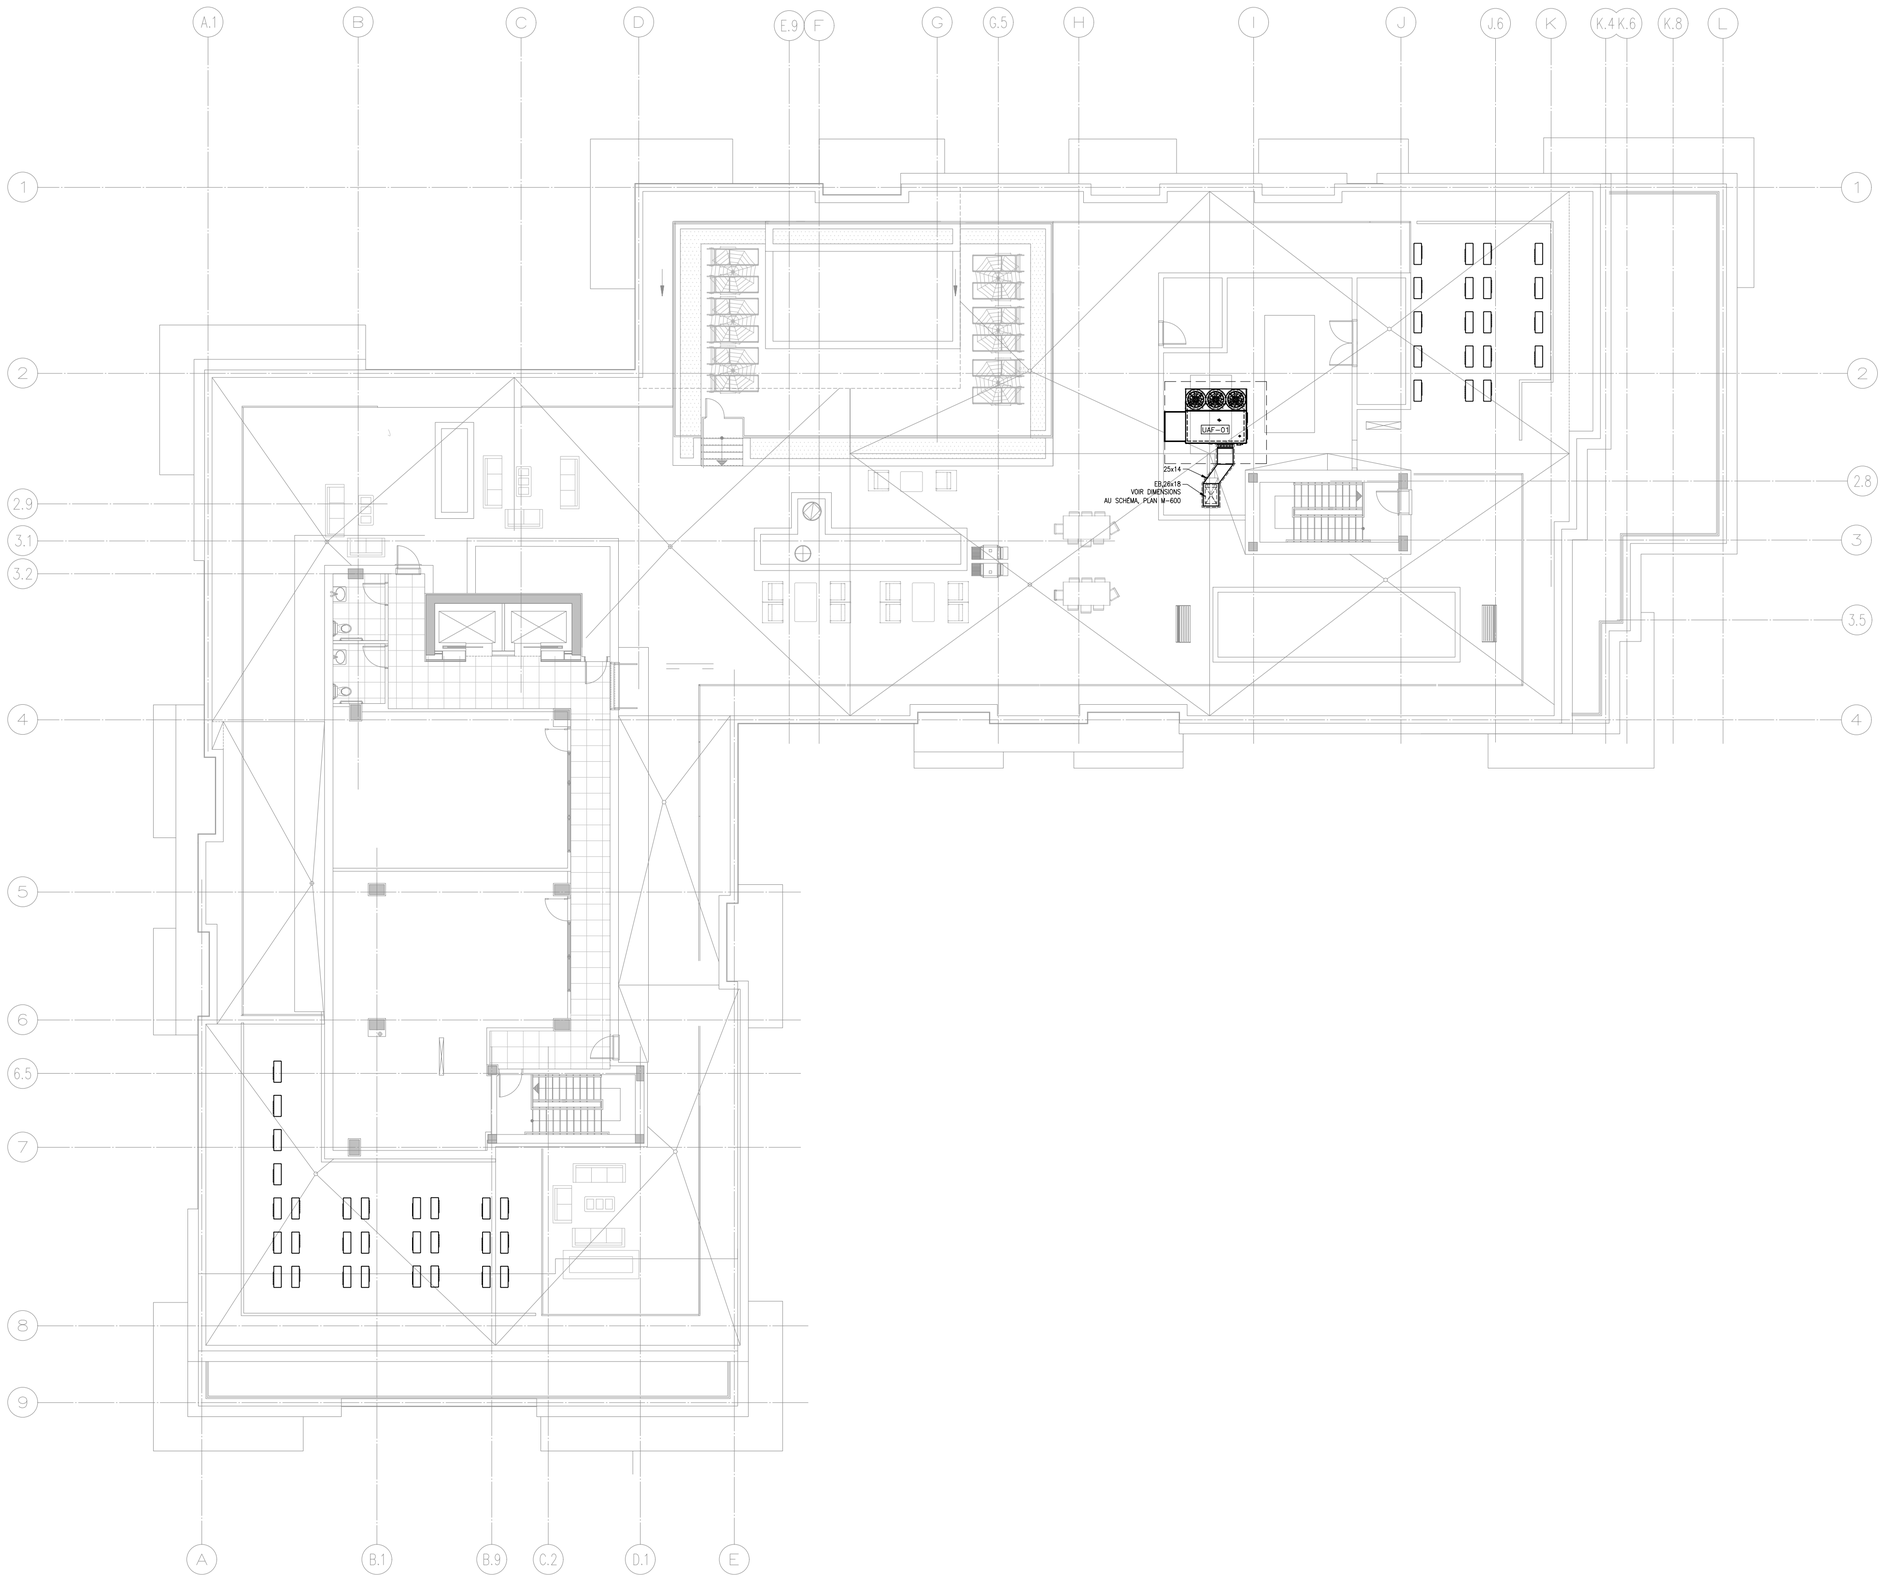

A.1
B
C
D
E.9
F
G
G.5
H
I
J
J.6
K
K.4
K.6
K.8
L
1
2
2.9
3.1
3.2
4
5
6
6.5
7
8
9
A
B.1
B.9
C.2
D.1
E
2
2.8
3
3.5
4
1
UAF-03
25x14
EB,26x18
VOIR DIMENSIONS
AU SCHÉMA, PLAN M-600